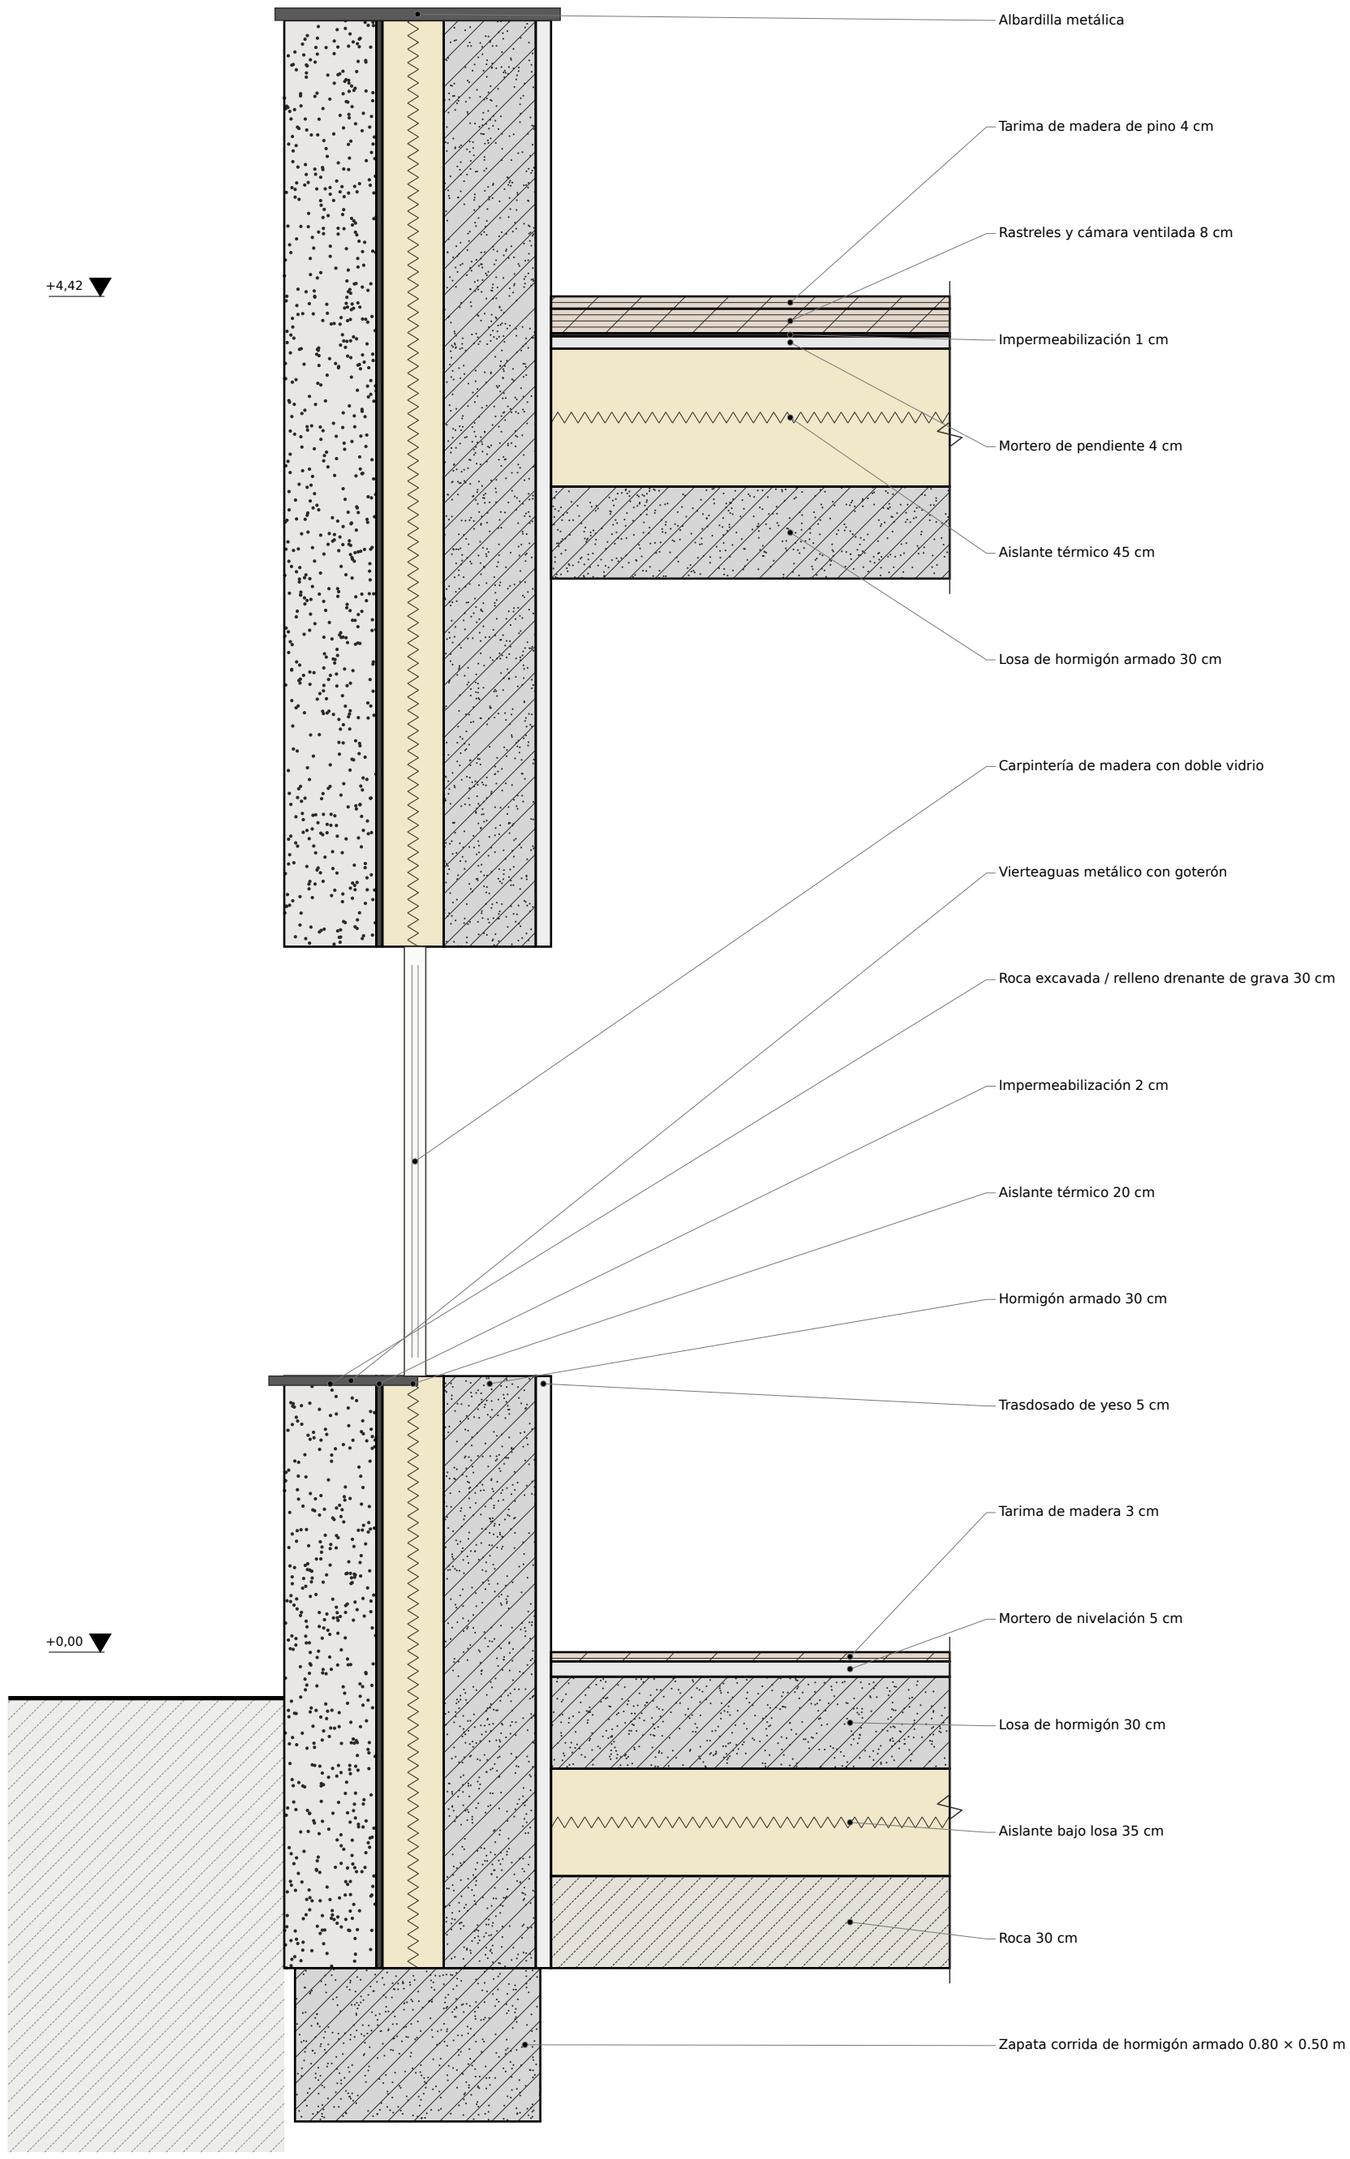


DETALLE CONSTRUCTIVO

E 1:20

CASO_021 · PROPUESTA A	E 1:20	**D01**
SECCIÓN CONSTRUCTIVA DEL MURO TRASERO Y LA CUBIERTA-TERRAZA	Anteproyecto	