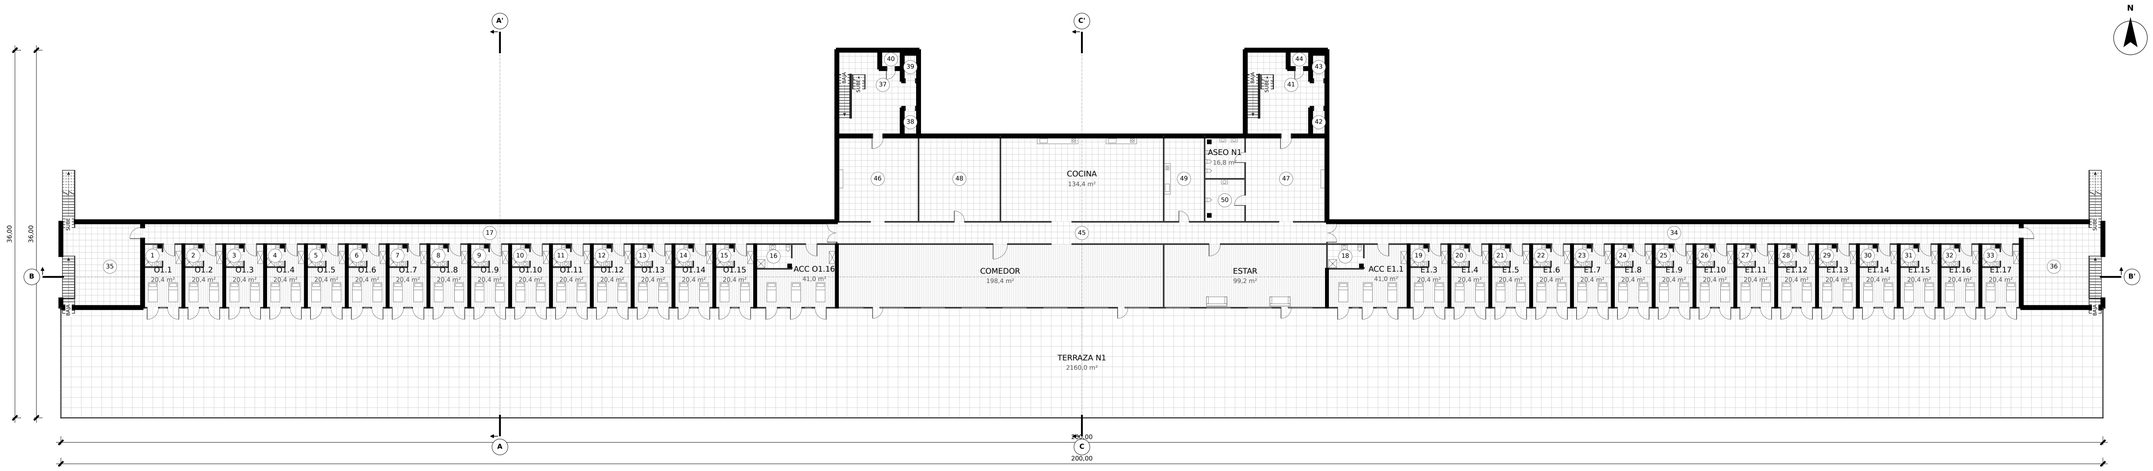


PLANTA N1 · COMEDOR, ESTAR Y COCINA

E 1:300

0 2 5 10 20 m

1 Baño O1.1 · 4,4 m²
2 Baño O1.2 · 4,4 m²
3 Baño O1.3 · 4,4 m²
4 Baño O1.4 · 4,4 m²
5 Baño O1.5 · 4,4 m²
6 Baño O1.6 · 4,4 m²
7 Baño O1.7 · 4,4 m²
8 Baño O1.8 · 4,4 m²
9 Baño O1.9 · 4,4 m²
10 Baño O1.10 · 4,4 m²
11 Baño O1.11 · 4,4 m²
12 Baño O1.12 · 4,4 m²
13 Baño O1.13 · 4,4 m²
14 Baño O1.14 · 4,4 m²
15 Baño O1.15 · 4,4 m²
16 Baño Acc O1.16 · 8,6 m²
17 Pasillo O1 · 149,6 m²
18 Baño Acc E1.1 · 8,6 m²
19 Baño E1.3 · 4,4 m²
20 Baño E1.4 · 4,4 m²
21 Baño E1.5 · 4,4 m²
22 Baño E1.6 · 4,4 m²
23 Baño E1.7 · 4,4 m²
24 Baño E1.8 · 4,4 m²
25 Baño E1.9 · 4,4 m²
26 Baño E1.10 · 4,4 m²
27 Baño E1.11 · 4,4 m²
28 Baño E1.12 · 4,4 m²
29 Baño E1.13 · 4,4 m²
30 Baño E1.14 · 4,4 m²
31 Baño E1.15 · 4,4 m²
32 Baño E1.16 · 4,4 m²
33 Baño E1.17 · 4,4 m²
34 Pasillo E1 · 149,6 m²
35 Escalera de evacuación O1 · 61,6 m²
36 Escalera de evacuación E1 · 61,6 m²
37 Escalera protegida O1 · 57,2 m²
38 Ascensor · 4,3 m²
39 Ascensor de servicio · 4,3 m²
40 Cuarto de limpieza O1 · 4,0 m²
41 Escalera protegida E1 · 57,2 m²
42 Ascensor · 4,3 m²
43 Ascensor de servicio · 4,3 m²
44 Cuarto de limpieza E1 · 4,0 m²
45 Pasillo central 1 · 105,6 m²
46 Vestíbulo de comedor O · 67,2 m²
47 Vestíbulo de comedor E · 67,2 m²
48 Despensa y cámaras · 67,2 m²
49 Oficio y fregadero · 33,6 m²
50 Aseo accesible N1 · 16,8 m²

CASO_021 · PROPUESTA A

PLANTA N1 · COMEDOR, ESTAR Y COCINA

E 1:300

Anteproyecto

P02