

A · Planta 1: plano del claro sobre pilar

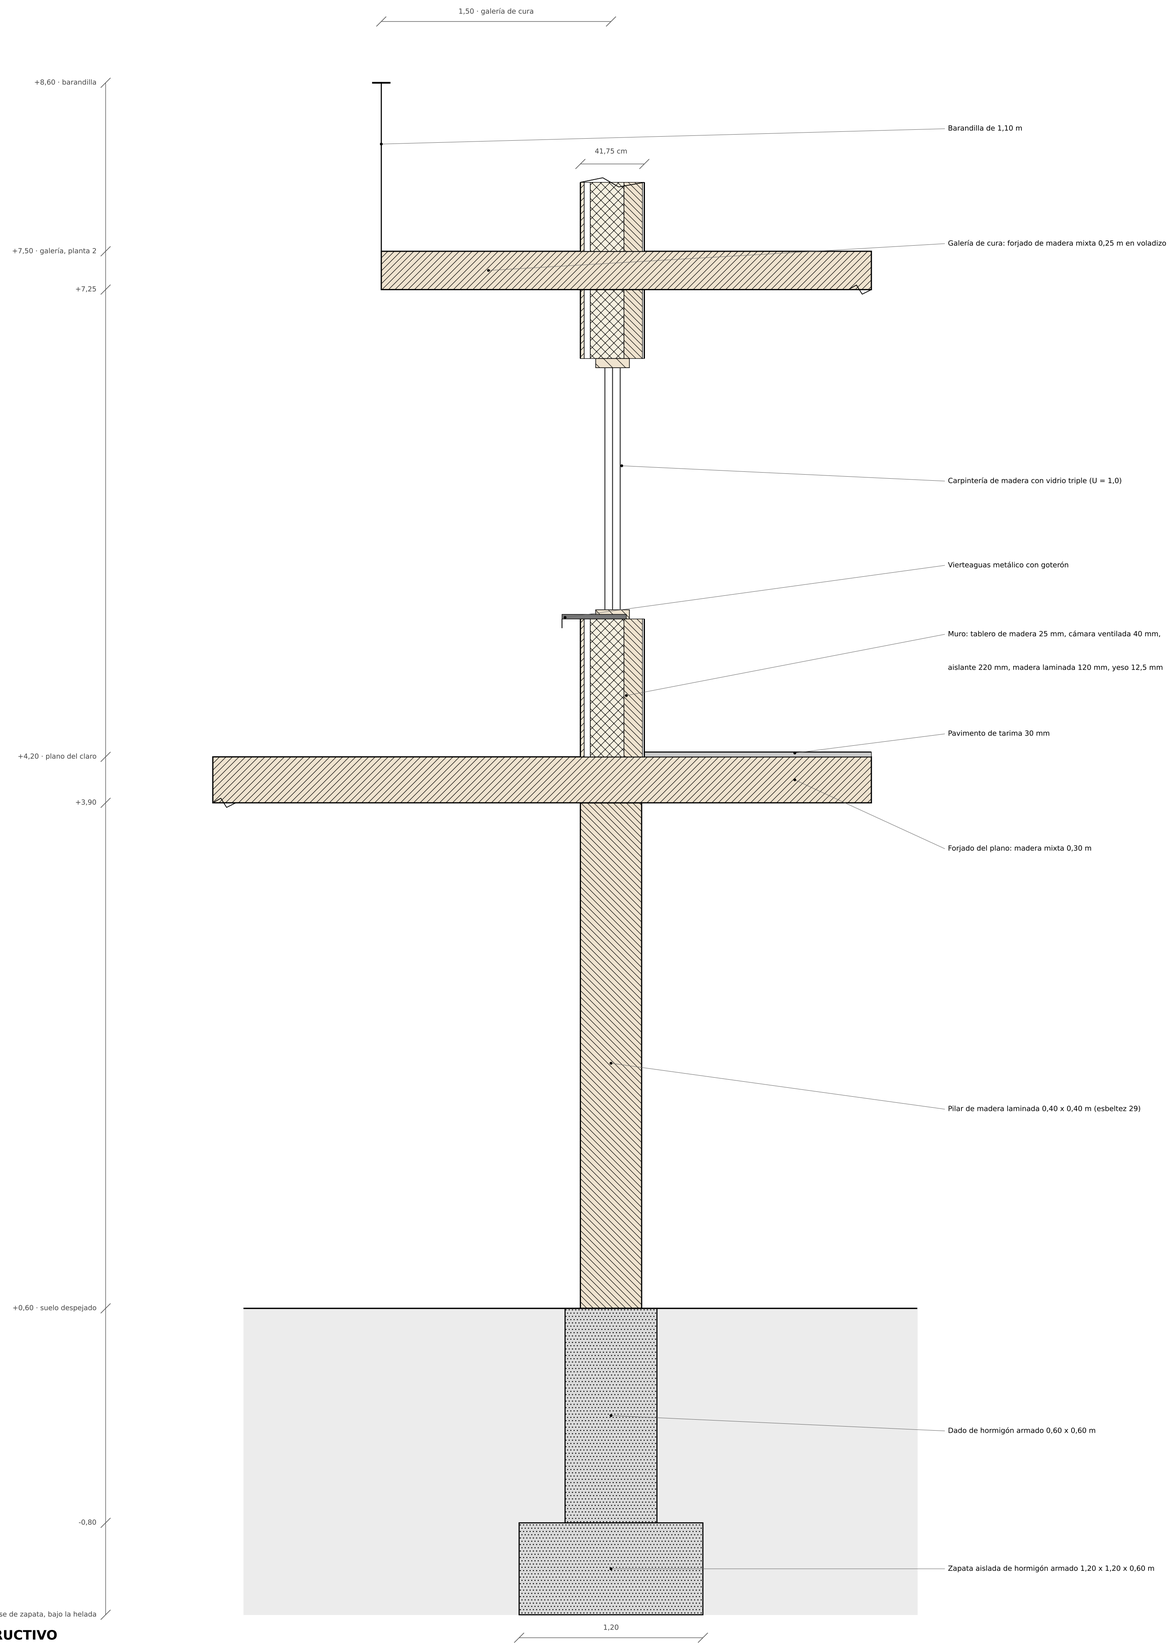

B · Planta 4: cubierta con vuelo

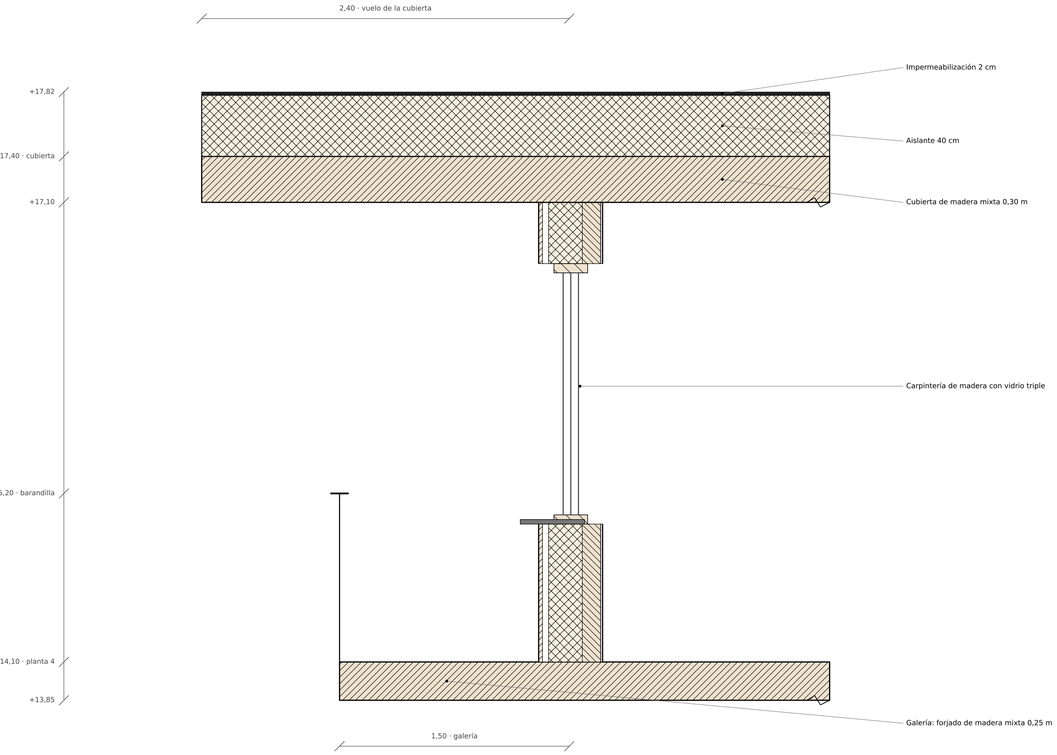

DETALLE CONSTRUCTIVO

E 1:20 · cotas absolutas del modelo · orientación: el exterior (sur) a la izquierda

0 1 2 m

CASO_021 · PROPUESTA B E 1:20

SECCIÓN CONSTRUCTIVA DE LA FACHADA SUR DE LAS BARRAS **D01**