ANTEPROYECTO
VIVIENDA SOCIAL
PROGRESIVA
CASO_001 - Propuesta B

SECCIÓN DE VIVIENDA TIPO
longitudinal 1:75

Detalle de la sección A-A
(vivienda A3) con cotas.

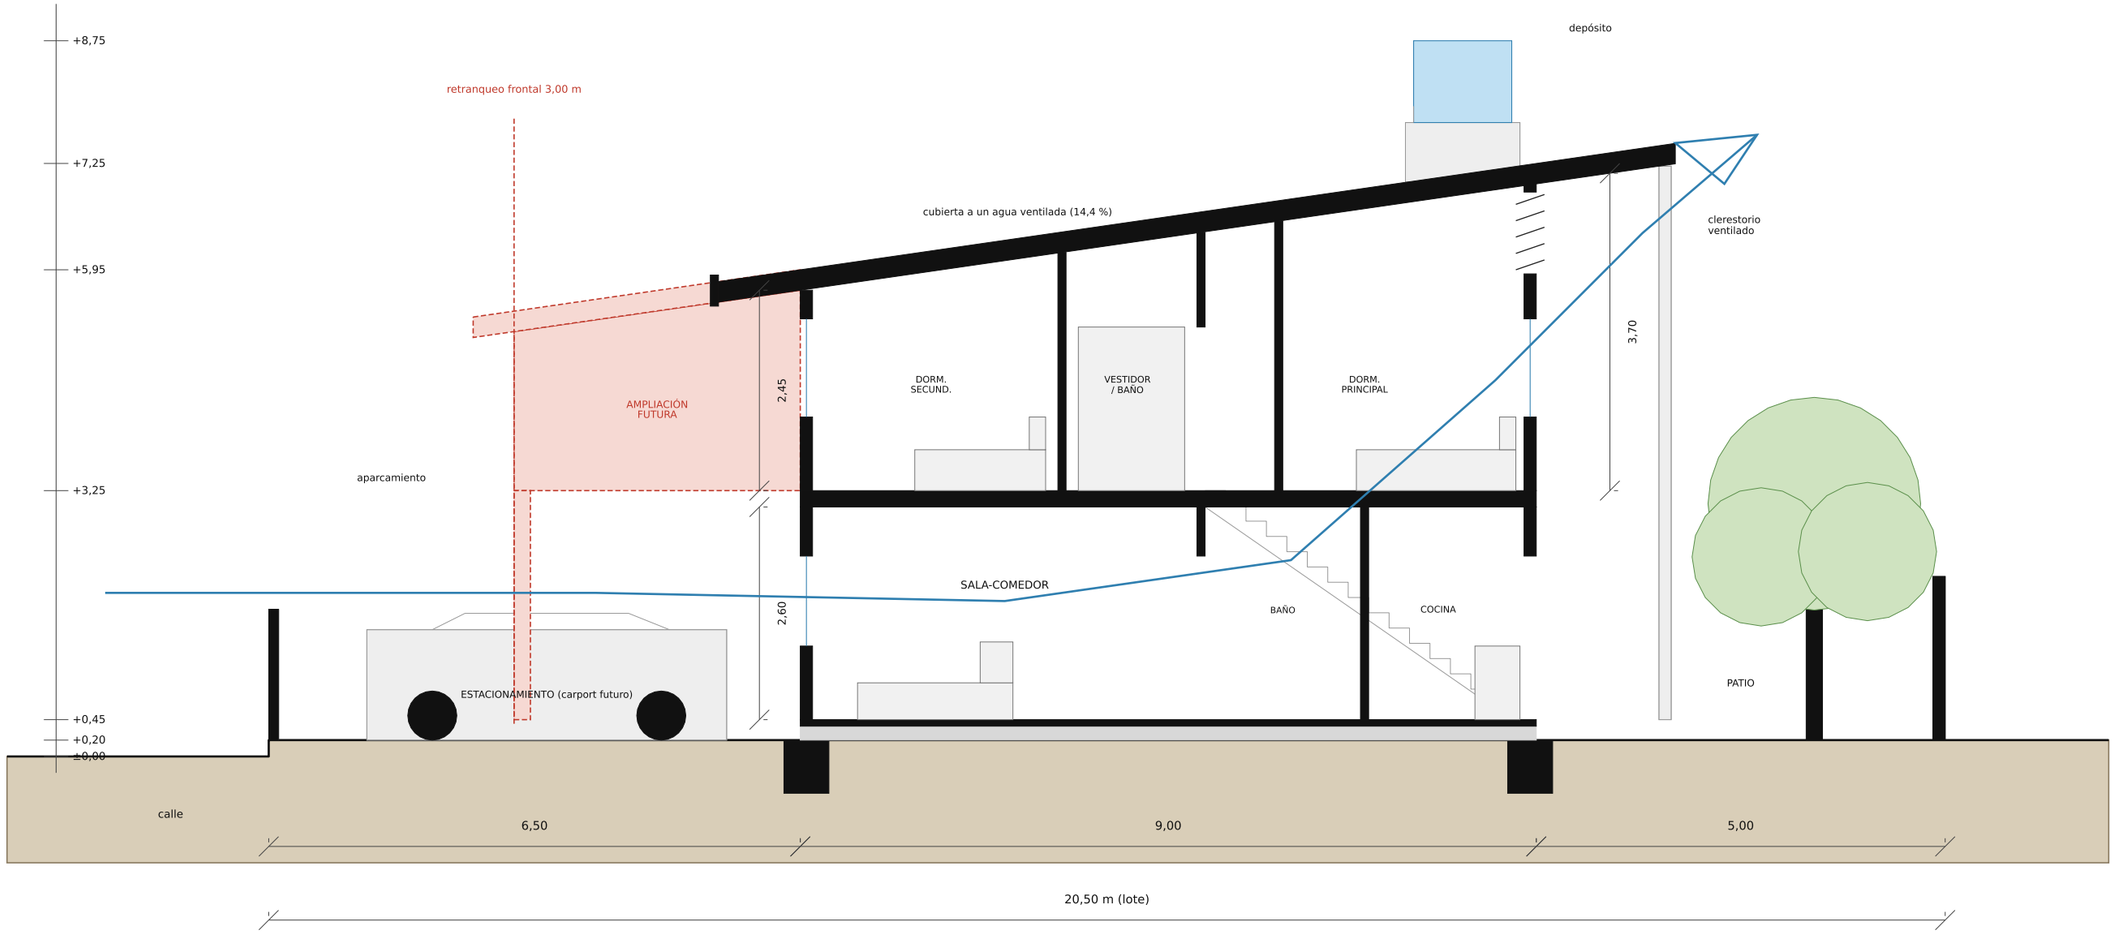

Escala 1:75
(formato 420x297 mm)