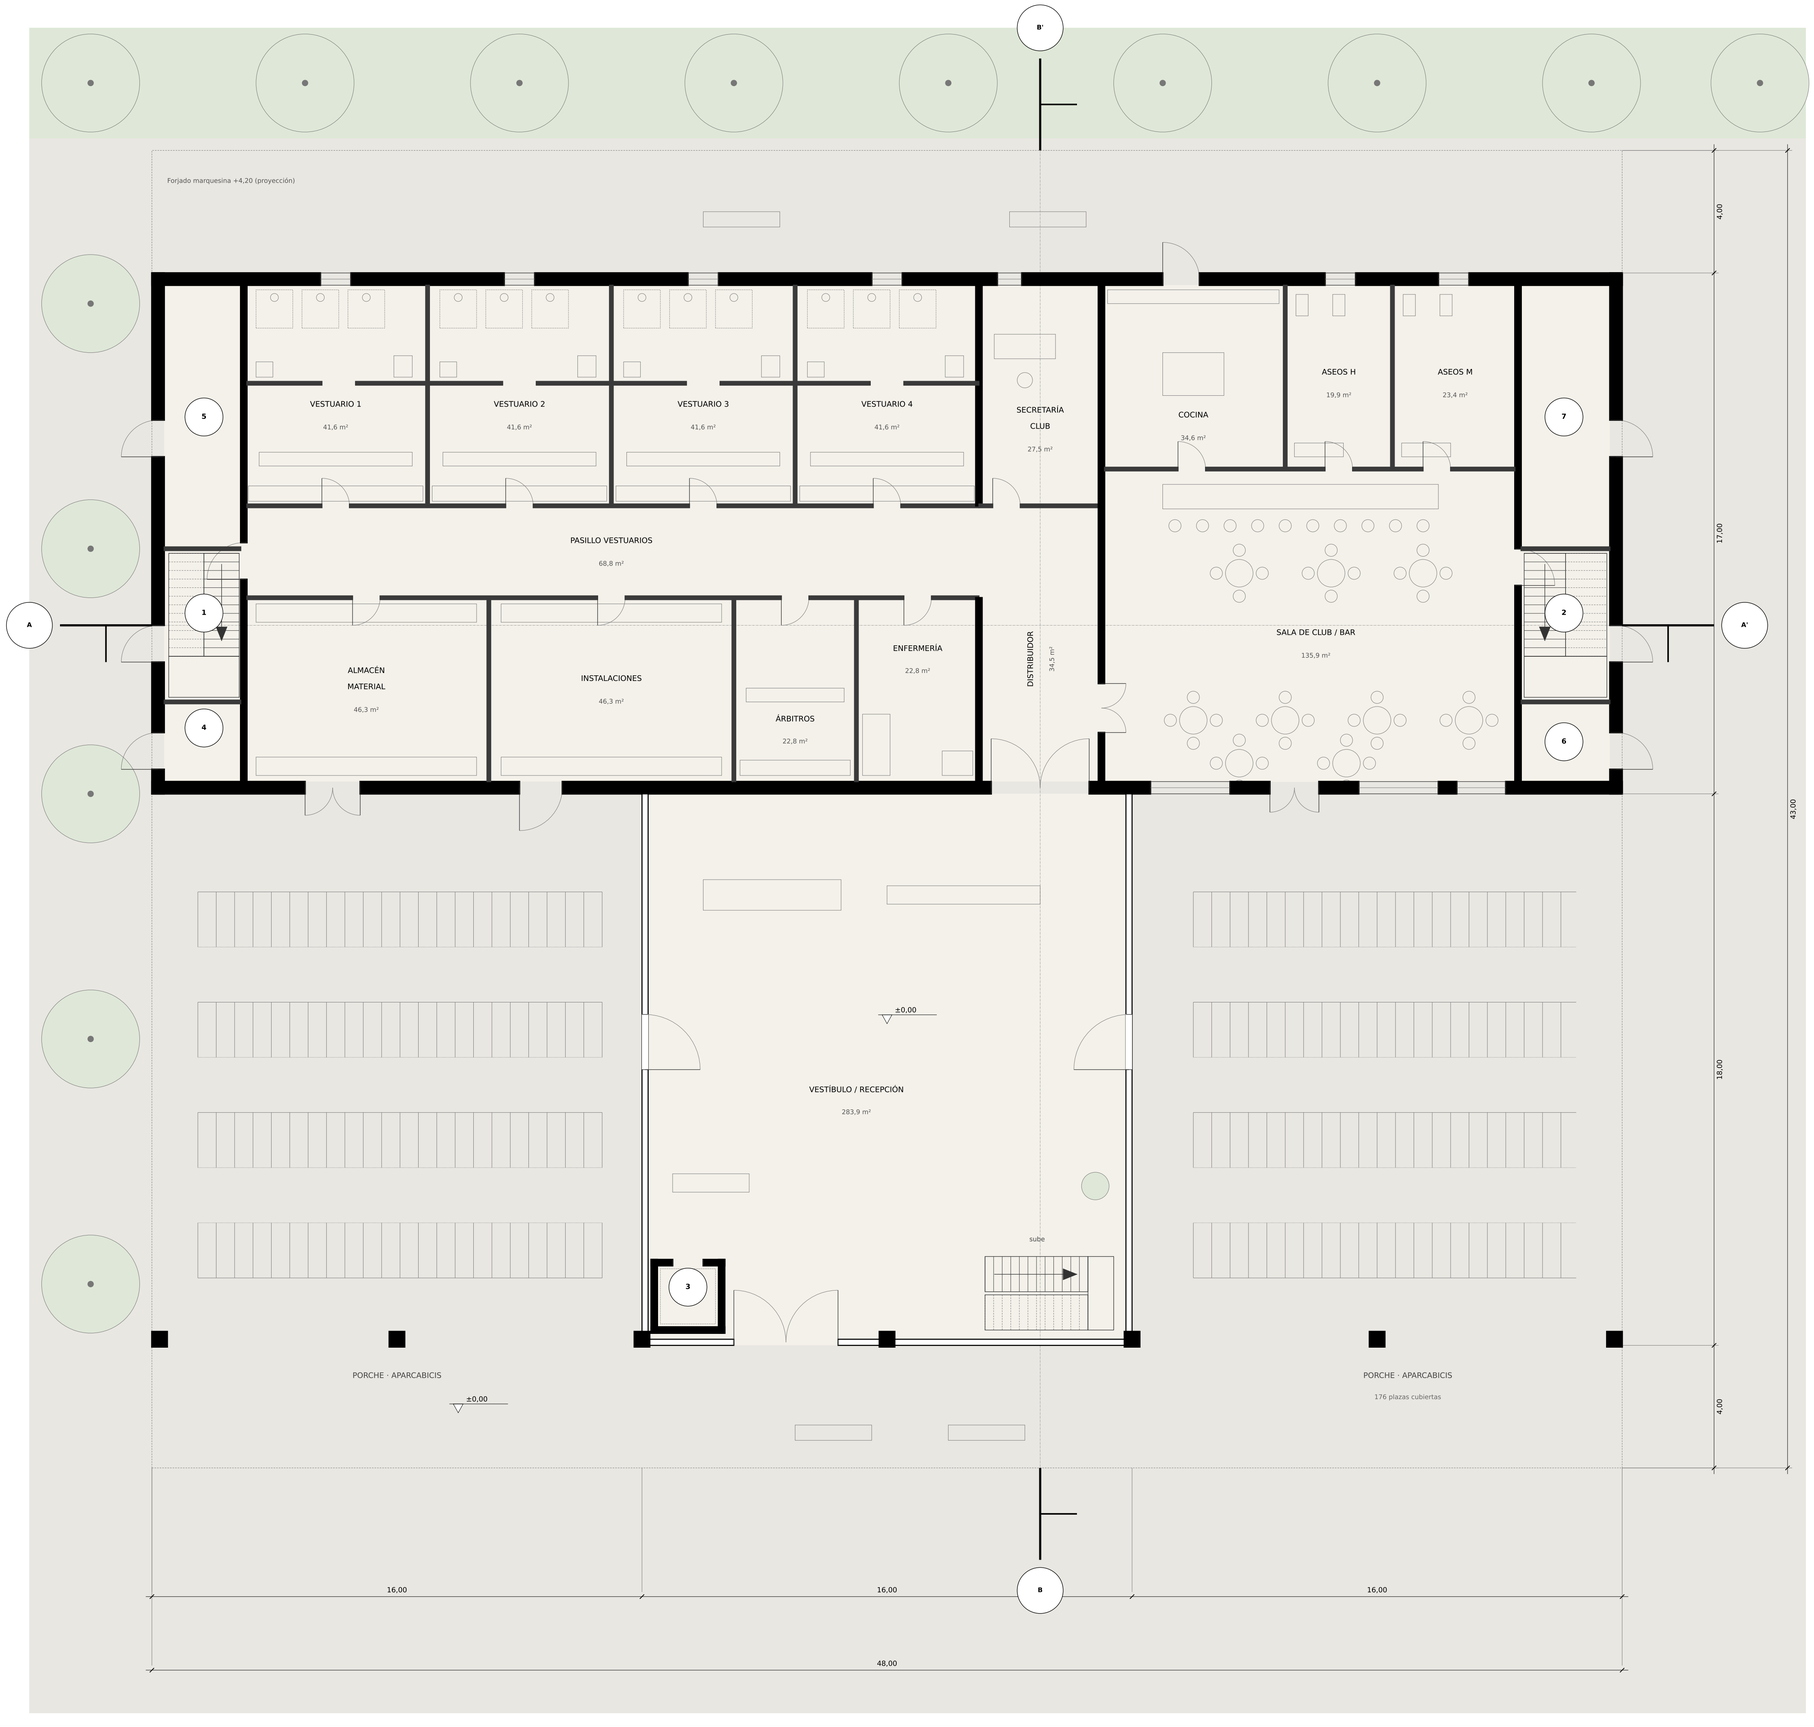


PLANTA BAJA

E 1:100

N

0 1 2 5 10 m

LEYENDA

PLANTA BAJA · uso del edificio (superficies útiles)

1	Escalera de jugadores	12,1 m²
2	Escalera este / evacuación	14,1 m²
3	Ascensor (PMR y montacargas)	4,3 m²
4	Limpieza	6,2 m²
5	Almacén exterior oeste	21,0 m²
6	Almacén de mobiliario	7,1 m²
7	Almacén exterior este	24,4 m²

Cuadro de superficies completo en memoria.md.

Norte asumido: camino de acceso en el lado sur.

CASO_002 · PROPUESTA A	Escala 1:100 (A1)
PLANTA BAJA · PORCHE Y SERVICIOS	ANTEPROYECTO
	Lámina P01