Cuadro de superficies útiles

Espacio de asamblea (38 plazas)	59,7 m²
Presbiterio (altar, ambón, sede, sagrario)	17,0 m²
Sacristía-almacén	3,3 m²
Aseo seco (compostable)	3,1 m²
Total útil interior	**83,1 m²**
Umbral cubierto (exterior, no computa)	3,3 m²
Superficie construida cerrada (muros incl.)	**103,8 m²**

Leyenda

1 Altar (mesa de piedra reutilizada)

2 Ambón

3 Sede

4 Sagrario (hornacina) y cruz en el muro oeste

5 Bancos de madera reciclada (0,45 m)

6 Letrina seca compostable

7 Armario de sacristía

Línea discontinua: cubierta (por encima del corte)

Plano de corte horizontal a +1,20 m

N

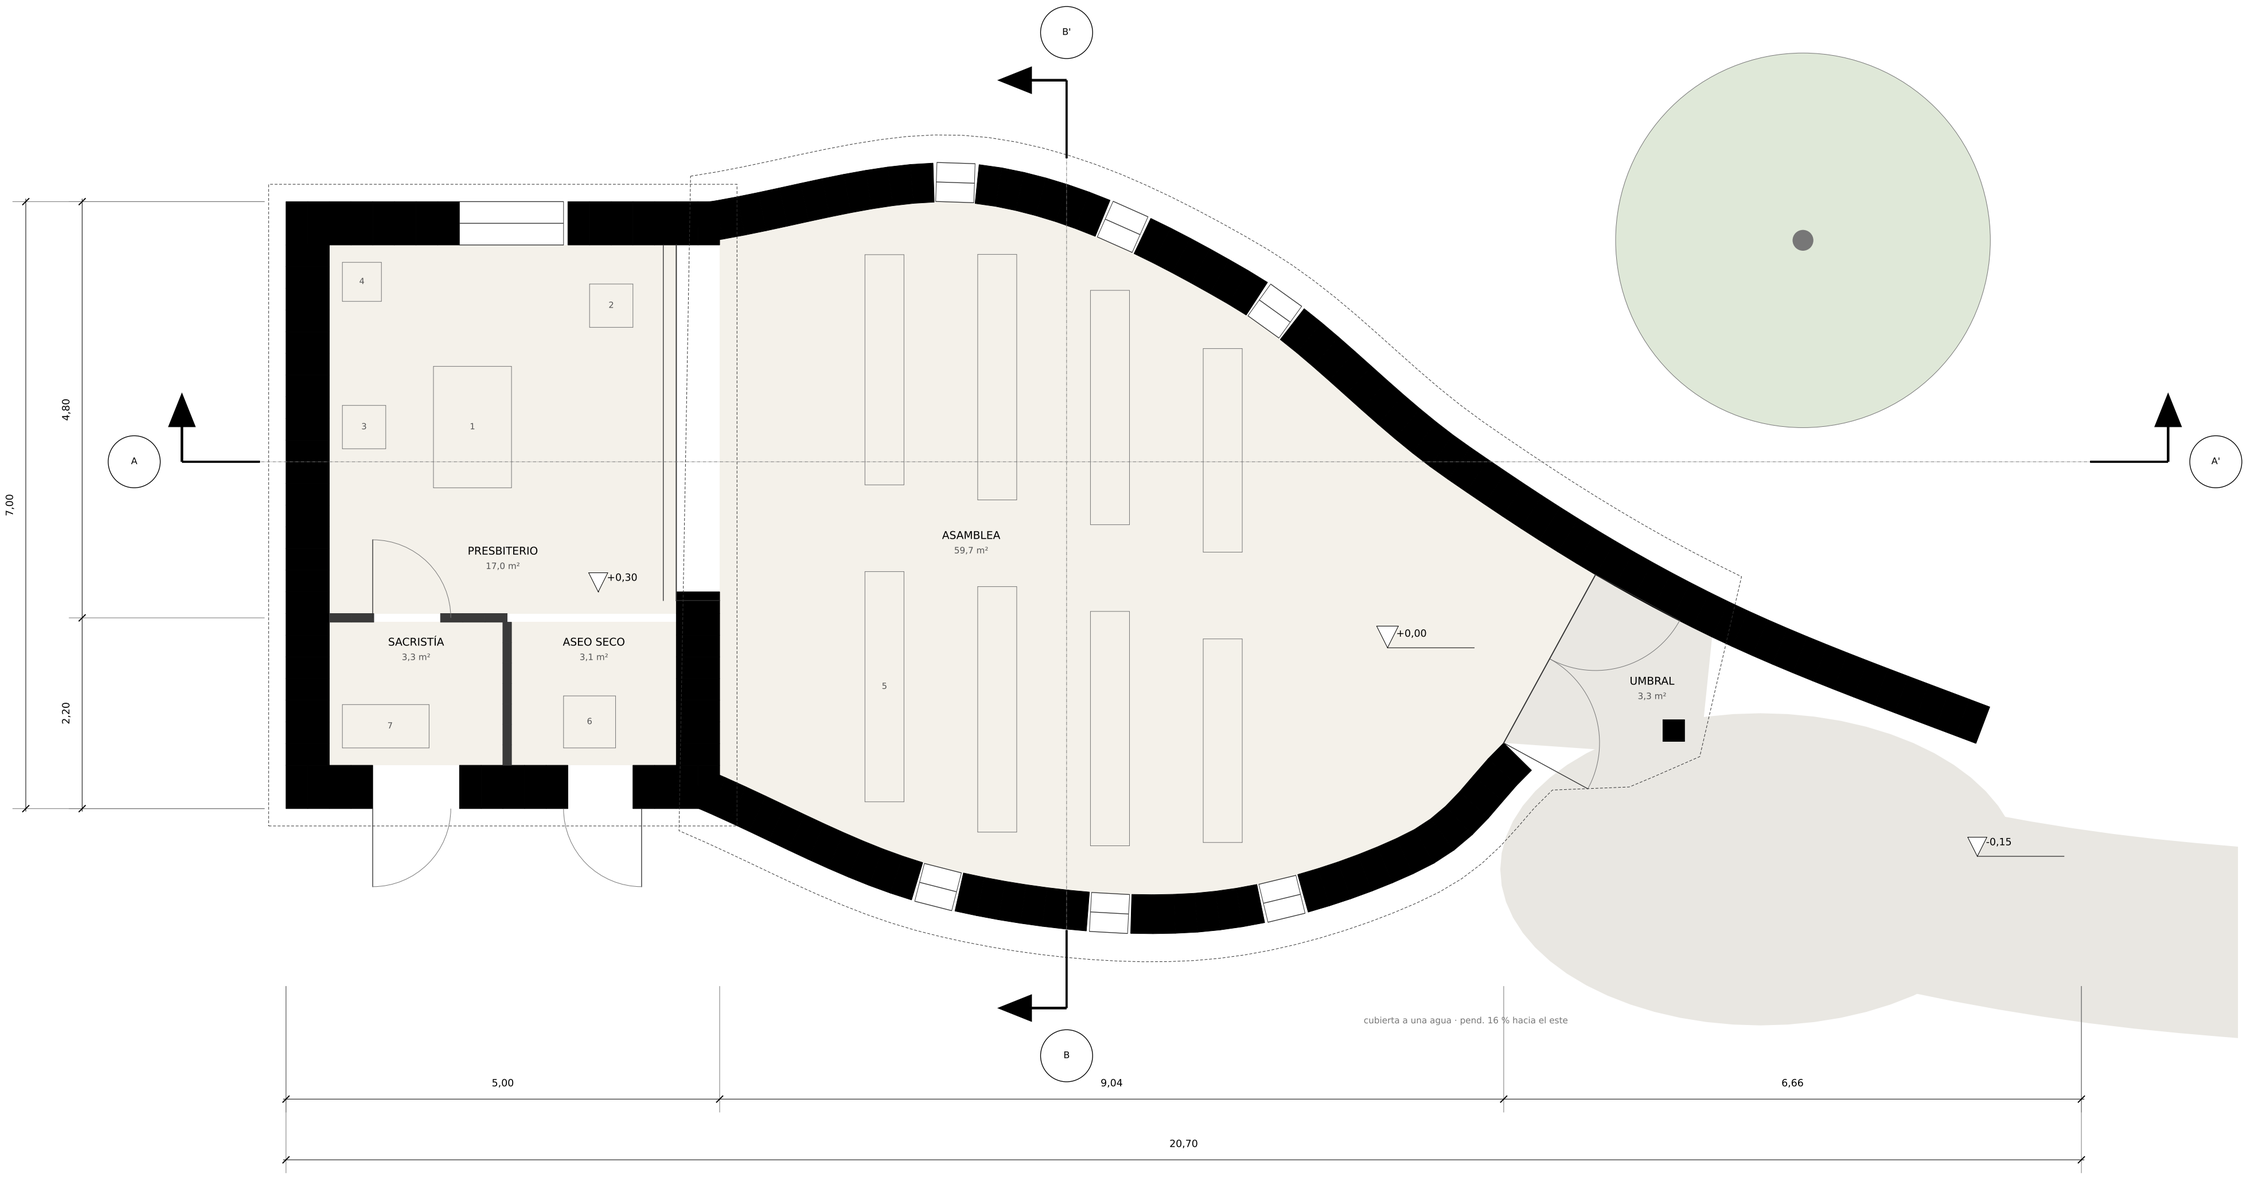

PLANTA BAJA

E 1:50

0 1 2 5 10 m

CASO_003 · PROPUESTA A	Anteproyecto	
Planta baja	Escala 1:50	**P01**