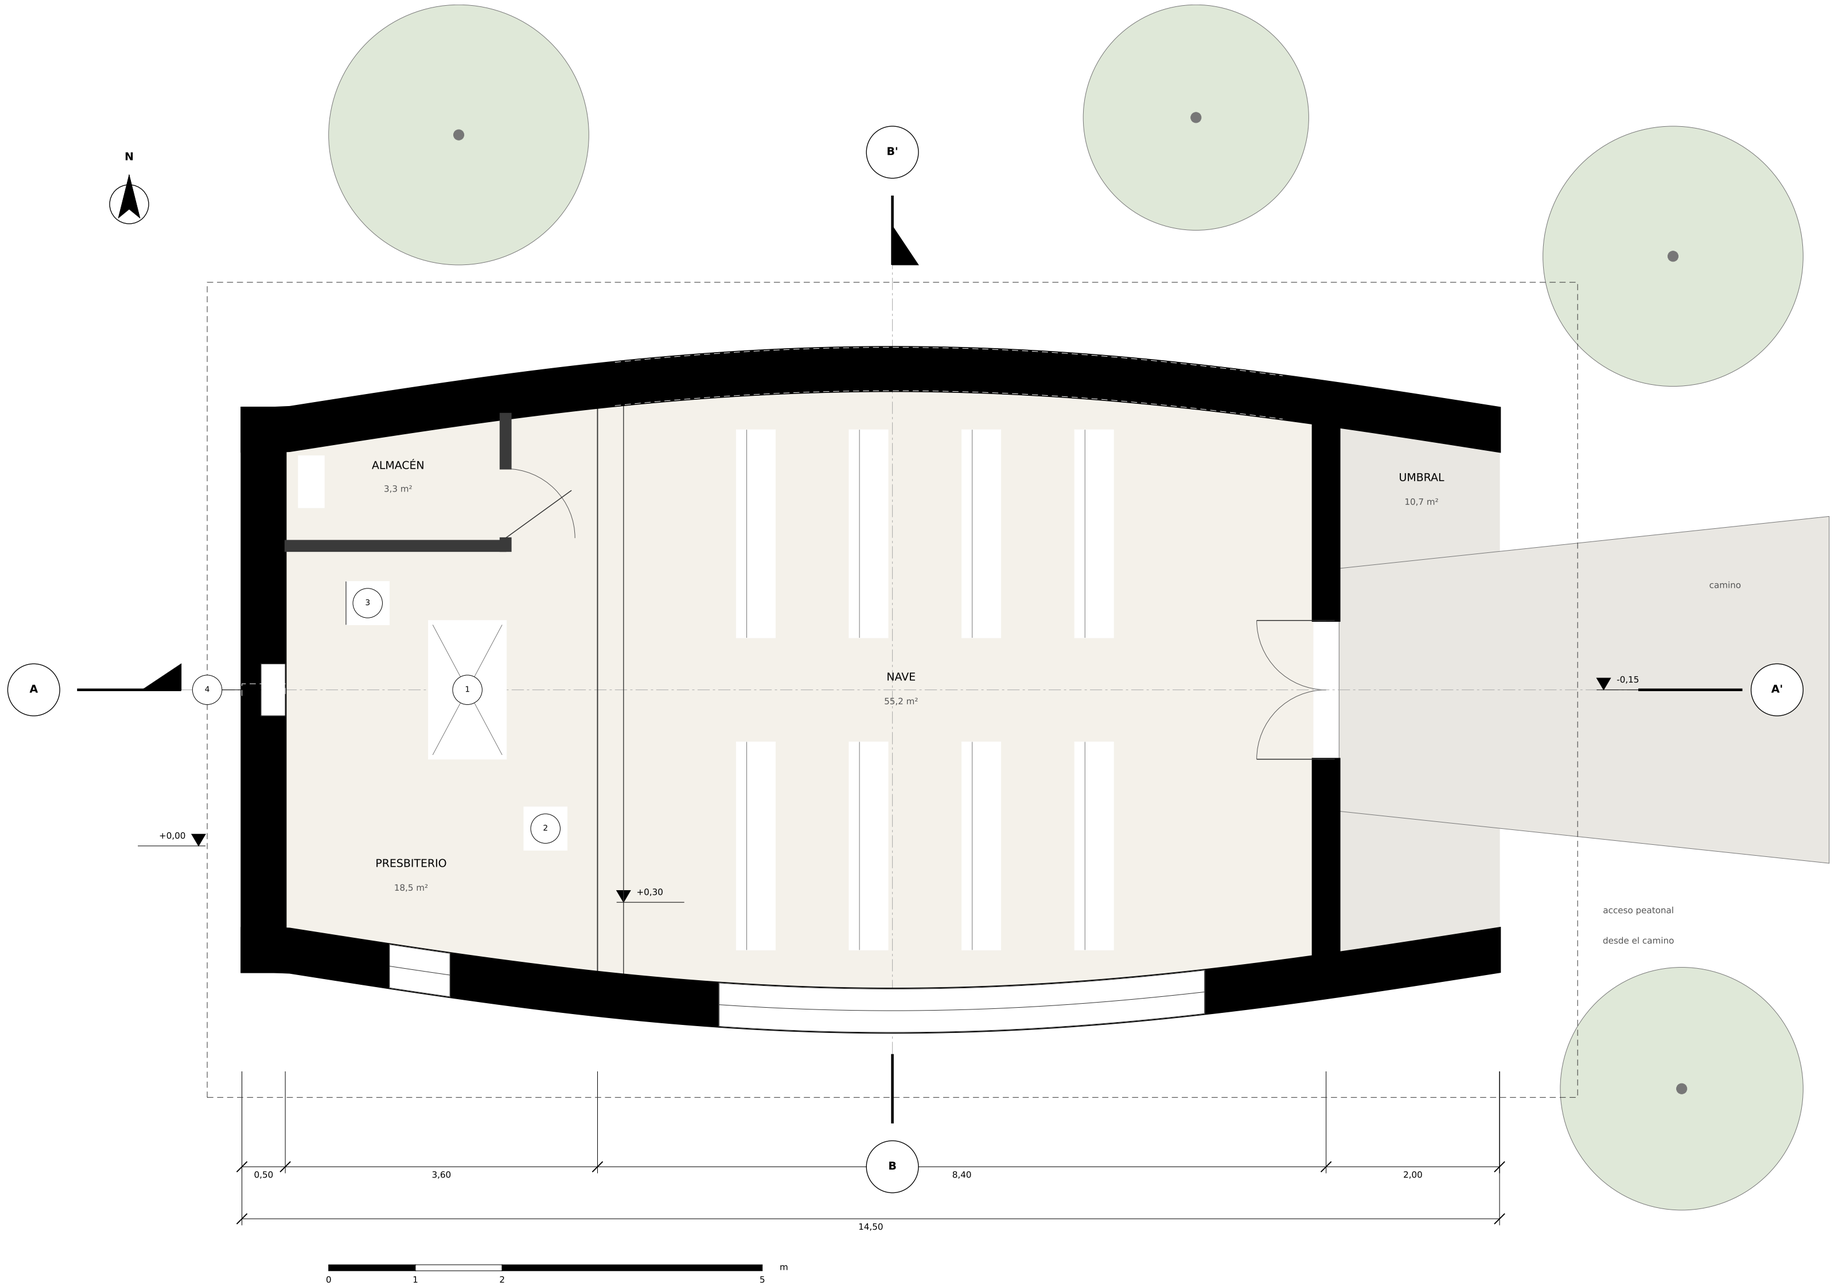

LEYENDA

1 Altar (bloque de piedra reutilizada)

2 Ambón

3 Sede

4 Sagrario (nicho) y cruz de luz en el muro oeste (hueco superior discontinuo)

CUADRO DE SUPERFICIES ÚTILES

Nave (asamblea, 32 plazas)	55,2 m²
Presbiterio (con sagrario)	18,5 m²
Almacén-sacristía	3,3 m²
Umbral cubierto	10,7 m²
Superficie útil total	**87,6 m²**
Superficie construida (huella con muros)	106,8 m²

Cotas de nivel respecto al suelo de la nave (+0,00).

Terreno exterior -0,15. Plataforma presbiterio +0,30.

Corte de planta a +1,20 m.

PLANTA BAJA

E 1:50

CASO_003 · PROPUESTA C	**Planta baja**	
Anteproyecto	Escala 1:50	**Lámina P01**