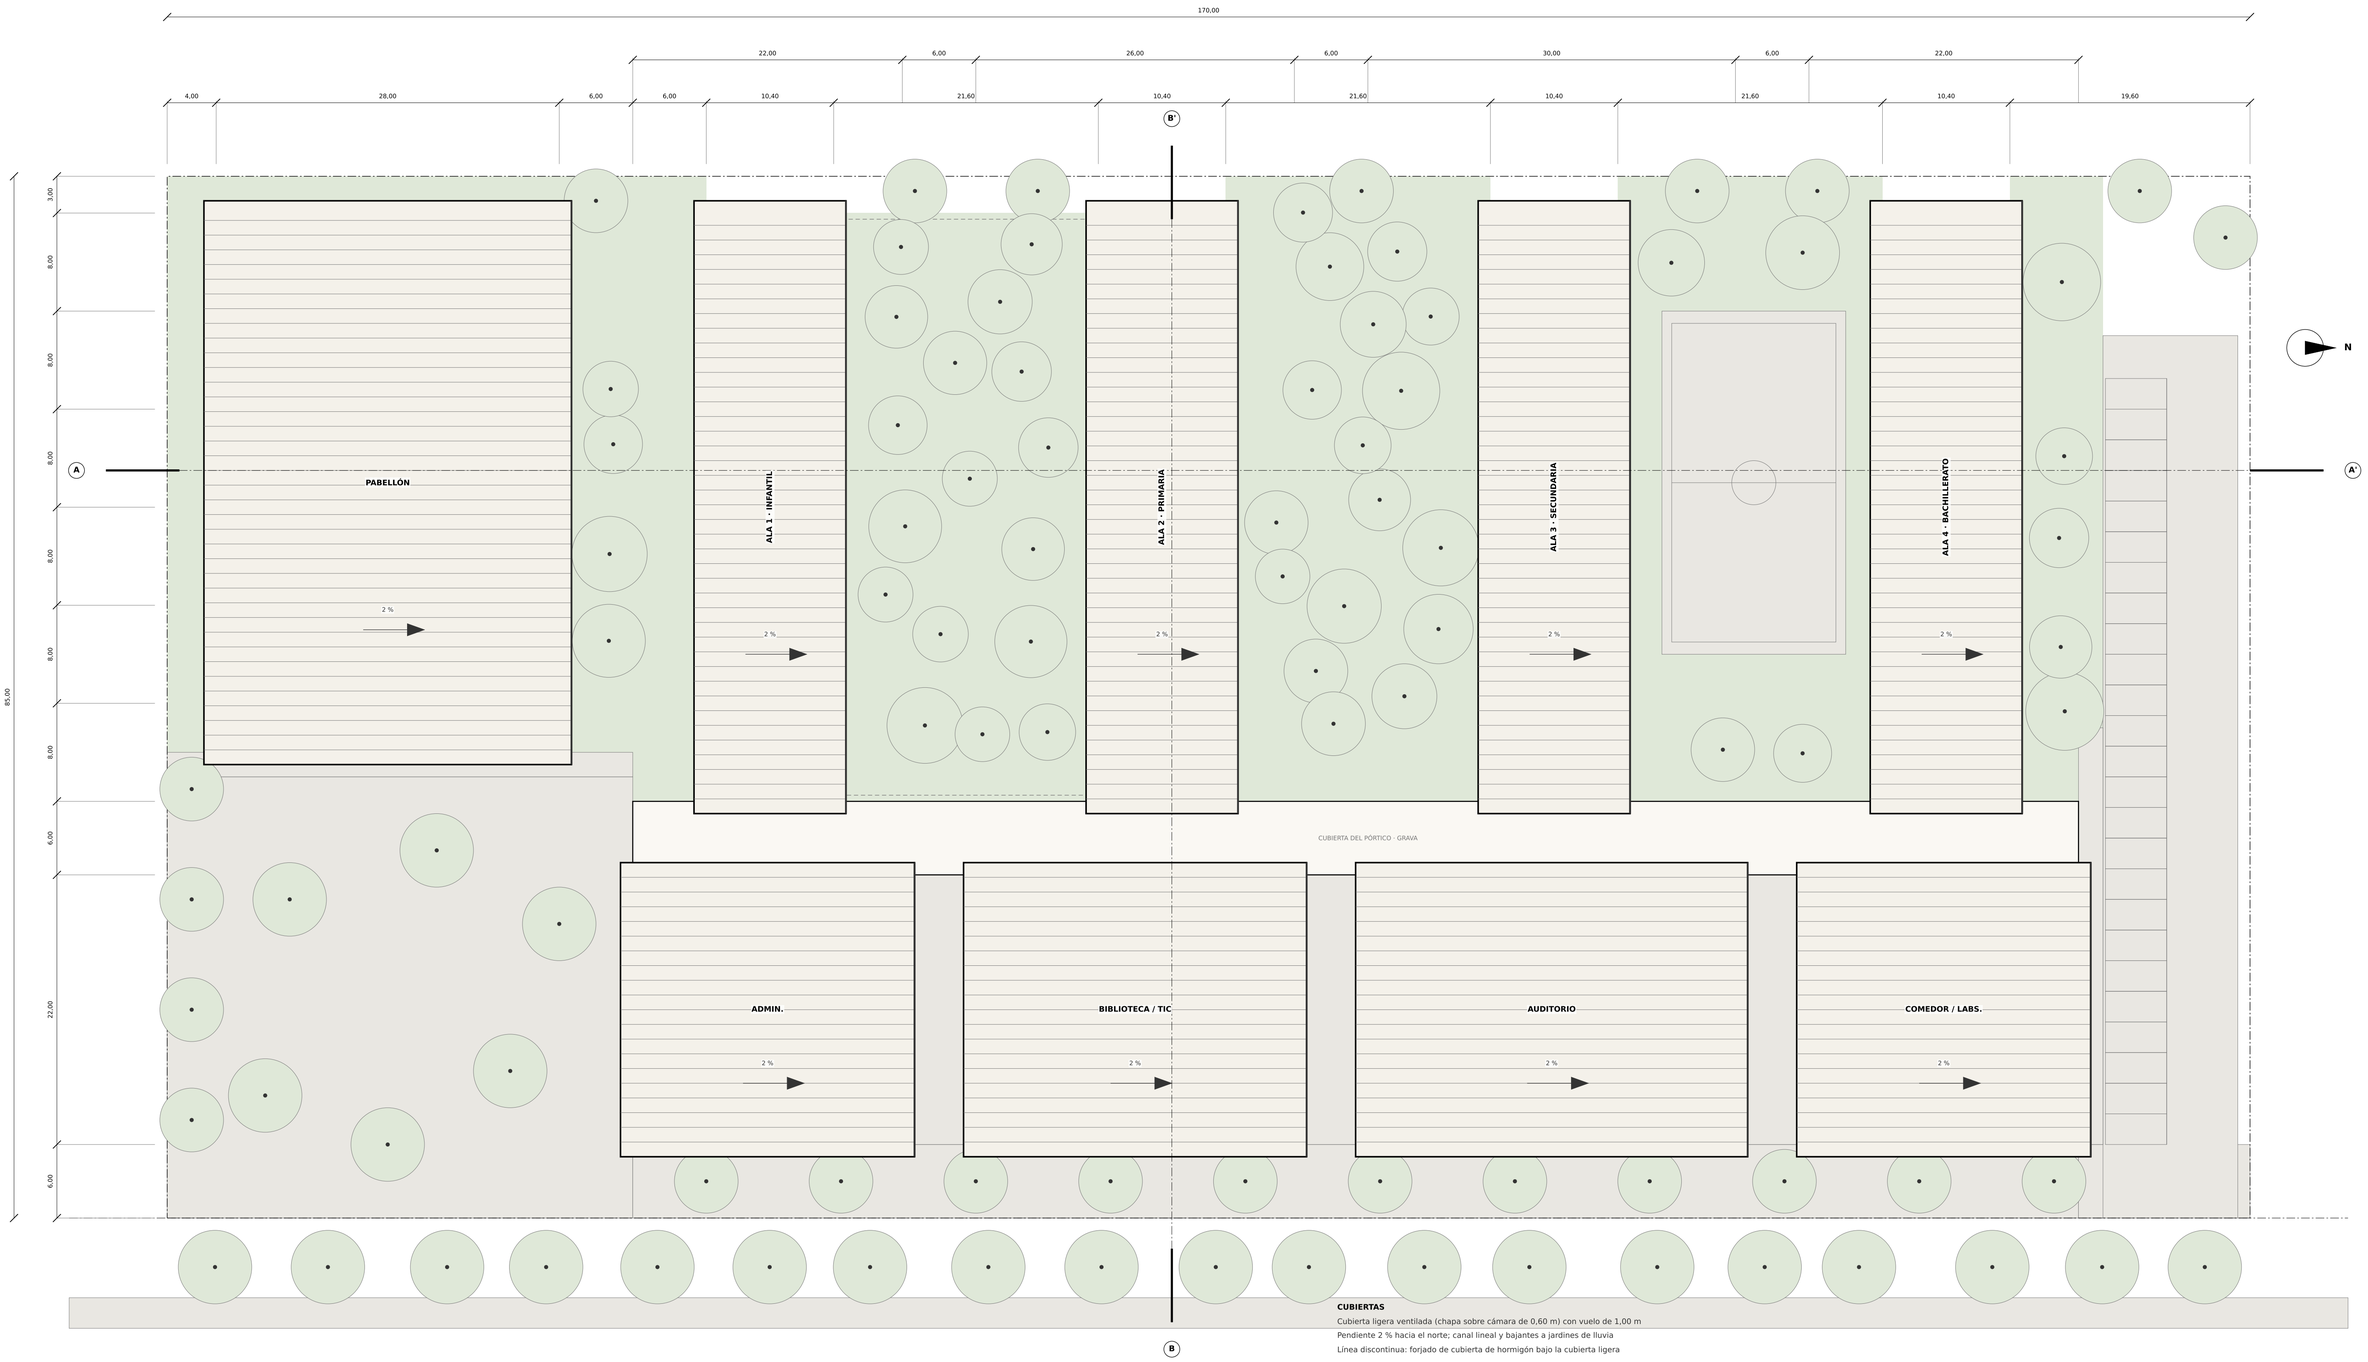


CUBIERTAS

Cubierta ligera ventilada (chapa sobre cámara de 0,60 m) con vuelo de 1,00 m

Pendiente 2 % hacia el norte; canal lineal y bajantes a jardines de lluvia

Línea discontinua: forjado de cubierta de hormigón bajo la cubierta ligera

PLANTA DE CUBIERTAS

E 1:250

0 1 2 5 10 m

CASO_004 · PROPUESTA A	Centro educativo · anteproyecto
	Lámina **P03**
Planta de cubiertas · conjunto	Escala **1:250**
	Anteproyecto A