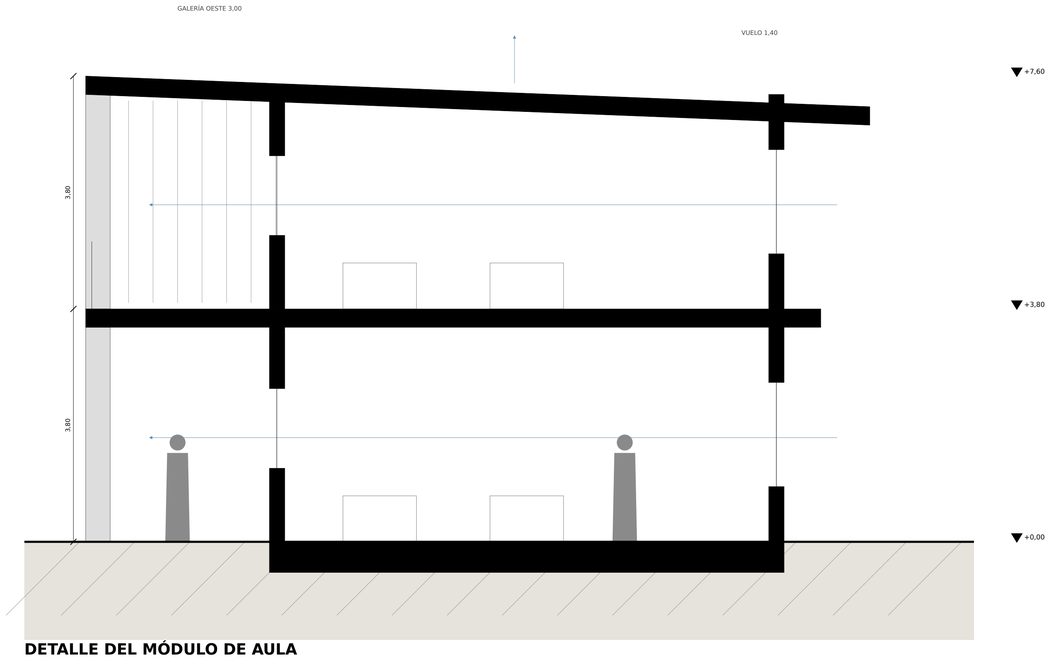

DETALLE DEL MÓDULO DE AULA

E 1:50

SISTEMA CONSTRUCTIVO DEL MÓDULO

Pórticos de hormigón armado cada 7,50 m con muros de carga transversales de 25 cm.

Forjado losa maciza 30 cm, solera sobre encachado en seco (sin sótano).

Cerramiento de bloque cerámico visto / ladrillo local, sin carpintería al sol directo.

Cubierta ligera ventilada con pendiente 4 % al este, vuelo de 1,40 m y placas FV.

Galería oeste 3,00 m con lamas verticales de madera frente a la radiación de tarde.

Ventana alta oeste + ventana larga este: ventilación cruzada; extracción en cumbrera.

Cota de nivel referida al acceso (+0,00).

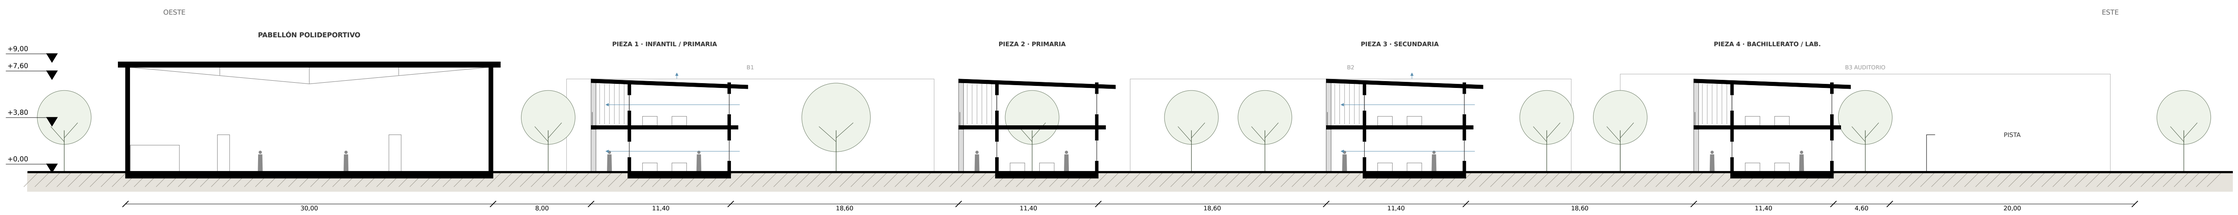

Terreno natural asumido con pendiente < 1 % (plataforma única a +0.00).

SECCIÓN LONGITUDINAL A-A'

E 1:250

0 1 2 5 10 m

CASO_004 · PROPUESTA B	ESCALA **1:250**	LÁMINA **S01**
Sección longitudinal A-A'	Anteproyecto	