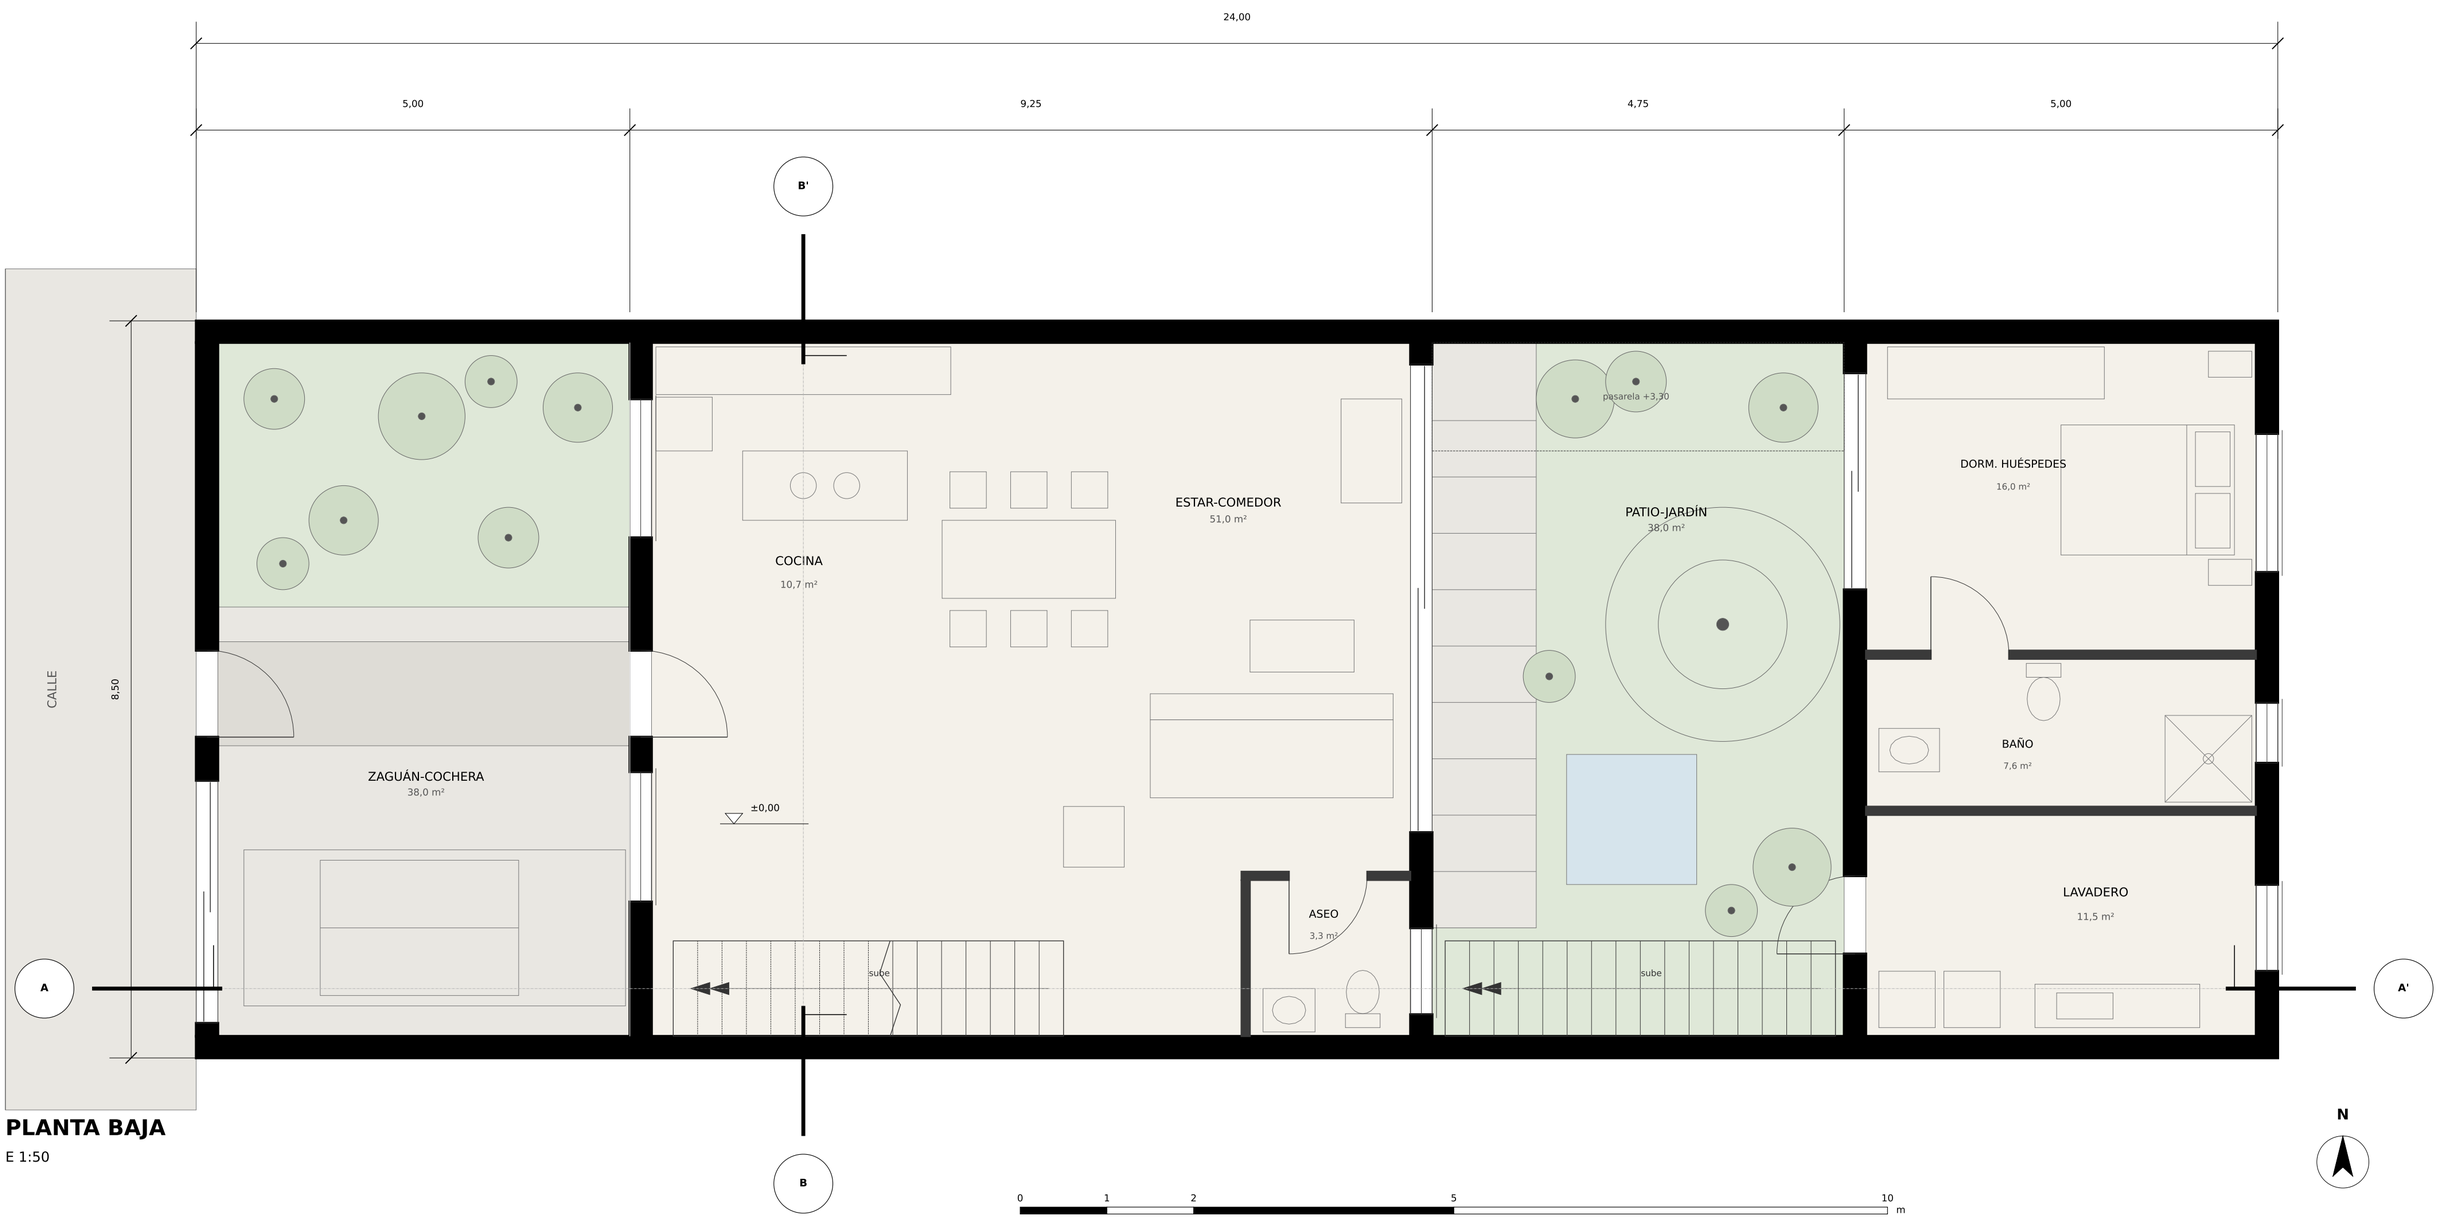

PLANTA BAJA

E 1:50

CUADRO DE SUPERFICIES ÚTILES

Zaguán-jardín / cochera (semicubierto)	38,0 m²
Estar-comedor	51,0 m²
Cocina (abierta)	10,7 m²
Escalera 1	5,0 m²
Aseo	3,3 m²
Lavadero-cuarto técnico	11,5 m²
Baño de huéspedes	7,6 m²
Dormitorio de huéspedes	16,0 m²
Patio-jardín (descubierto)	38,0 m²
Útil cerrado de la planta	**105,1 m²**

NOTAS

Cotas en metros. ±0,00 = cota del solar (plano). Altura libre interior 3,00 m; forjados de 0,30 m.

Muros de carga de fábrica armada/hormigón de 0,25 m (negro). Tabiques de 0,10 m (gris oscuro).

Orientación: calle al oeste-suroeste (aquí, oeste); medianeras al norte y al sur.

Cortes A–A' (longitudinal, mirando al norte) y B–B' (transversal, mirando al este).

Planta alta volada sobre el zaguán (cota +3,30): zaguán semicubierto.

Escalera 1 (interior) y escalera 2 (patio) rematan en forjado +3,30.

CASO_006 · PROPUESTA A

Planta baja

Anteproyecto	Escala 1:50	**Lámina P01**