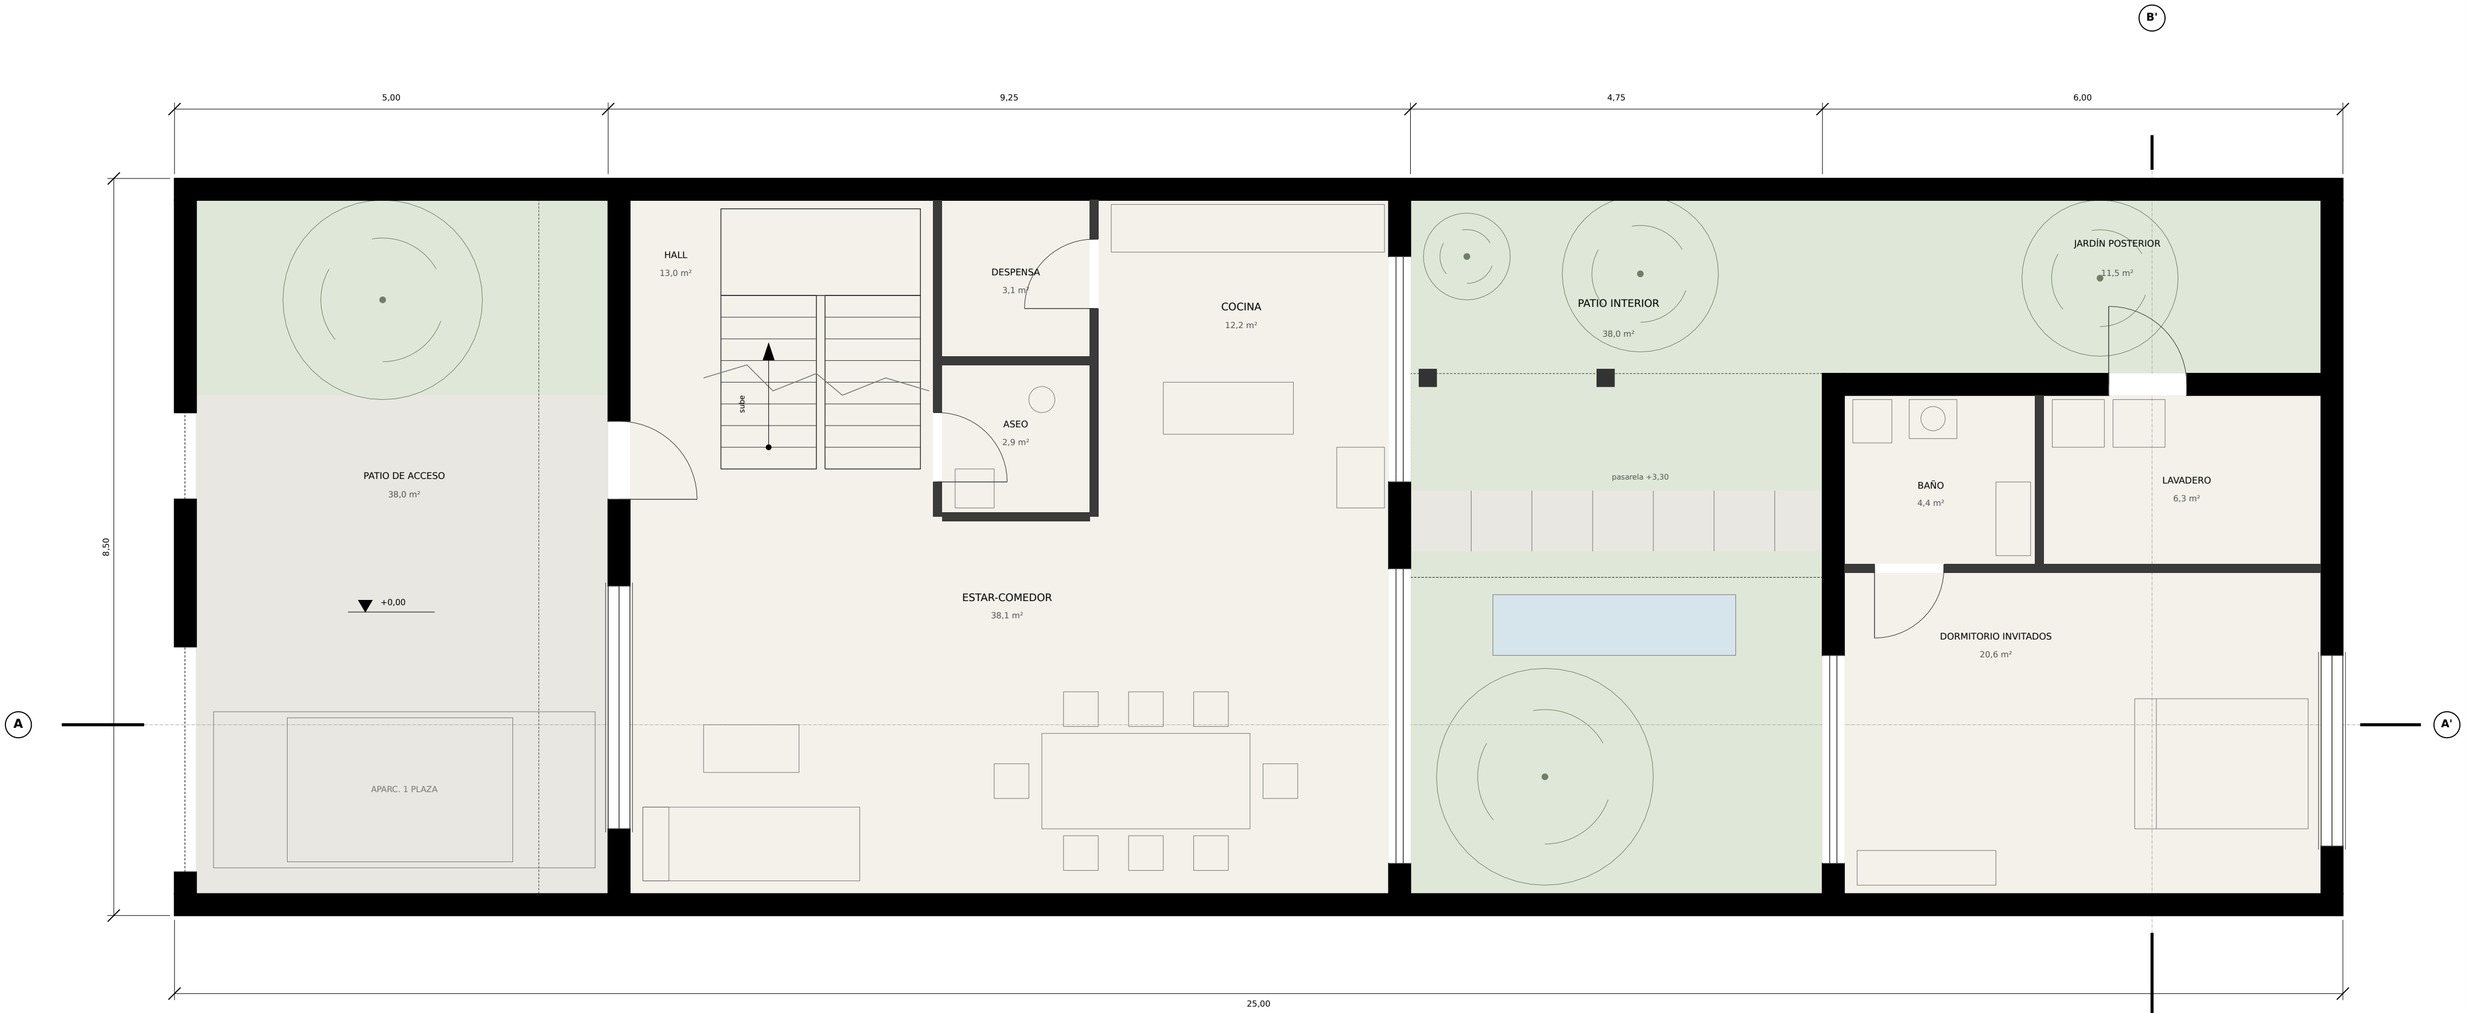

PLANTA BAJA

E 1:50

0 1 2 5 10 m

N

CUADRO DE SUPERFICIES ÚTILES

ESTAR-COMEDOR	38,1 m²
HALL Y ESCALERA	13,0 m²
ASEO	2,9 m²
DESPENSA	3,1 m²
COCINA	12,2 m²
DORMITORIO INVITADOS	20,6 m²
BAÑO INVITADOS	4,4 m²
LAVADERO	6,3 m²
TOTAL ÚTIL DEL NIVEL	**100,5 m²**
Superficie construida bruta del nivel	116,1 m²

LEYENDA

- Muro portante cortado
- Tabique cortado
- Vegetación / patio / cubierta vegetal
- Pavimento exterior
- Lámina de agua
- Interior
- Elemento por encima del plano de corte

Hipótesis: altura máx. 9,60 m; muros de 25 cm; tabiques de 10 cm.
Norte aprox. (±15°): fachada a calle al oeste-suroeste.

CASO_006 · PROPUESTA B	ESCALA	LÁMINA
PLANTA BAJA	**1:50**	**P01** Anteproyecto