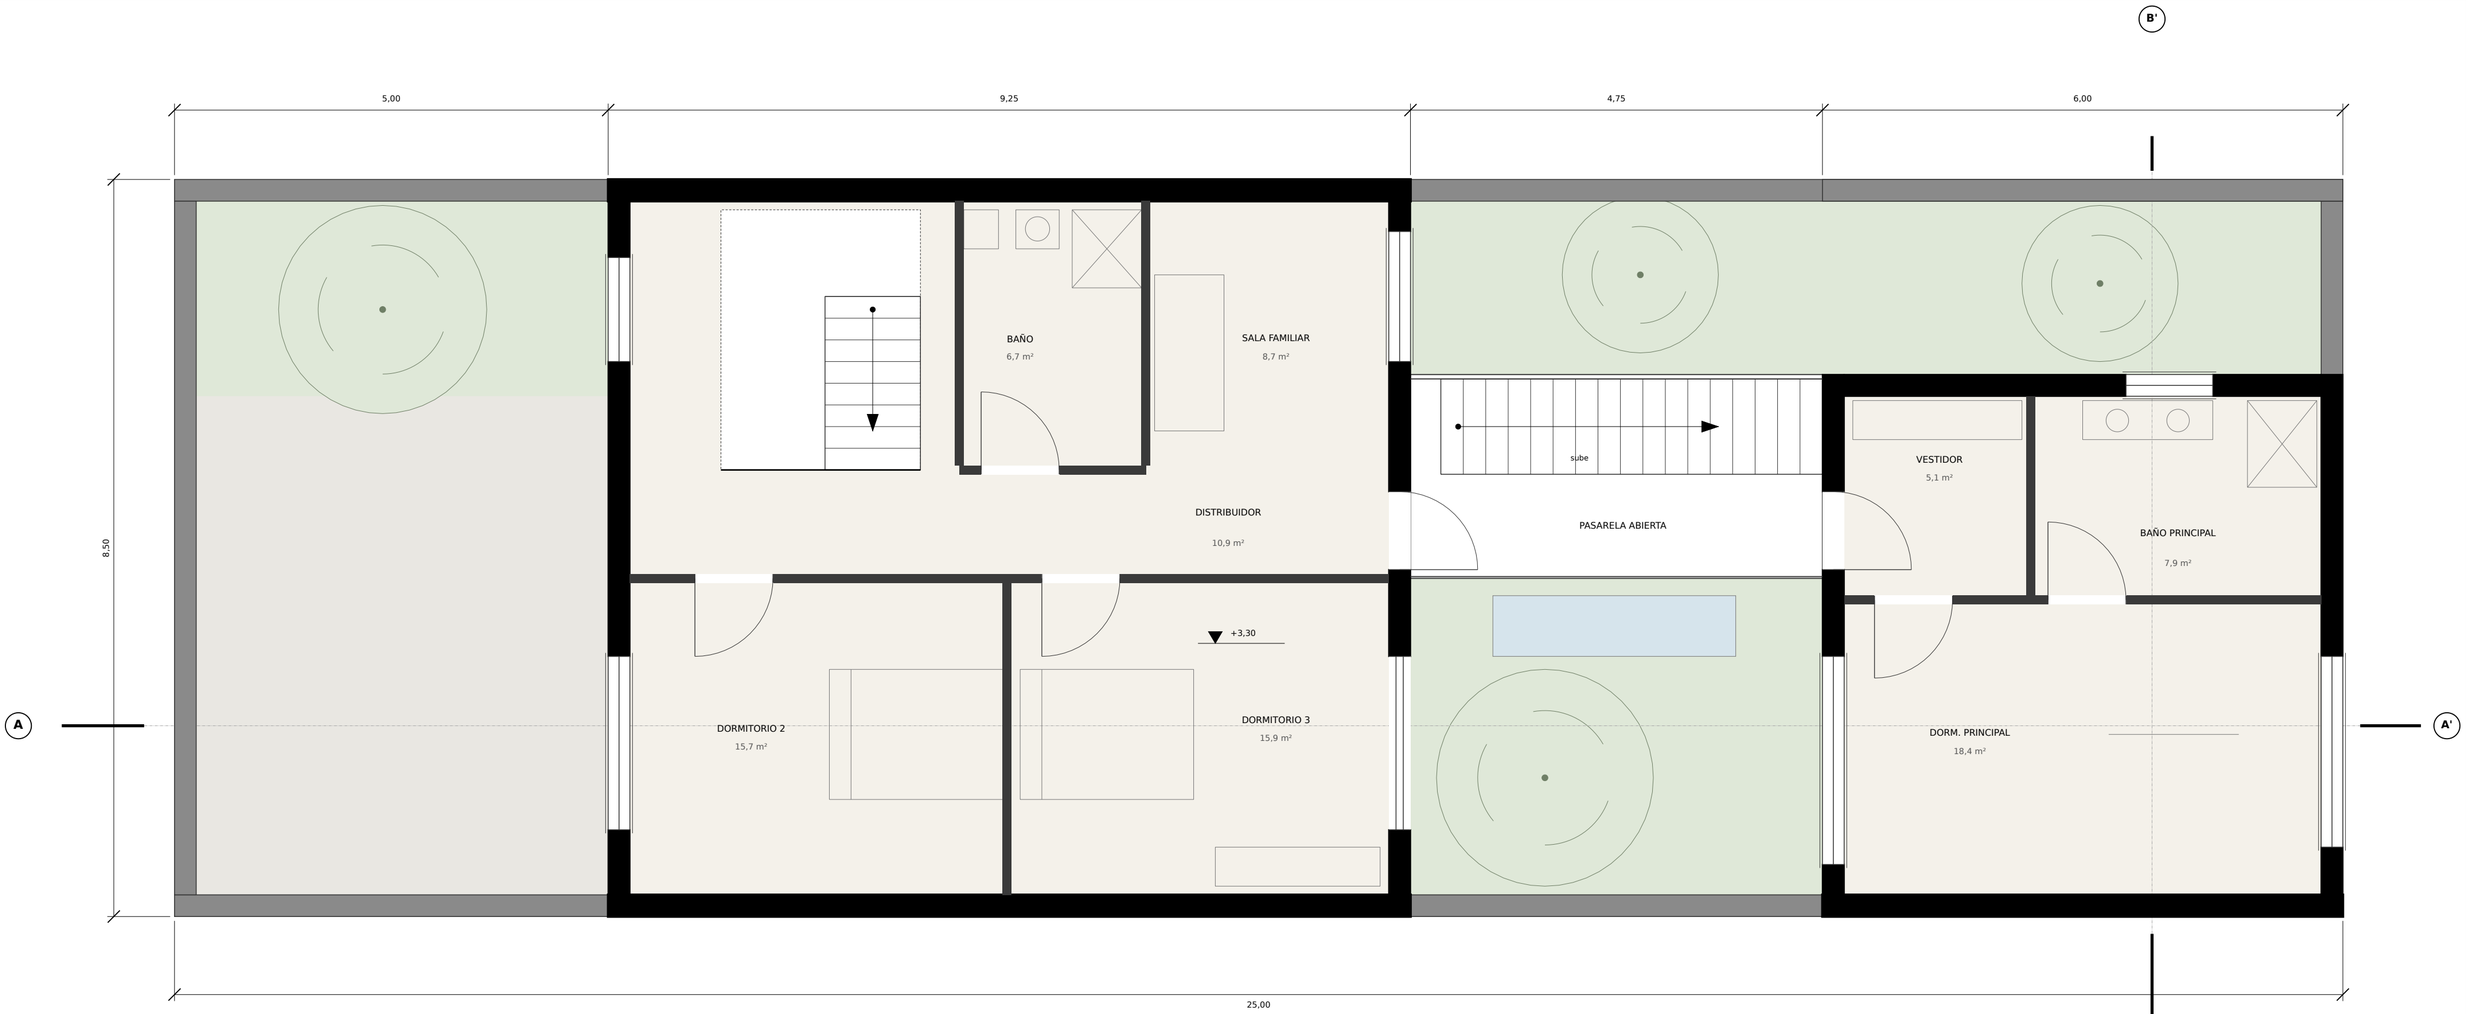

PLANTA PRIMERA

E 1:50

0 1 2 5 10 m

N

CUADRO DE SUPERFICIES ÚTILES

DORMITORIO 2	15,7 m²
DORMITORIO 3	15,9 m²
DISTRIBUIDOR	10,9 m²
BAÑO COMÚN	6,7 m²
SALA FAMILIAR	8,7 m²
DORMITORIO PRINCIPAL	18,4 m²
VESTIDOR	5,1 m²
BAÑO PRINCIPAL	7,9 m²
TOTAL ÚTIL DEL NIVEL	**89,2 m²**
Superficie construida bruta del nivel	127,3 m²

LEYENDA

- Muro portante cortado
- Tabique cortado
- Vegetación / patio / cubierta vegetal
- Pavimento exterior
- Lámina de agua
- Interior
- Elemento por encima del plano de corte

Hipótesis: altura máx. 9,60 m; muros de 25 cm; tabiques de 10 cm.
Norte aprox. (±15°): fachada a calle al oeste-suroeste.

CASO_006 · PROPUESTA B	ESCALA	LÁMINA
PLANTA PRIMERA	**1:50**	**P02** Anteproyecto