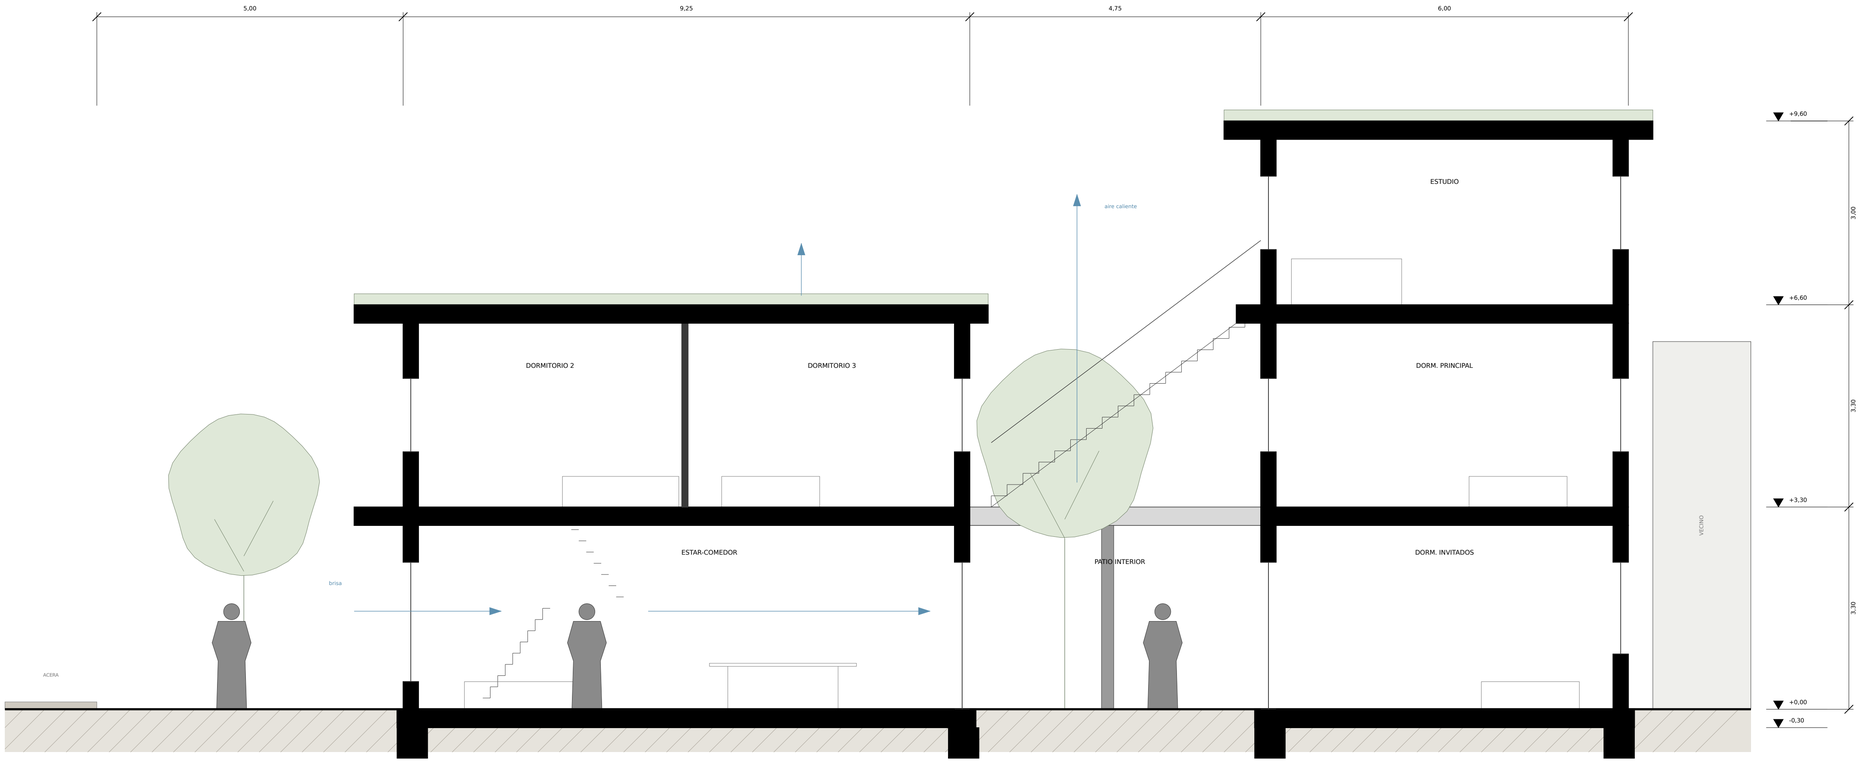

SECCIÓN LONGITUDINAL A-A'

E 1:50

0 1 2 5 10 m

NOTAS

Forjados y cubiertas: losa de hormigón armado e=30 cm.

Muros portantes: fábrica de ladrillo macizo 25 cm / hormigón.

Altura libre 3,00 m (planta) y 2,70 m (estudio).

Cubiertas vegetales extensivas con pendiente del 2 %.

Terreno plano; cota 0,00 = rasante de la calle.

Cota de coronación 9,60 m (hipótesis normativa).

Flechas azules: ventilación cruzada y efecto chimenea.

CASO_006 · PROPUESTA B	ESCALA	LÁMINA
SECCIÓN LONGITUDINAL A-A'	**1:50**	**S01** Anteproyecto