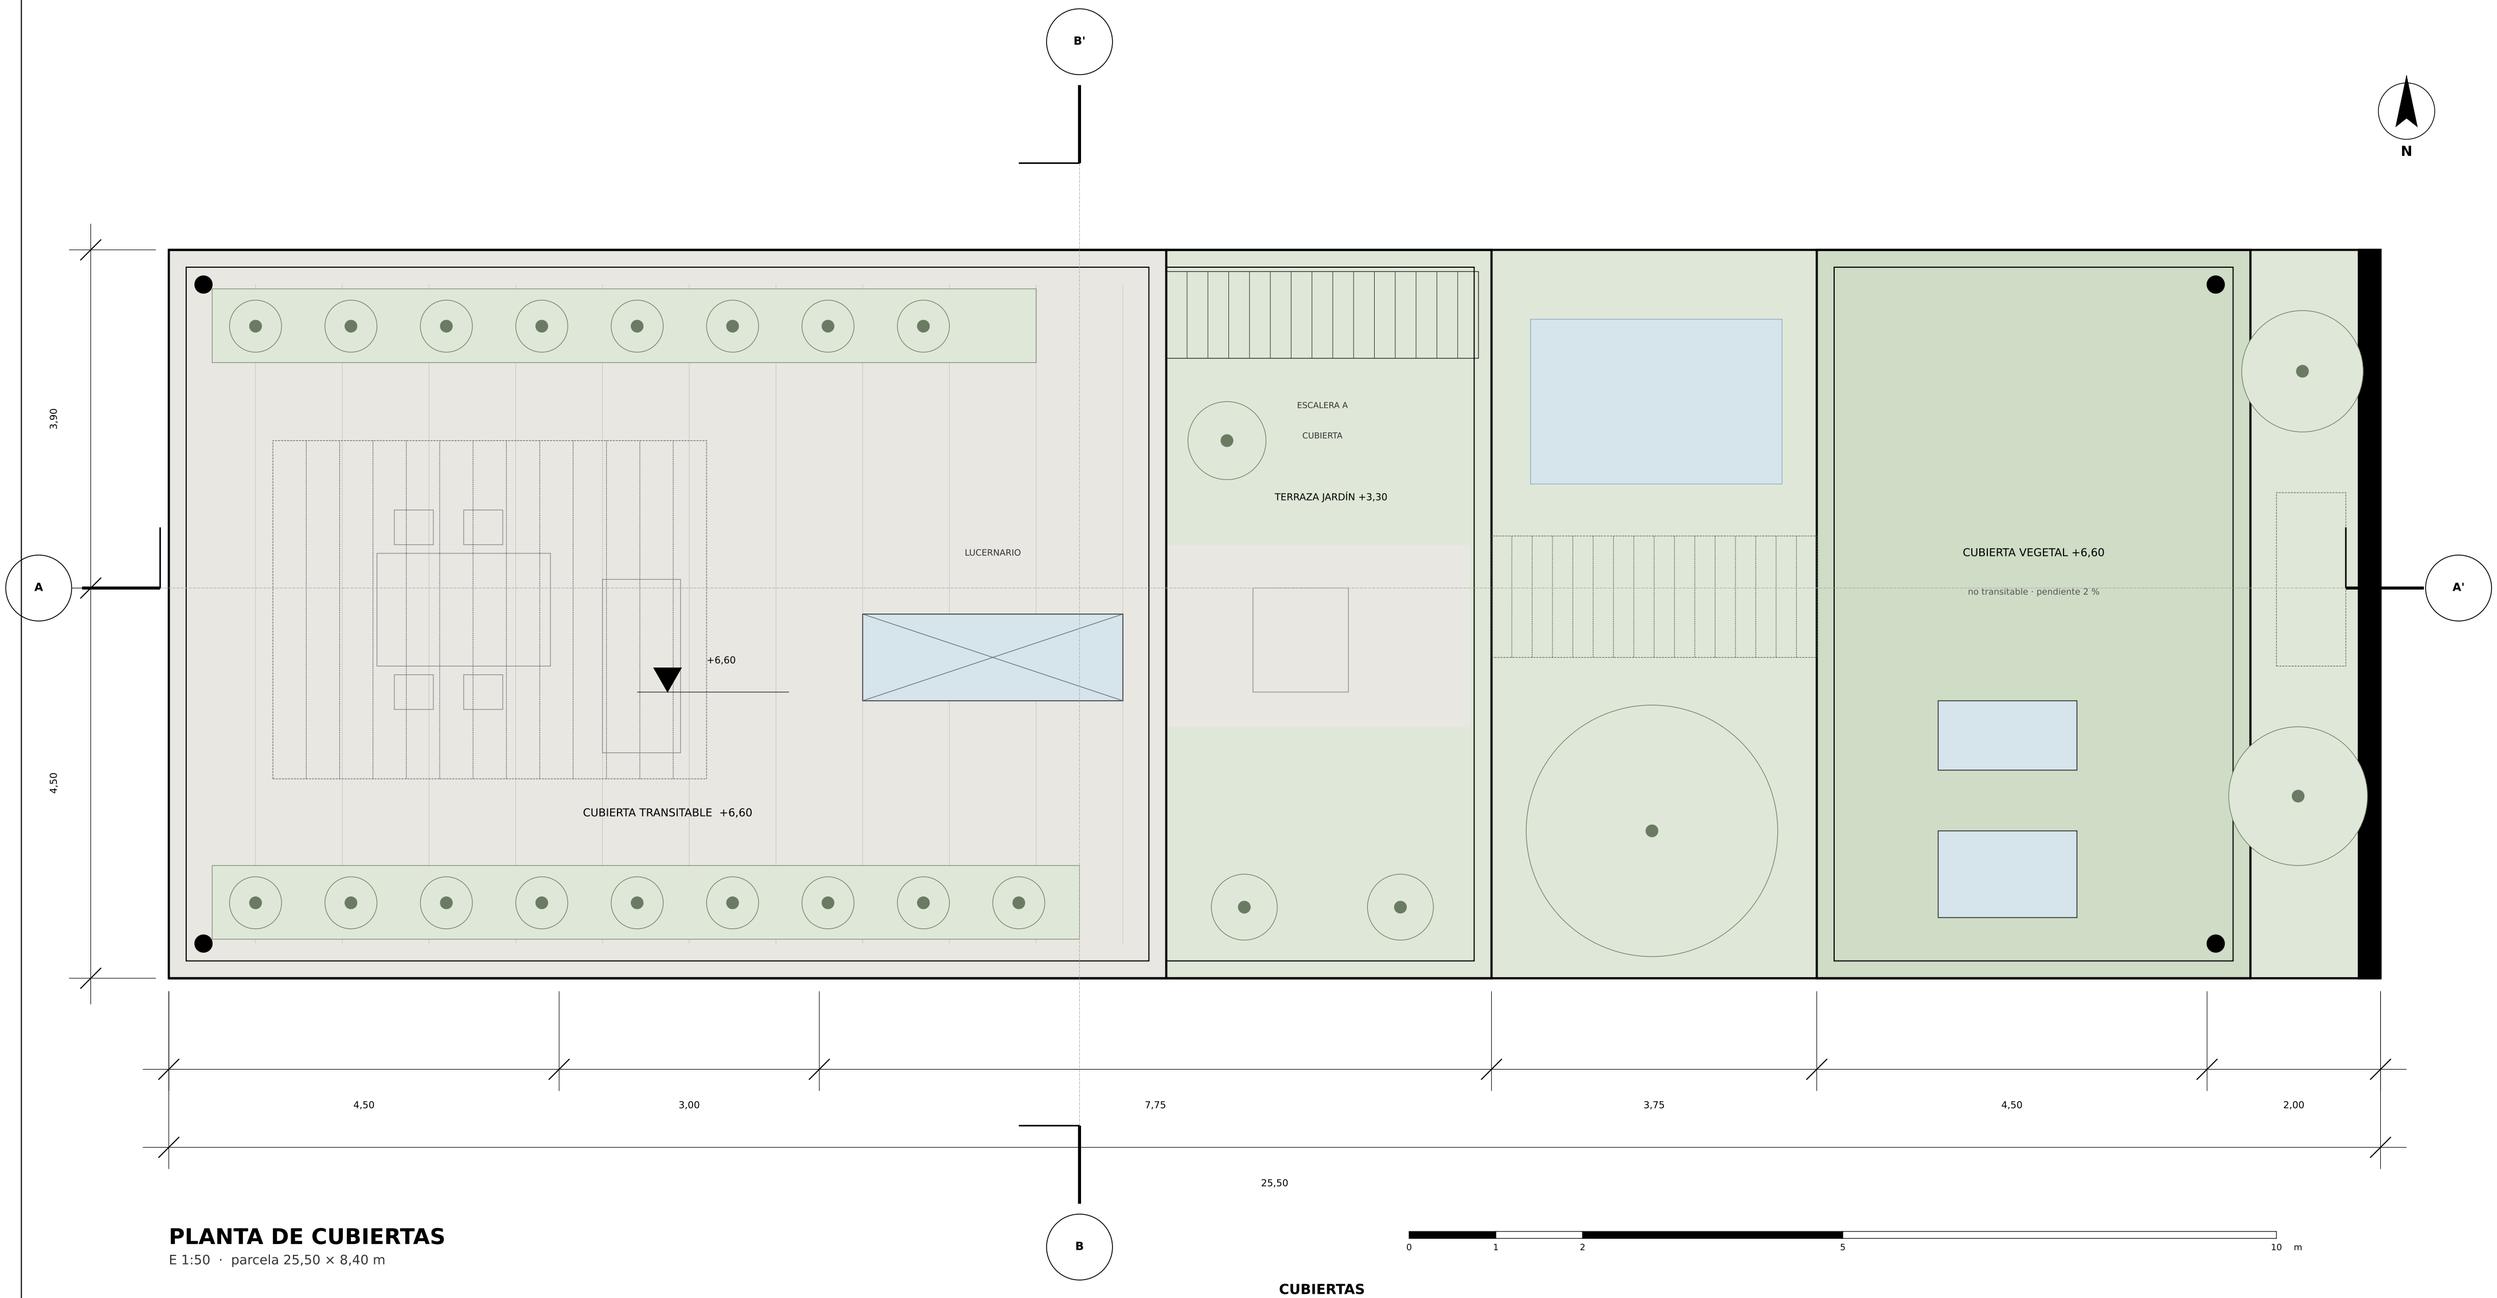

PLANTA DE CUBIERTAS

E 1:50 · parcela 25,50 × 8,40 m

LEYENDA

- Muro de hormigón / medianera (cortado)
- Tabique de ladrillo (cortado)
- Interior
- Exterior pavimentado
- Vegetación / patio
- Agua

Cotas en metros. Celosía de madera en trazo marrón claro.

CUBIERTAS

· Cubierta transitable +6,60 sobre dormitorios y sala superior: pavimento filtrante, jardineras y pérgola.

· Cubierta vegetal extensiva (sedum) +6,60 sobre dormitorio principal.

· Terraza jardín +3,30 sobre el salón. Pendientes 2 % hacia bajantes y aljibe pluvial.

· Lucernario sobre sala superior.

CASO_006 · PROPUESTA C Anteproyecto · vivienda unifamiliar entre medianeras	Escala 1:50	
Planta de cubiertas +6,60	Lámina **P03**	Anteproyecto