


EDIFICIO 3 · LADO INTERIOR **EDIFICIO 2 · CENTRAL** **EDIFICIO 1 · LADO AGUA**

SECCIÓN LONGITUDINAL A-A' (y = 8,80)

E 1:100

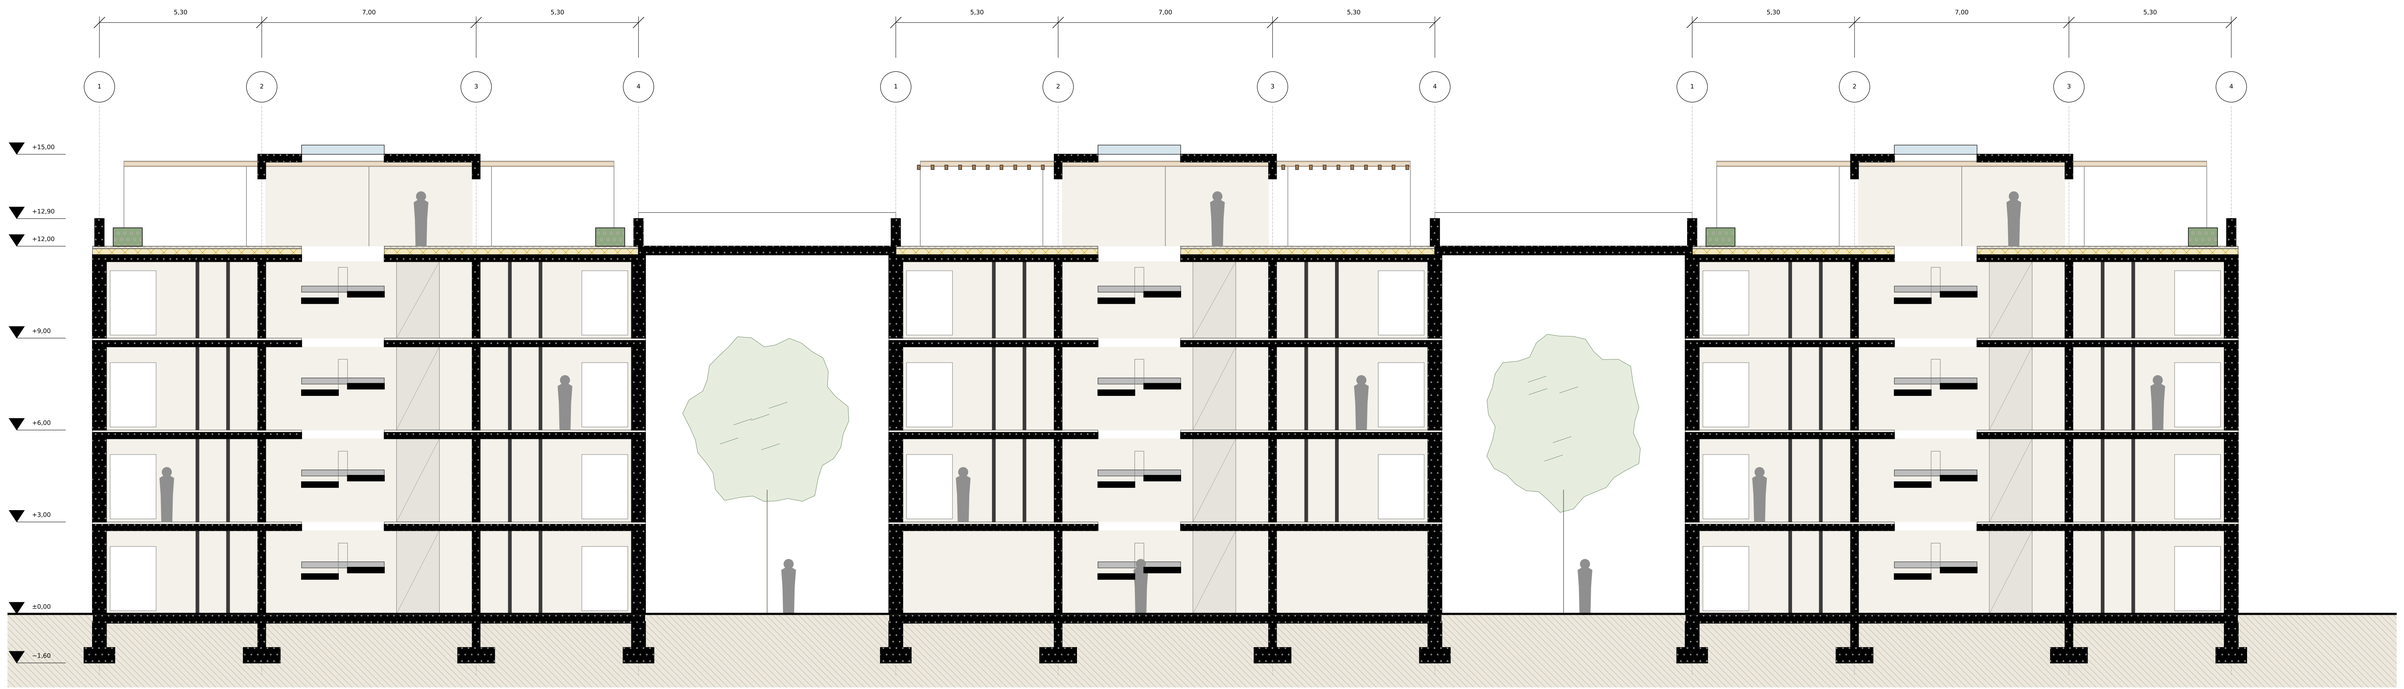

ALZADO SUR (hacia el patio y la lámina de agua)

E 1:100

CASO_007 · PROPUESTA A Anteproyecto	ESCALA	LÁMINA
Sección longitudinal A-A' y alzado sur · 1:100	**1:100**	**S01**