


C · CUBIERTA Y PETO

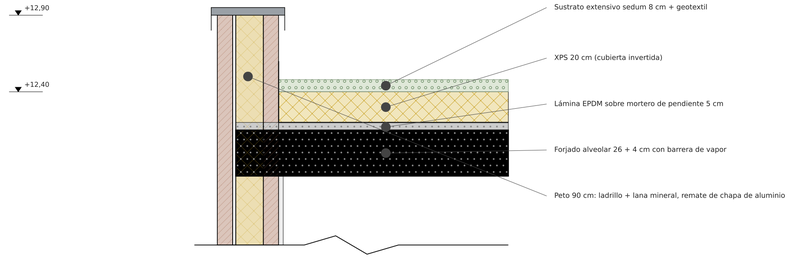

B · FORJADO TIPO, BALCÓN Y CARPINTERÍA

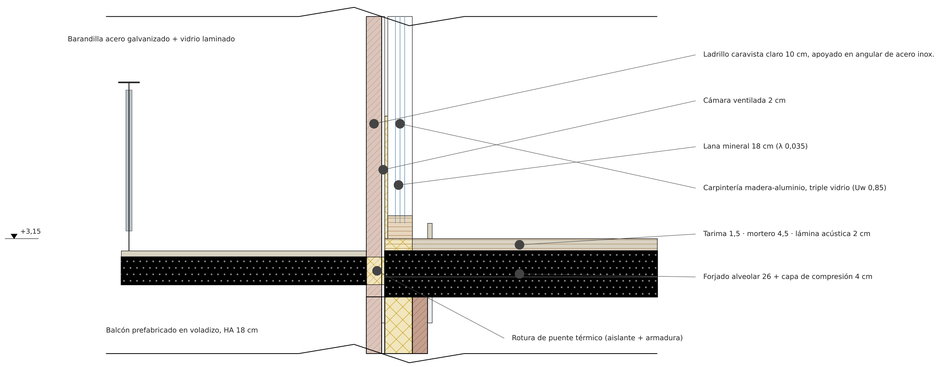

A · ARRANQUE Y CIMENTACIÓN

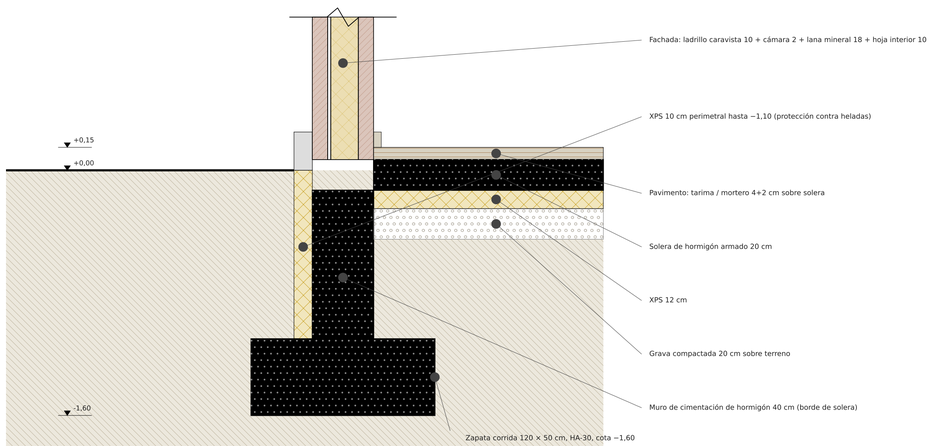

COMPOSICIÓN DE CERRAMIENTOS (clima Dfb)

Elemento	Composición (exterior → interior)	e (cm)	U (W/m²K)
Fachada	ladrillo 10 · cámara 2 · lana mineral 18 · hoja interior 10	40	≈ 0,17
Cubierta invertida	sedum 8 · XPS 20 · EPDM · pendiente 5 · forjado 30	63	≈ 0,16
Forjado entre viviendas	tarima 1,5 · mortero 4,5 · acústica 2 · alveolar 26 + 4	38	Rw ≥ 58 dB
Solera sobre terreno	acabado 8 · hormigón 20 · XPS 12 · grava 20	60	≈ 0,26
Balcón en voladizo	losa prefabricada 18 · rotura de puente térmico 12 · barandilla acero	18	ψ ≤ 0,10
Carpintería	madera-aluminio, triple vidrio bajo emisivo	—	Uw 0,85

Criterios: construcción tradicional y contrastada (fábrica, hormigón prefabricado), puentes térmicos resueltos en balcón y arranque, hermeticidad al aire continua en la cara interior del aislante, drenaje perimetral.

El balcón no apoya en el terreno: voladizo prefabricado anclado al forjado.

SECCIÓN CONSTRUCTIVA DE FACHADA

E 1:20

CASO_007 · PROPUESTA B

Escala 1:20

Detalle constructivo de fachada

Lámina D01

Anteproyecto · vivienda colectiva · 3 edificios exentos

Anteproyecto