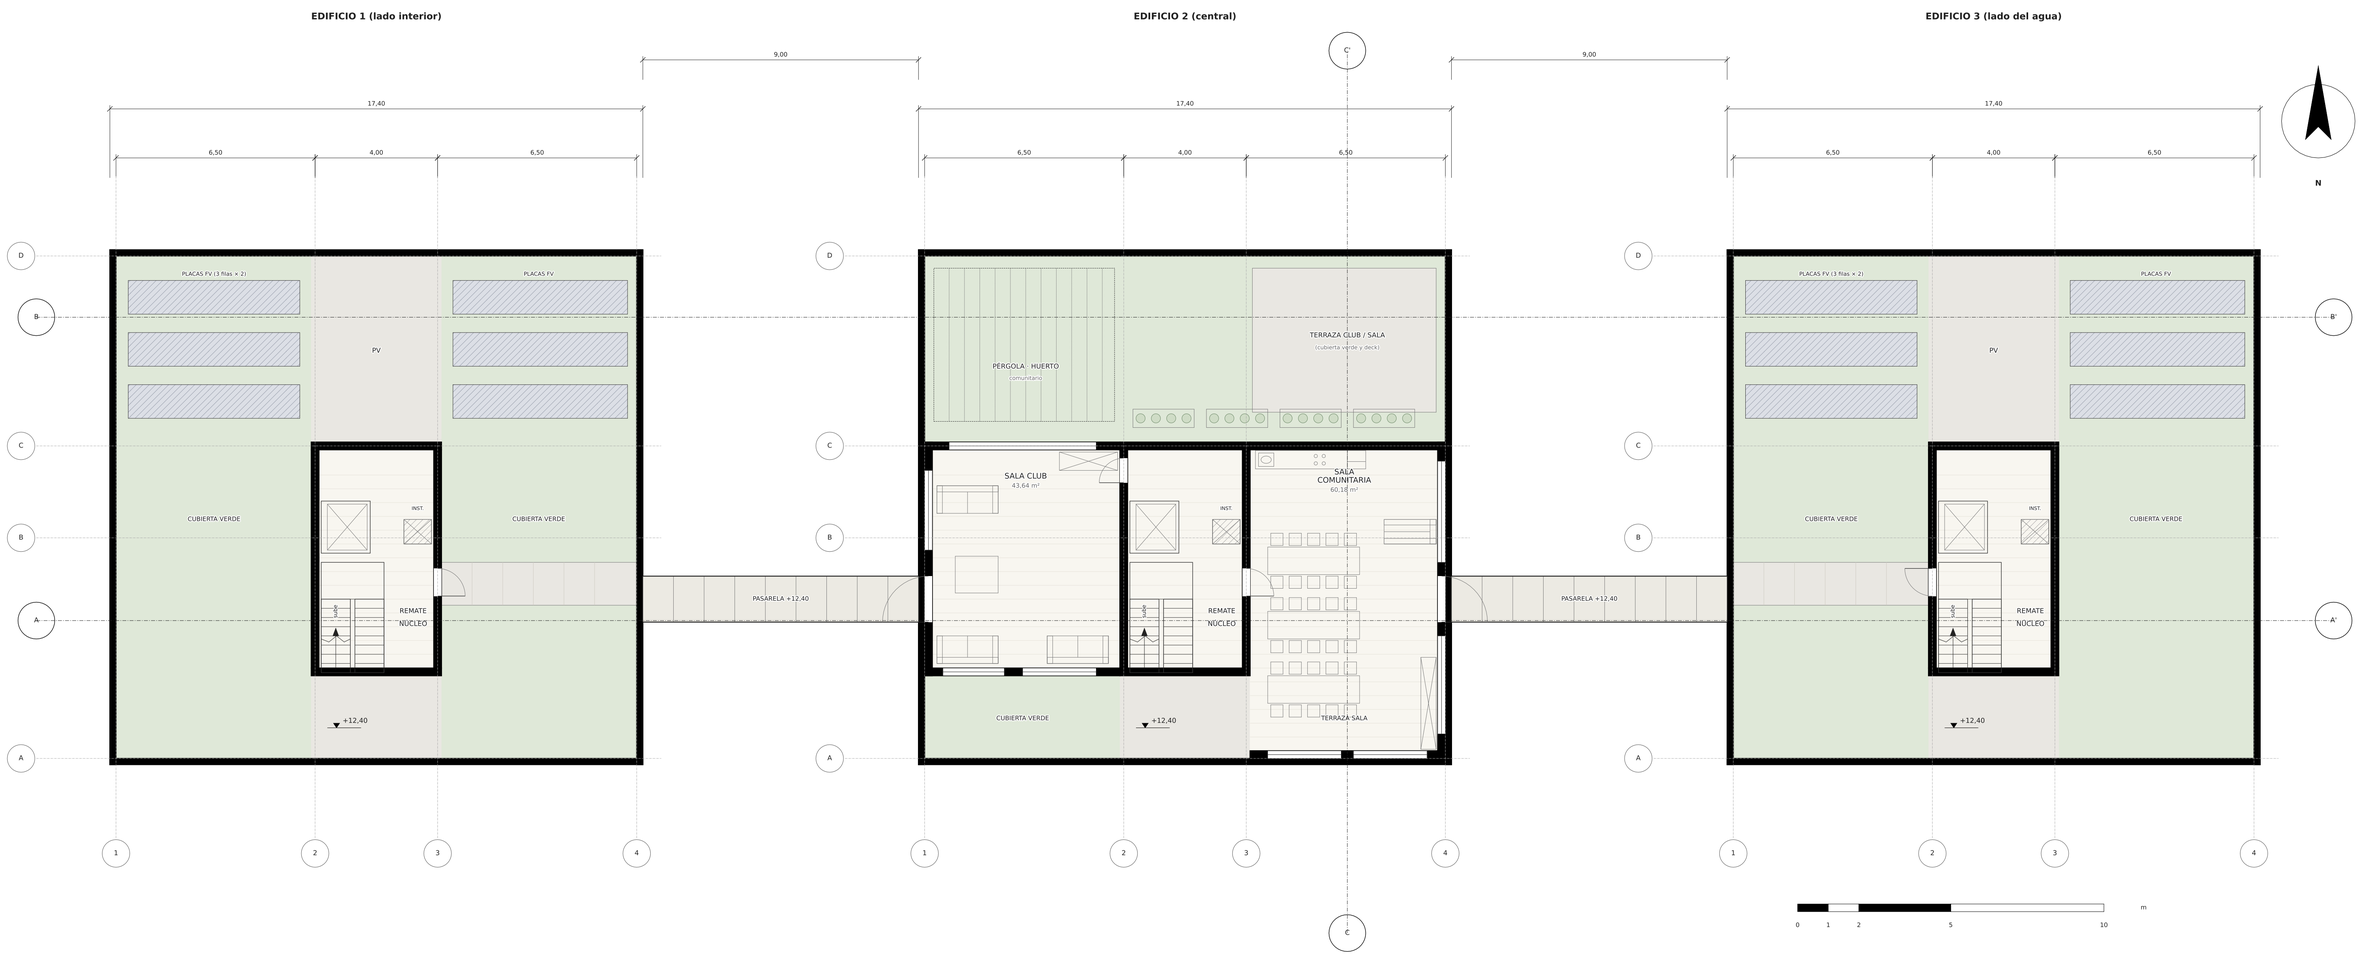


Sala comunitaria y sala club sobre el edificio central (no computan). Las pasarelas unen los tres núcleos a +12,40 y permiten acceder a la sala desde cada escalera; sirven además de segunda vía de evacuación entre edificios. Cubierta plana invertida con acabado verde (sedum) y placas fotovoltaicas en los edificios 1 y 3.

Leyenda: verde = cubierta vegetal · gris claro = deck / pavimento flotante · trazo discontinuo = pérgola de acero y madera por encima del plano de corte

PLANTA DE ÁTICO Y CUBIERTAS · NIVEL +12,40
E 1:100

CASO_007 · PROPUESTA B

Escala 1:100

Planta de ático y cubiertas

Lámina P03

Anteproyecto · vivienda colectiva · 3 edificios exentos

Anteproyecto