

SECCIÓN B-B' (por viviendas norte, y = 14,60)

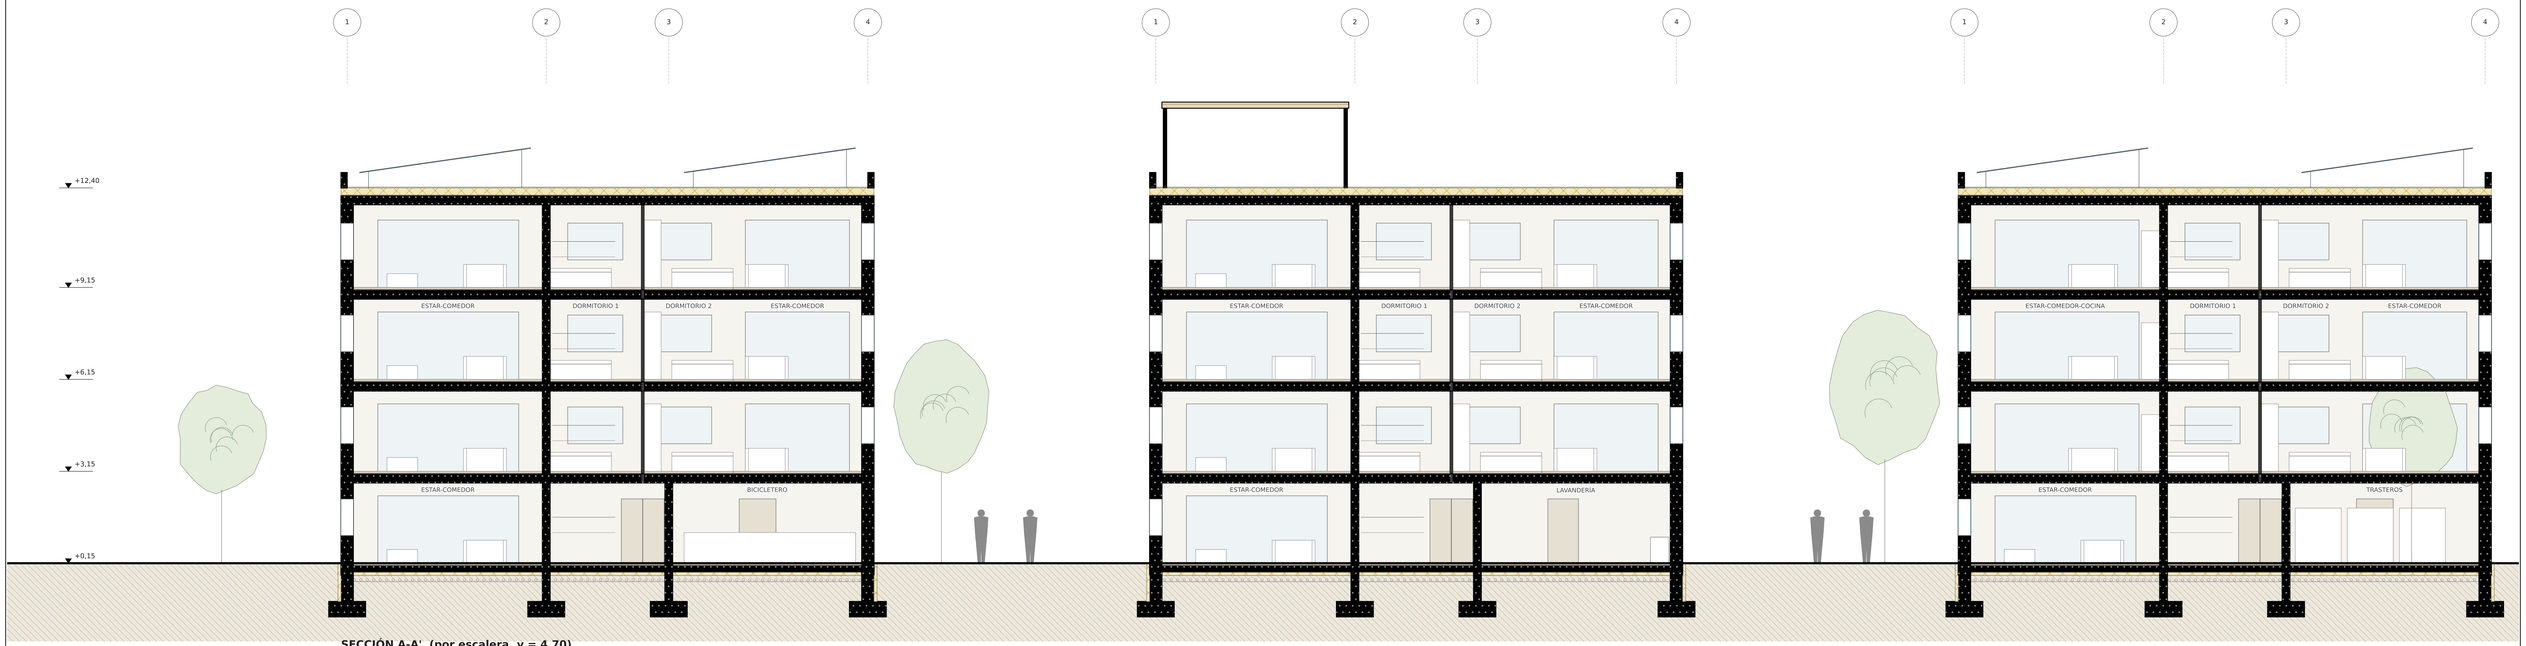

SECCIÓN A-A' (por escalera, y = 4,70)

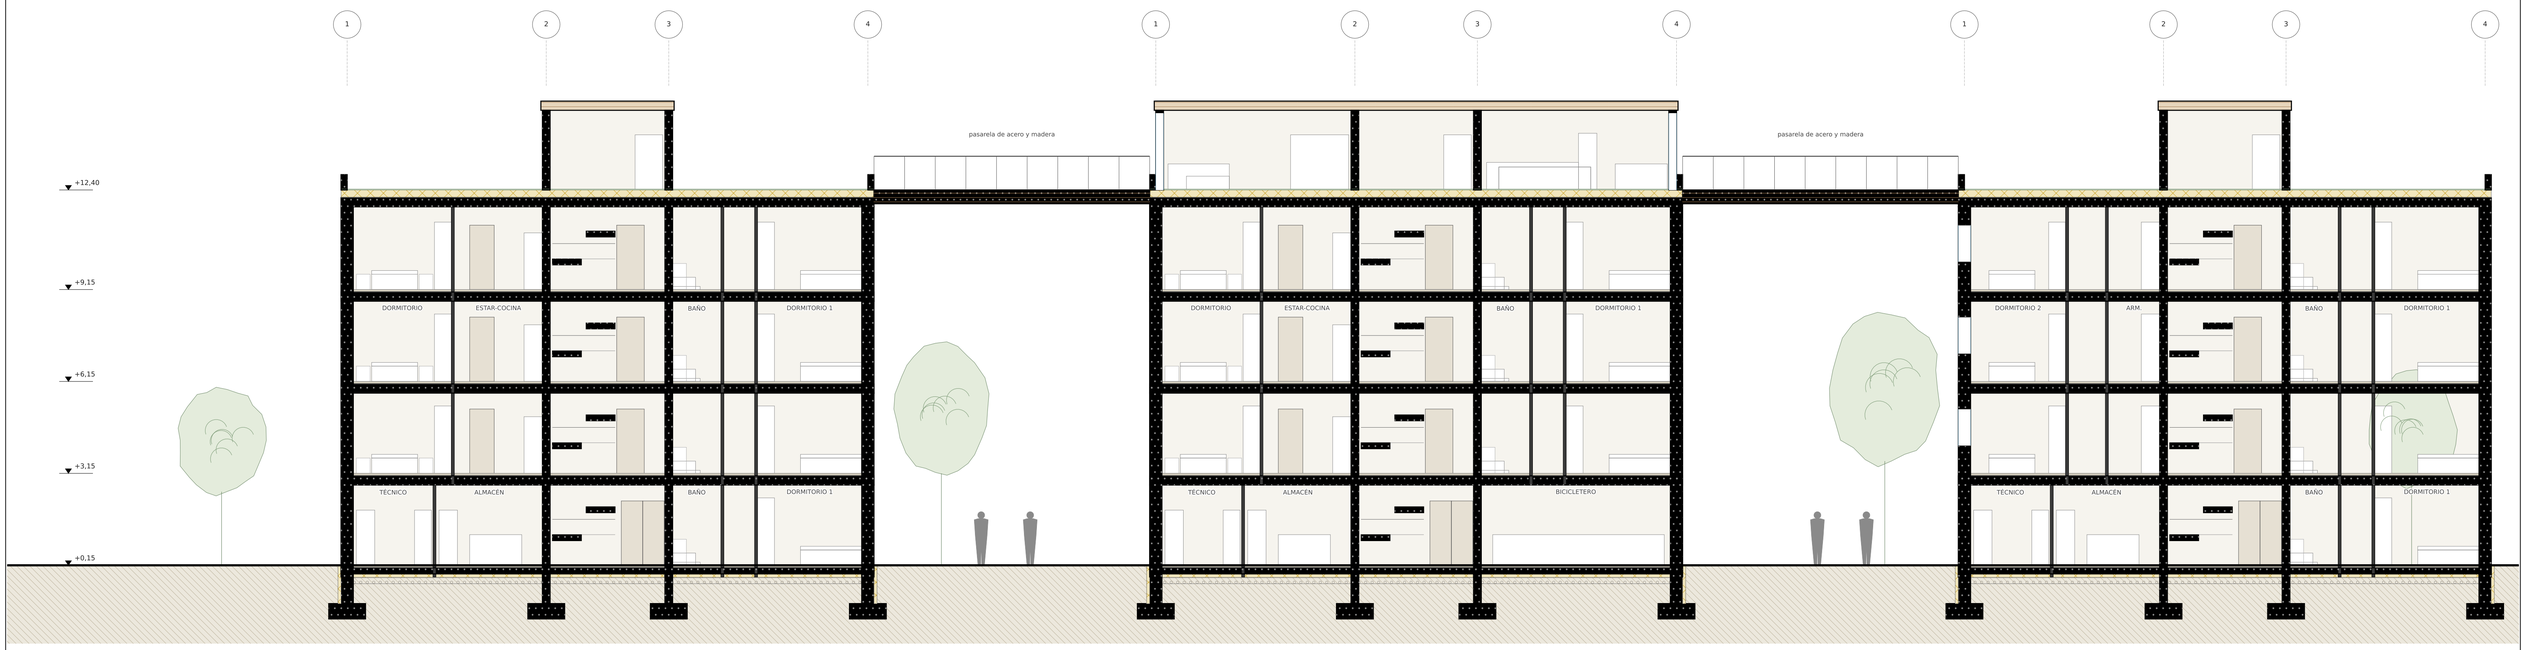

SECCIONES LONGITUDINALES A-A' Y B-B'

E 1:100

Cortadas: forjado alveolar 26+4 cm, muros de hormigón de los ejes 2, 3 y C, fachada, solera con grava y XPS, zapatas corridas (−1,60). En proyección: mobiliario, carpinterías de muros de fondo y escalera.

Hormigón armado

Terreno natural

Aislante térmico

Madera (CLT, pasarela)

CASO_007 · PROPUESTA B

Escala 1:100

Secciones longitudinales A-A' y B-B'

Lámina S01

Anteproyecto · vivienda colectiva · 3 edificios exentos

Anteproyecto