SECCIÓN C-C' (transversal por el edificio central, x = 14,00)


Fachada: ladrillo caravista 10 · cámara 2 · lana mineral 18 · hoja interior 10 (e = 0,40)

Forjado: alveolar 26 + 4 cm · aislamiento acústico · mortero · tarima

Balcón en voladizo con rotura de puente térmico (1,60 m) · barandilla de acero

Cubierta invertida: forjado 30 · barrera de vapor · pendiente · XPS 20 · EPDM · sedum

Solera 20 · XPS 12 · grava 20 · zapata corrida 1,20 × 0,50 a −1,60

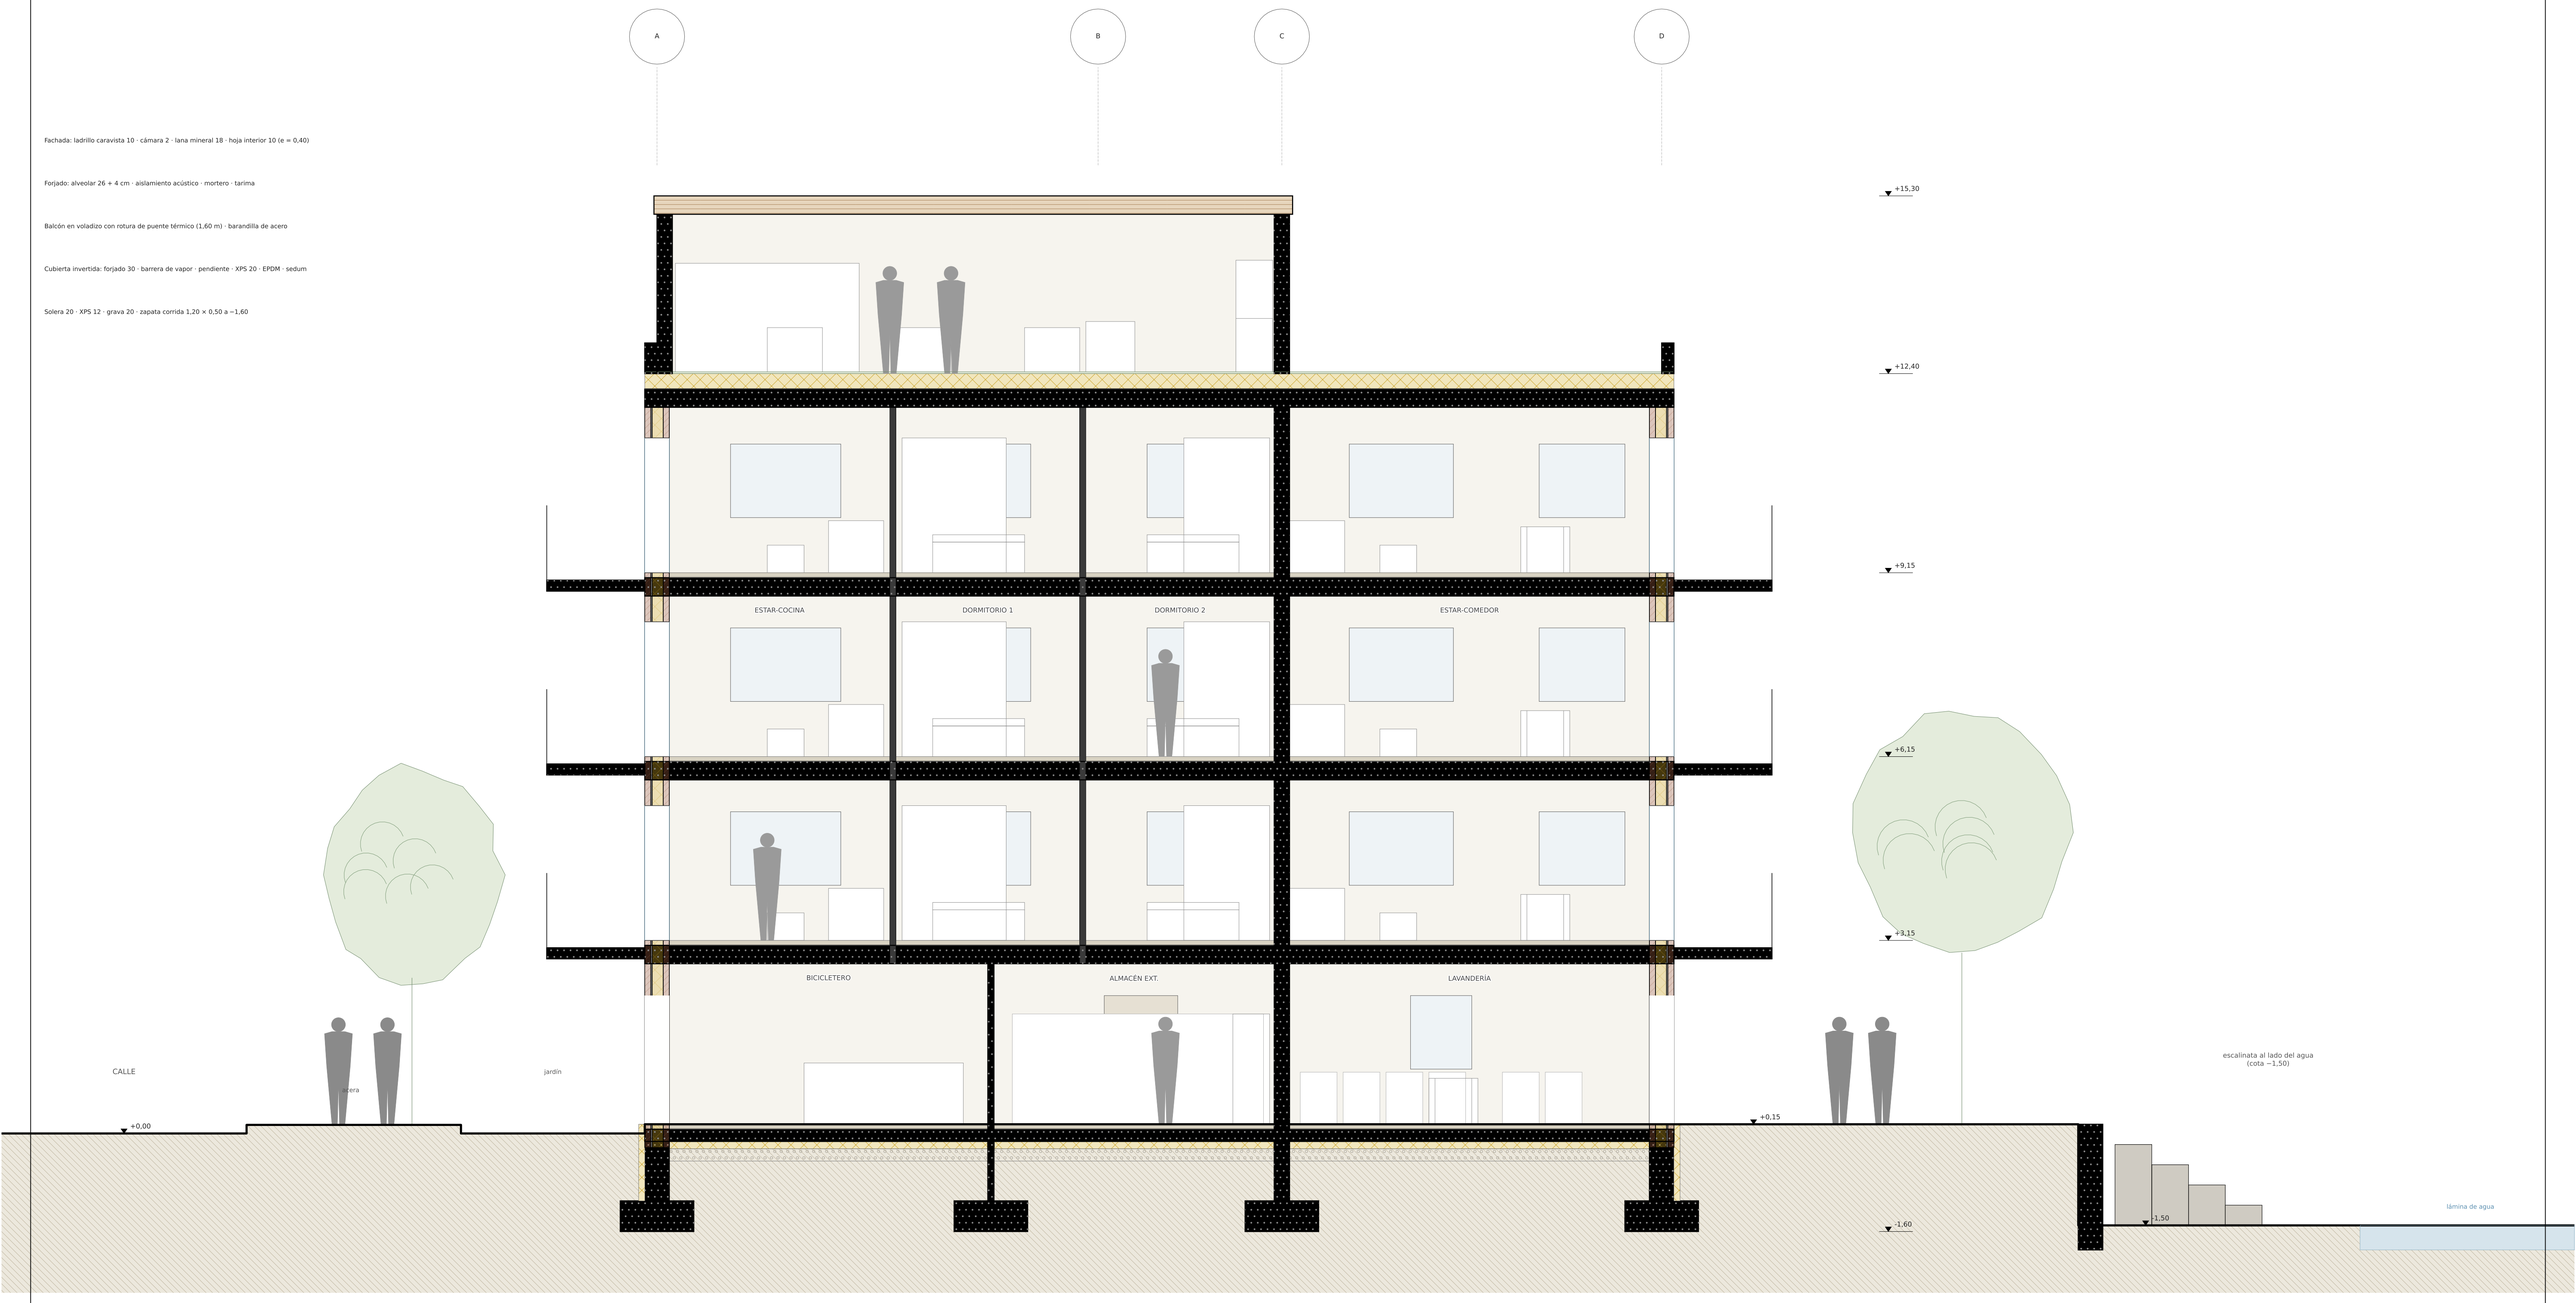

SECCIÓN TRANSVERSAL C-C'
E 1:50

CASO_007 · PROPUESTA B

Escala 1:50

Sección transversal C-C'

Lámina S02

Anteproyecto · vivienda colectiva · 3 edificios exentos

Anteproyecto