
SECCIÓN CONSTRUCTIVA DE FACHADA · cimentación, forjado tipo y cubierta

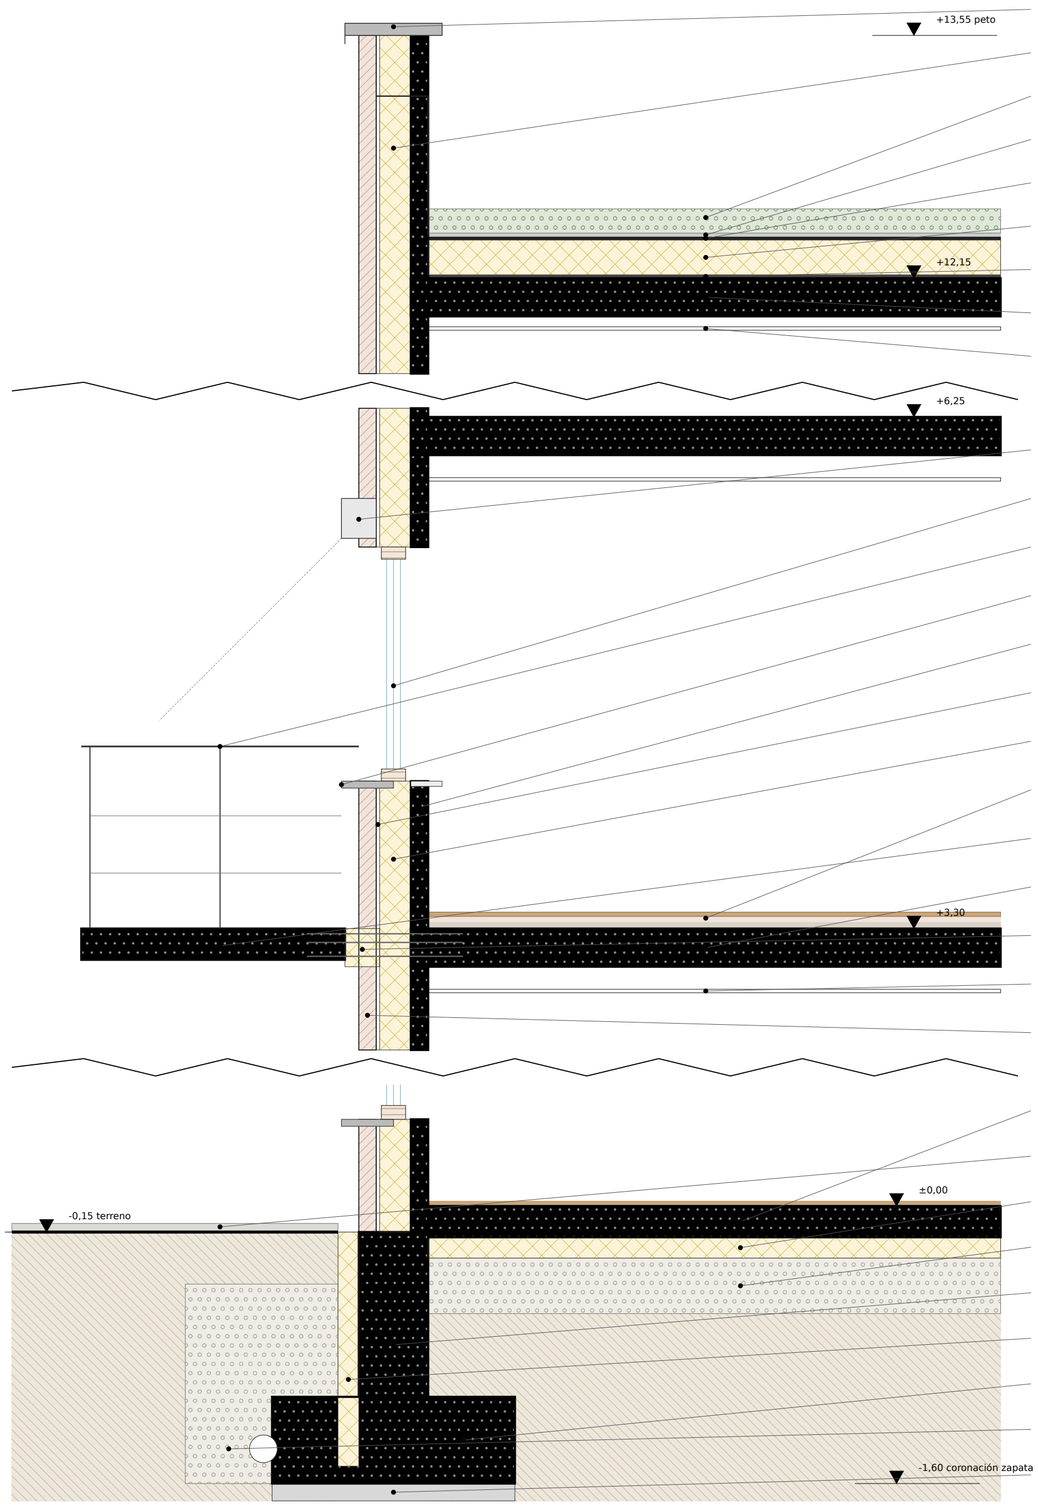

- Albardilla de chapa de aluminio con goterón
- Peto: mismas capas de fachada
- Sustrato 10 cm + sedum
- Geotextil de protección
- Impermeabilización lámina sintética
- Aislante PIR 20 cm, λ = 0,022 W/mK
- Barrera de vapor
- Forjado HA-30 e = 22 cm, pendiente 2 %
- Falso techo yeso laminado
- Cajón de toldo textil (según boceto)
- Carpintería madera-aluminio, triple vidrio Uw = 0,95
- Barandilla de acero lacado con tensores
- Vierteaguas de chapa con goterón
- Hoja interior hormigón prefabricado 10 cm
- Cámara de aire 2 cm
- Lana mineral 18 cm, λ = 0,035 W/mK
- Mortero 5 cm + aislante acústico 3 cm + tarima 1,5 cm
- Balcón prefabricado HA 18 cm (i = 1,5 %), sin apoyo en suelo
- Forjado losa HA-30 e = 22 cm
- Rotura de puente térmico con armaduras de conexión
- Falso techo yeso laminado 12,5 mm
- Ladrillo caravista claro 10 cm
- Solera HA 15 cm + acabado
- Pavimento exterior prefabricado 5 cm sobre arena
- Aislante XPS 12 cm
- Grava compactada 30 cm
- Muro de cimentación HA-30, e = 0,40 m
- Aislante XPS 12 cm perimetral
- Zapata corrida HA-30, 1,40 x 0,50 m, bajo helada
- Drenaje perimetral: tubo Ø110 + grava 20/40
- Hormigón de limpieza 10 cm

DETALLE D01 · SECCIÓN DE FACHADA

E 1:25

Fachada: U ≈ 0,19 W/m²K · cubierta: U ≈ 0,11 W/m²K · solera: U ≈ 0,25 W/m²K

CASO_007 · PROPUESTA C Anteproyecto · vivienda colectiva en propiedad, tres edificios	Dibujo: proyectista C	
Detalle D01 · sección constructiva	Escala 1:25	**Lámina D01**