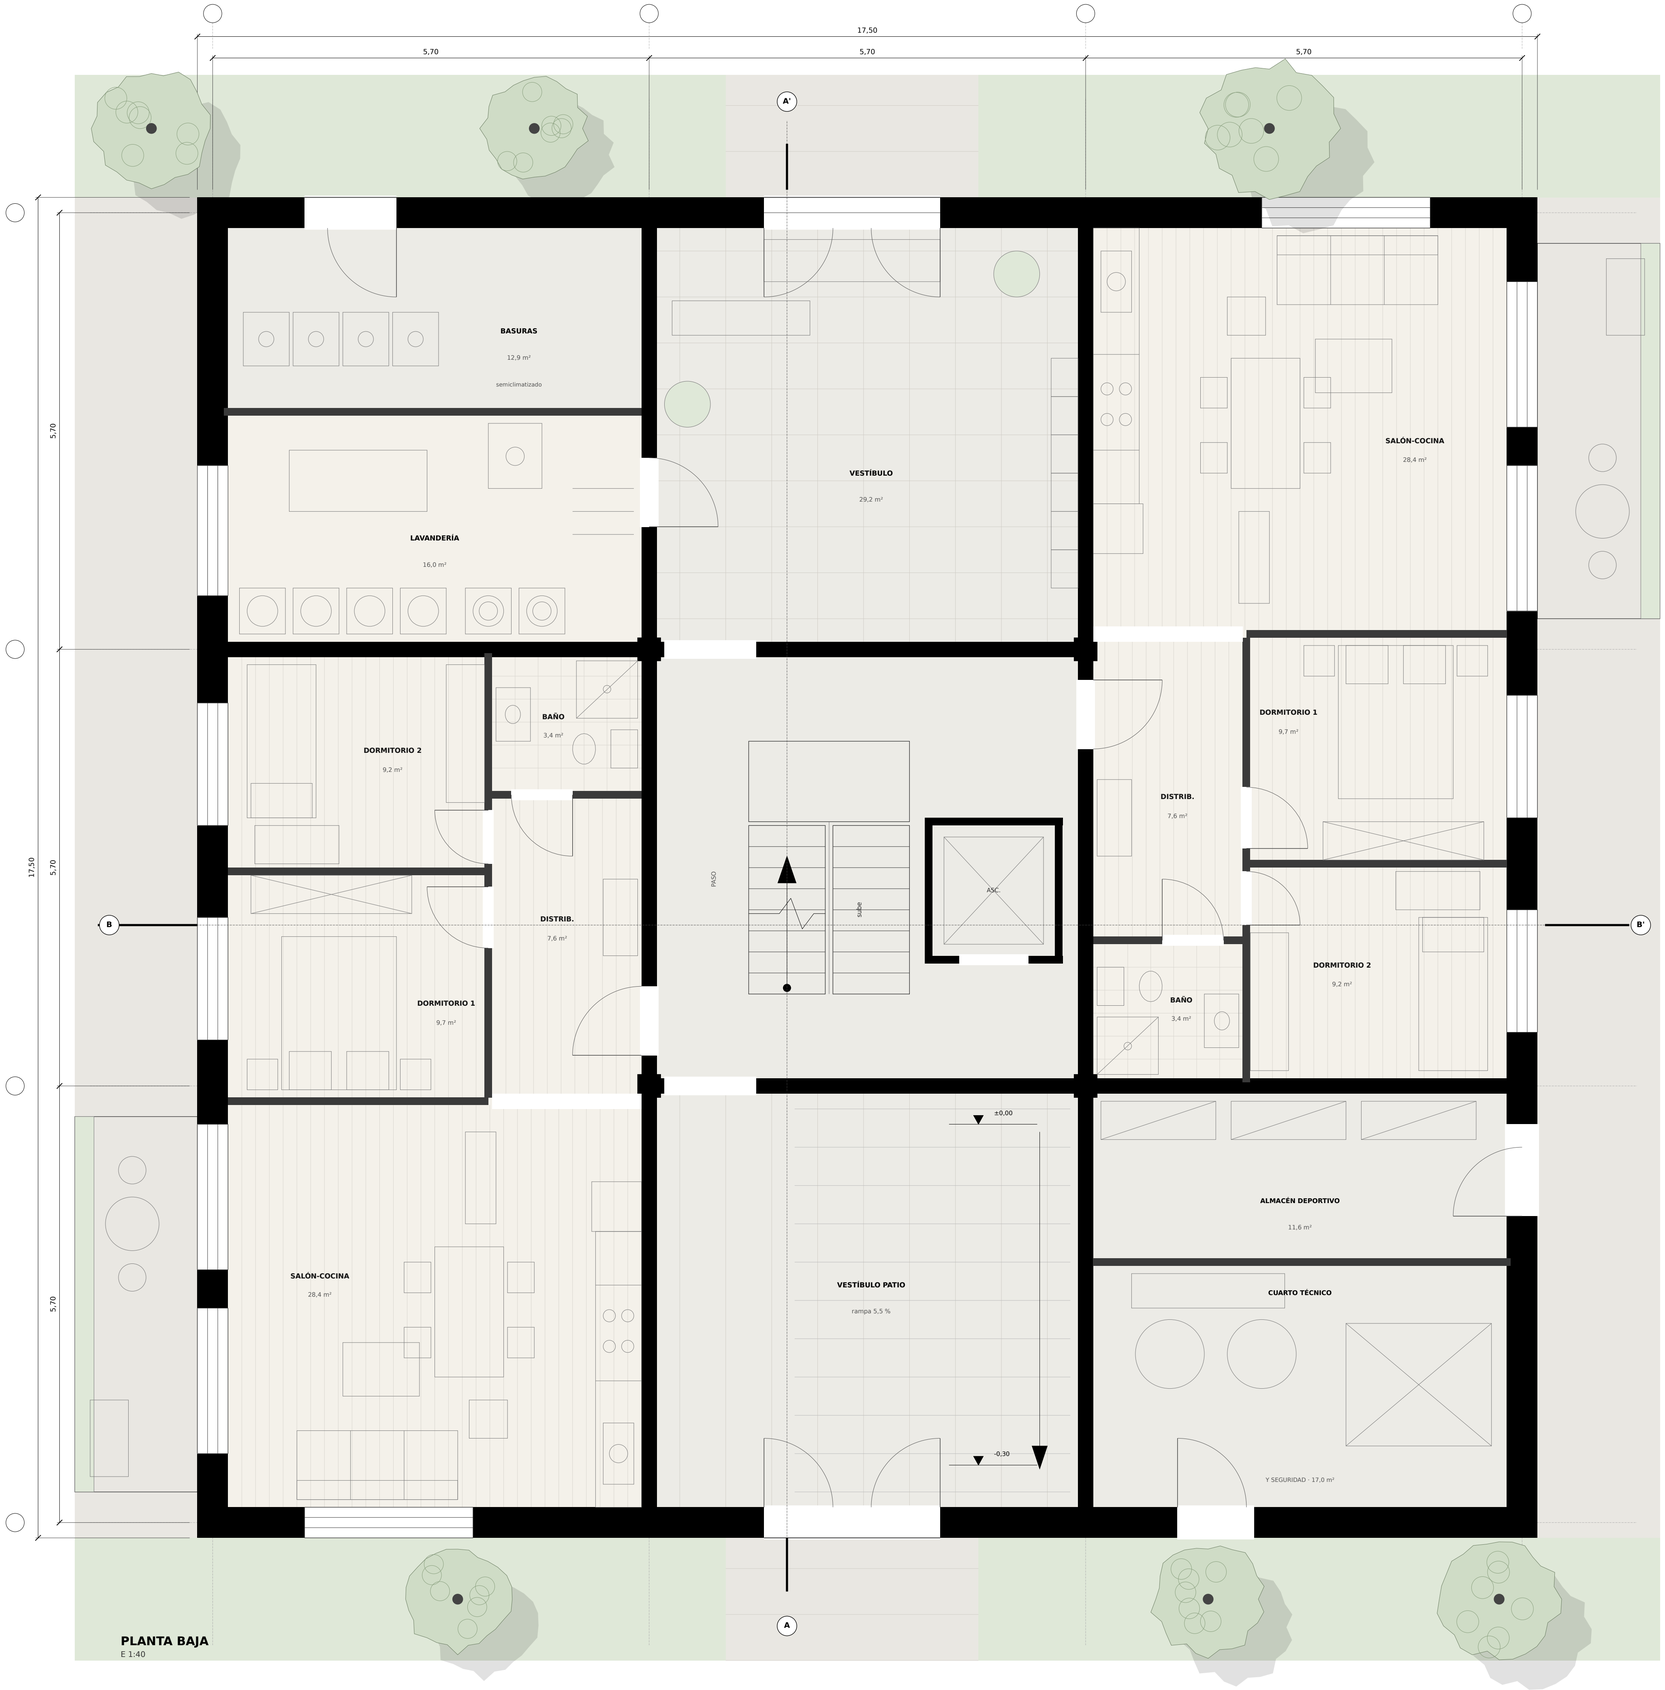


N

PLANTA BAJA

Cota del forjado: ±0,00 (calle) / -0,30 (patio)

Módulo de 17,10 x 17,10 m entre ejes · 17,50 x 17,50 m construidos

CUADRO DE SUPERFICIES ÚTILES (m²)

Nº	Estancia	m²
1	Vestíbulo calle	29,2
2	Núcleo escalera + ascensor	30,3
3	Vestíbulo patio (rampa)	29,2
4	Vivienda accesible O (2 hab.)	58,3
5	Vivienda E (2 hab.)	58,3
6	Lavandería	16,0
7	Basuras	12,9
8	Almacén deportivo	11,6
9	Cuarto técnico y seguridad	17,0

Los números del dibujo remiten a esta leyenda; los nombres de las estancias de las viviendas se rotulan directamente.

LEYENDA

- Muro de hormigón armado / pilar 0,30 x 0,30
- Tabique cerámico 0,10 (acabado 0,125)
- Balcón volado con rotura de puente térmico
- Ejes estructurales (1-4 / A-D)

Cota ±0,00 = calle (norte). Patio común a -0,30 (sur): rampa 5,5 % en el vestíbulo. Pasos calle-patio por el vestíbulo y el núcleo, 1,20 m libres. Edificio representado: pieza central (14 viviendas). Las otras dos piezas repiten estructura y núcleo; ver memoria para su distribución.

CASO_007 · PROPUESTA C Anteproyecto · vivienda colectiva en propiedad, tres edificios	Dibujo: proyectista C	
Planta baja	Escala 1:40	**Lámina P01**