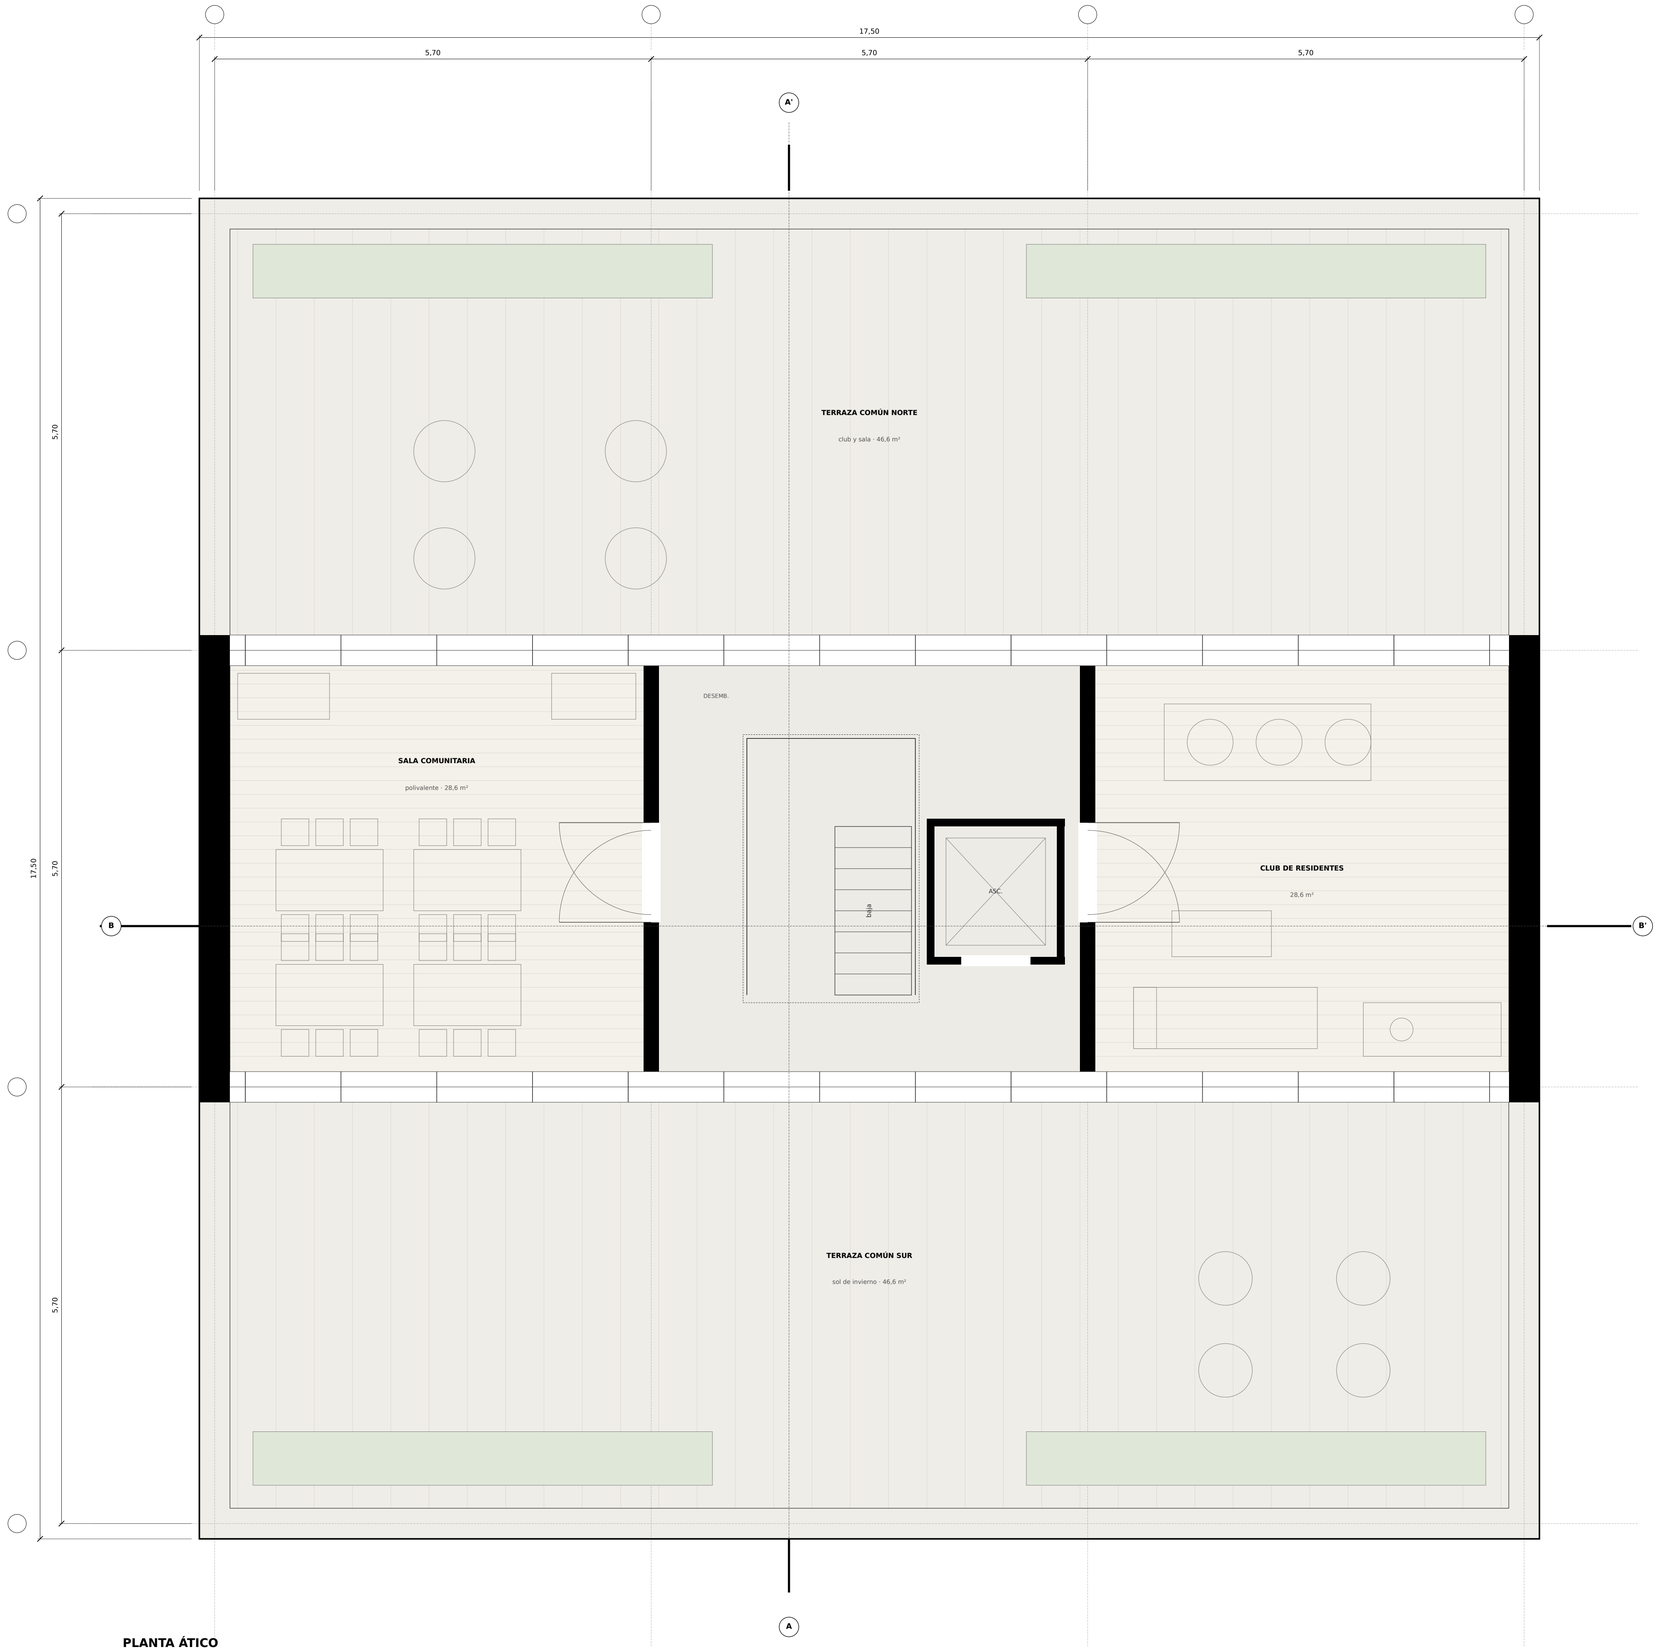

PLANTA ÁTICO
E 1:40

0 1 2 5 10 m

N

PLANTA ÁTICO

Cota del forjado: +12,15 (suelo acabado +12,55)

Módulo de 17,10 x 17,10 m entre ejes · 17,50 x 17,50 m construidos

ESPACIOS COMUNES DE ÁTICO (no computan)

Espacio	m²
Sala comunitaria polivalente	28,6
Club de residentes	28,6
Desembarco / núcleo	30,3
Terraza común N	46,6
Terraza común S	46,6

LEYENDA

- Muro de hormigón armado / pilar 0,30 x 0,30
- Tabique cerámico 0,10 (acabado 0,125)
- Balcón volado con rotura de puente térmico
- Ejes estructurales (1-4 / A-D)

La escalera llega al ático; la sala comunitaria y el club se abren a las terrazas comunes N y S.

CASO_007 · PROPUESTA C Anteproyecto · vivienda colectiva en propiedad, tres edificios	Dibujo: proyectista C	
Planta ático	Escala 1:40	**Lámina P05**