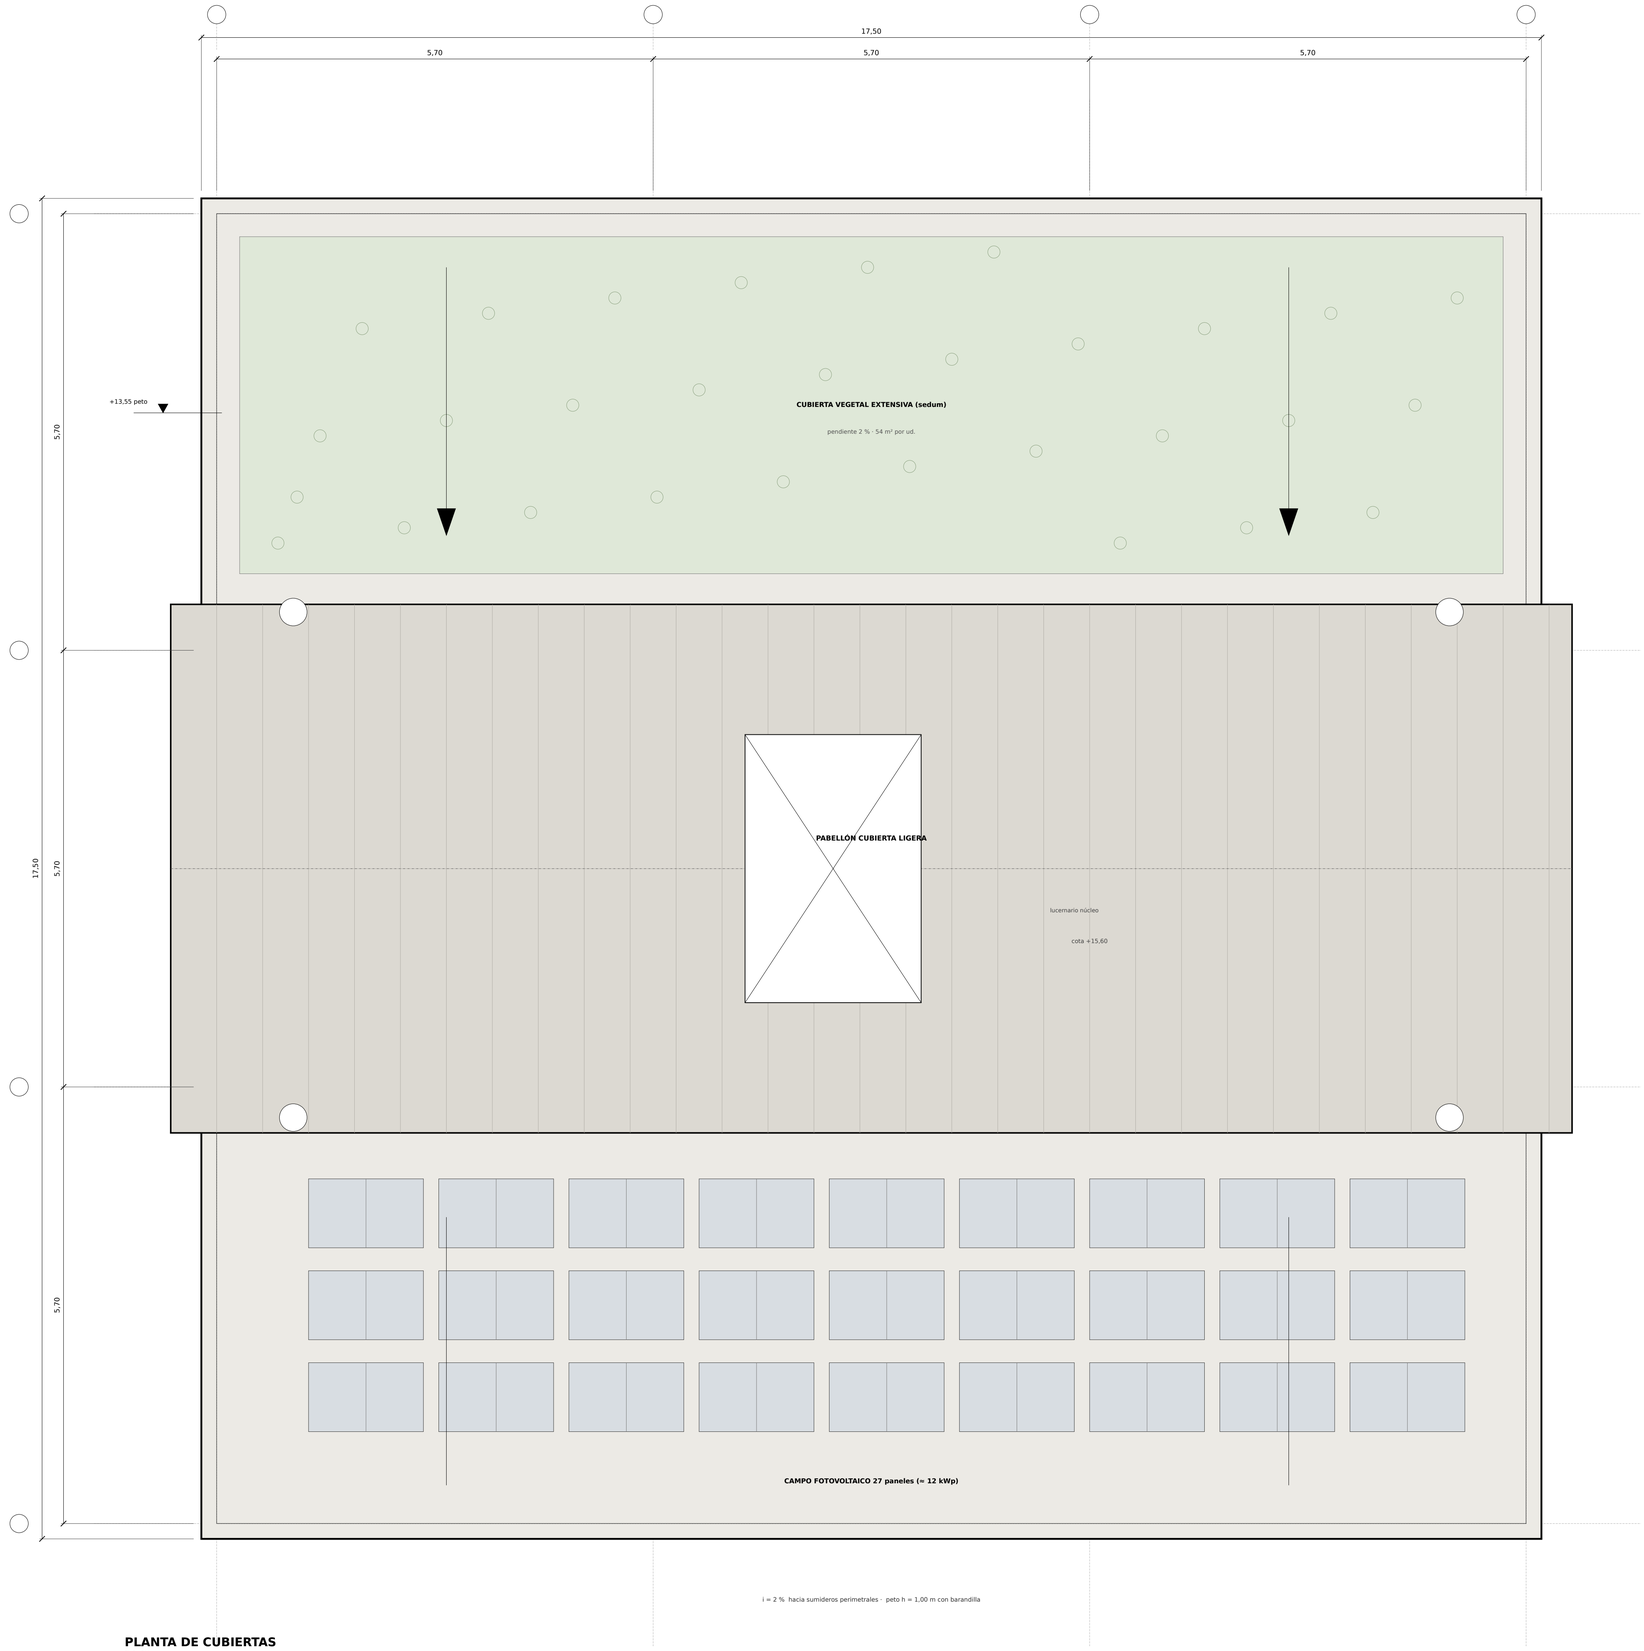

PLANTA DE CUBIERTAS
E 1:40

0 1 2 5 10 m

N

PLANTA DE CUBIERTAS

Cota del forjado: +13,55 peto / +15,60 pabellón

Módulo de 17,10 x 17,10 m entre ejes · 17,50 x 17,50 m construidos

CUBIERTA

Elemento	m²
Superficie de cubierta	306
Pabellón (vuelo incluido)	128
Sedum	54
Fotovoltaica	≈ 70 (27 paneles)

LEYENDA

- Muro de hormigón armado / pilar 0,30 x 0,30
- Tabique cerámico 0,10 (acabado 0,125)
- Balcón volado con rotura de puente térmico
- Ejes estructurales (1-4 / A-D)

Cubierta plana invertida: sedum al norte, fotovoltaica al sur.

CASO_007 · PROPUESTA C Anteproyecto · vivienda colectiva en propiedad, tres edificios	Dibujo: proyectista C	
Planta de cubiertas	Escala 1:40	**Lámina P06**