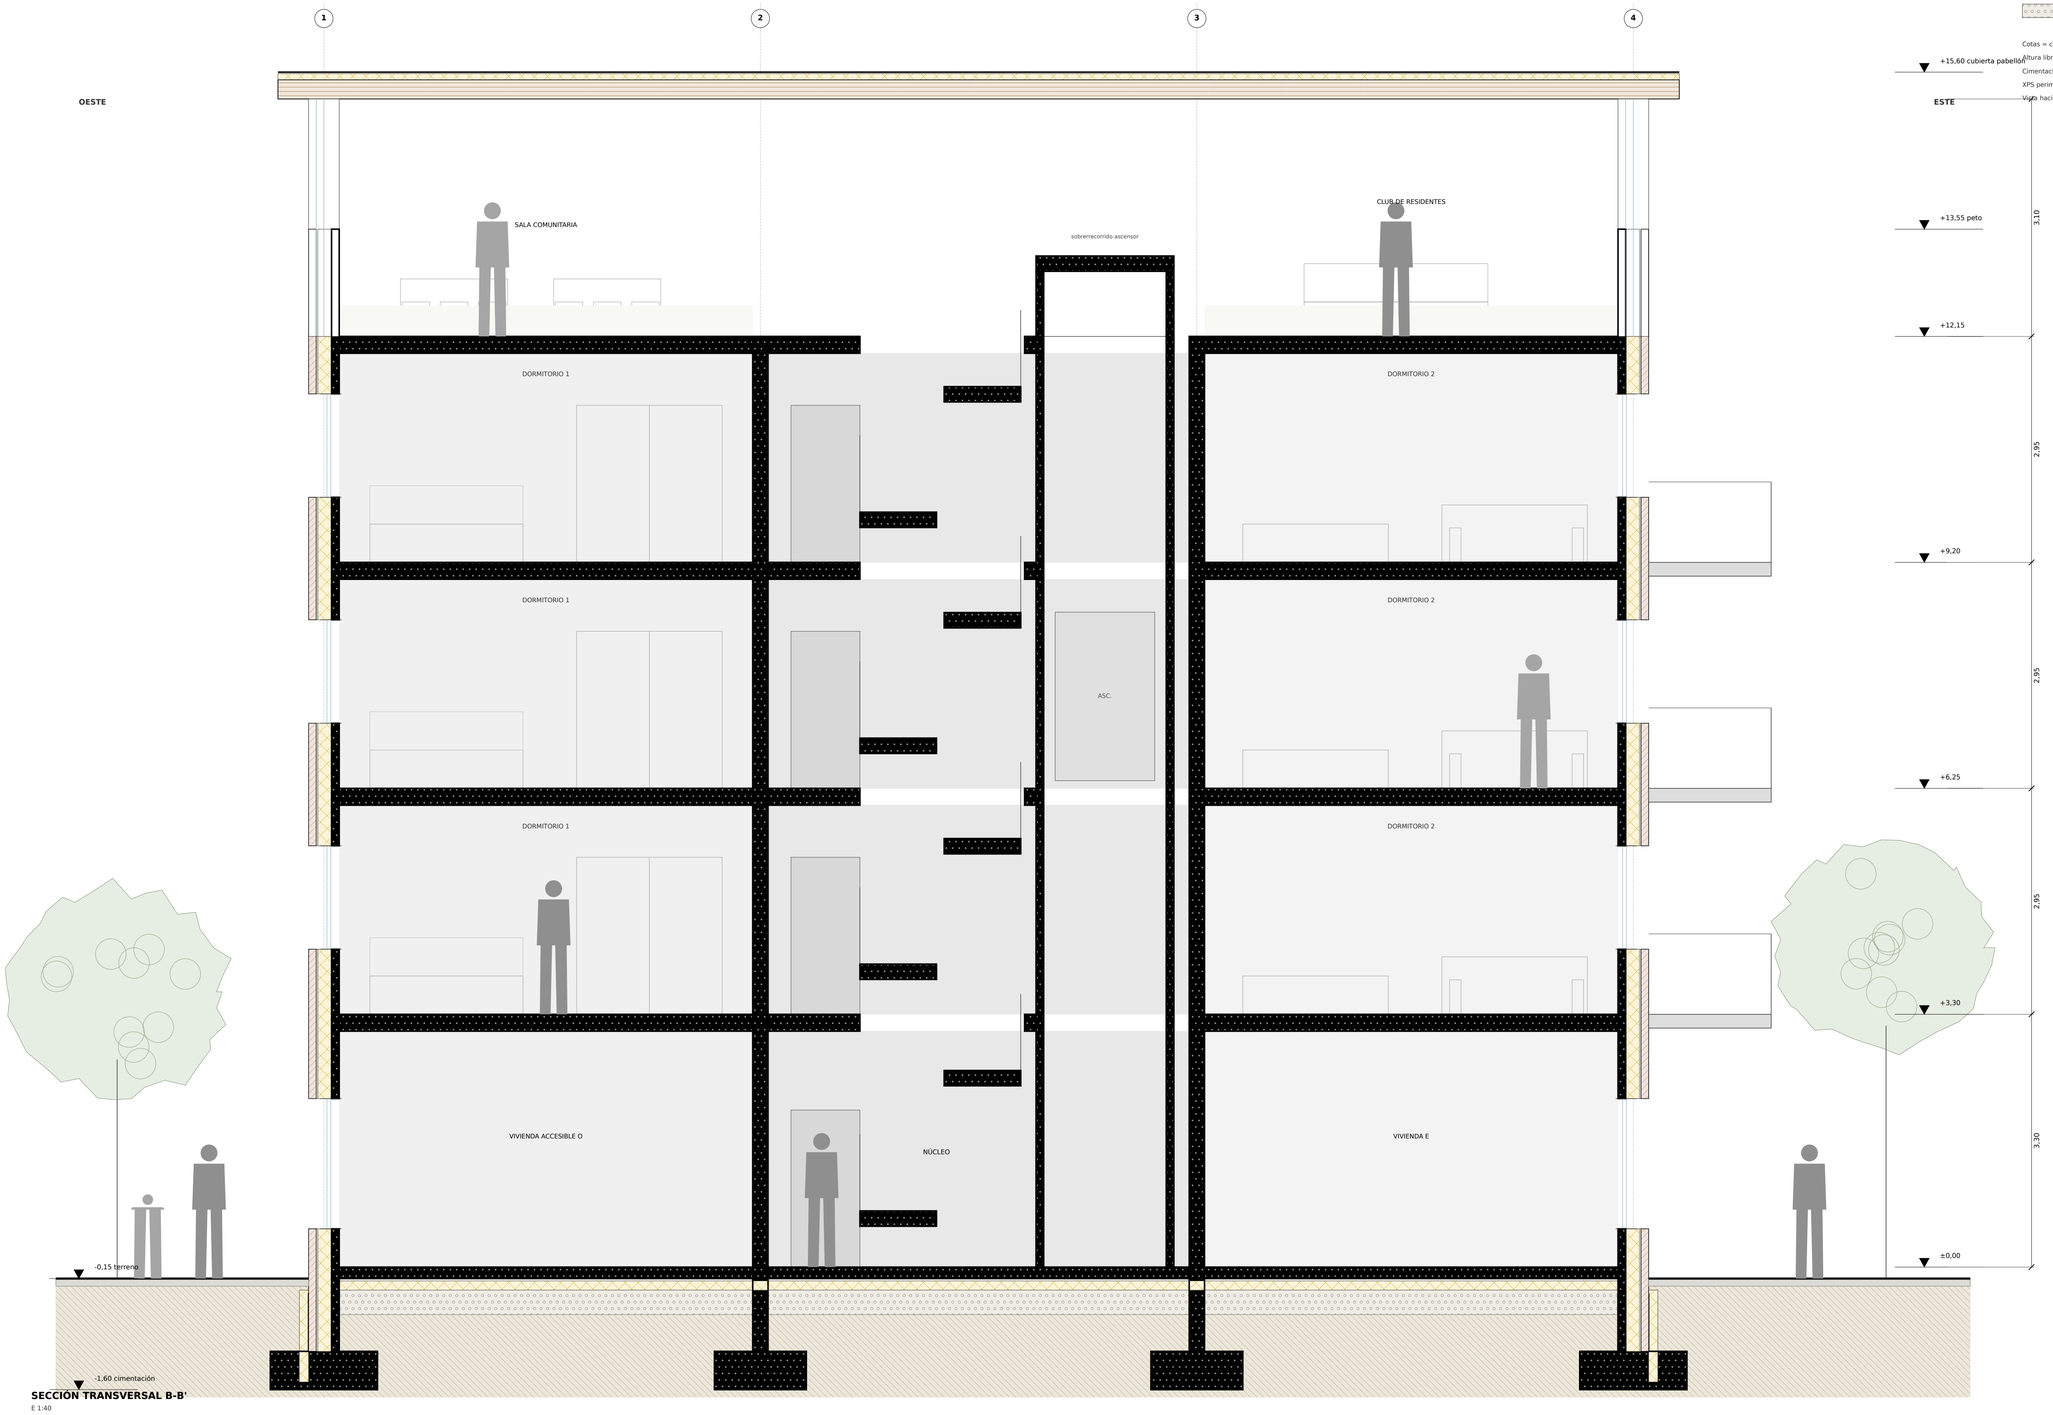


TRAMAS DE MATERIAL

- Hormigón armado
- Fábrica de ladrillo caravista
- Aislante térmico
- Madera (CLT / carpintería)
- Terreno natural
- Grava / relleno

Cotas = cara superior del forjado estructural.
Altura libre de vivienda 2,66 m; ático 2,70 m.
Cimentación a -1,60 m, bajo la helada (Dfb).
XPS perimetral 12 cm en cimentación y solera.
Vista hacia el norte desde y = 7,80 m.

SECCIÓN TRANSVERSAL B-B'

E 1:40

CASO_007 · PROPUESTA C

Anteproyecto · vivienda colectiva en propiedad, tres edificios

Dibujo: proyectista C

Sección transversal b-b'

Escala 1:40

Lámina S02