
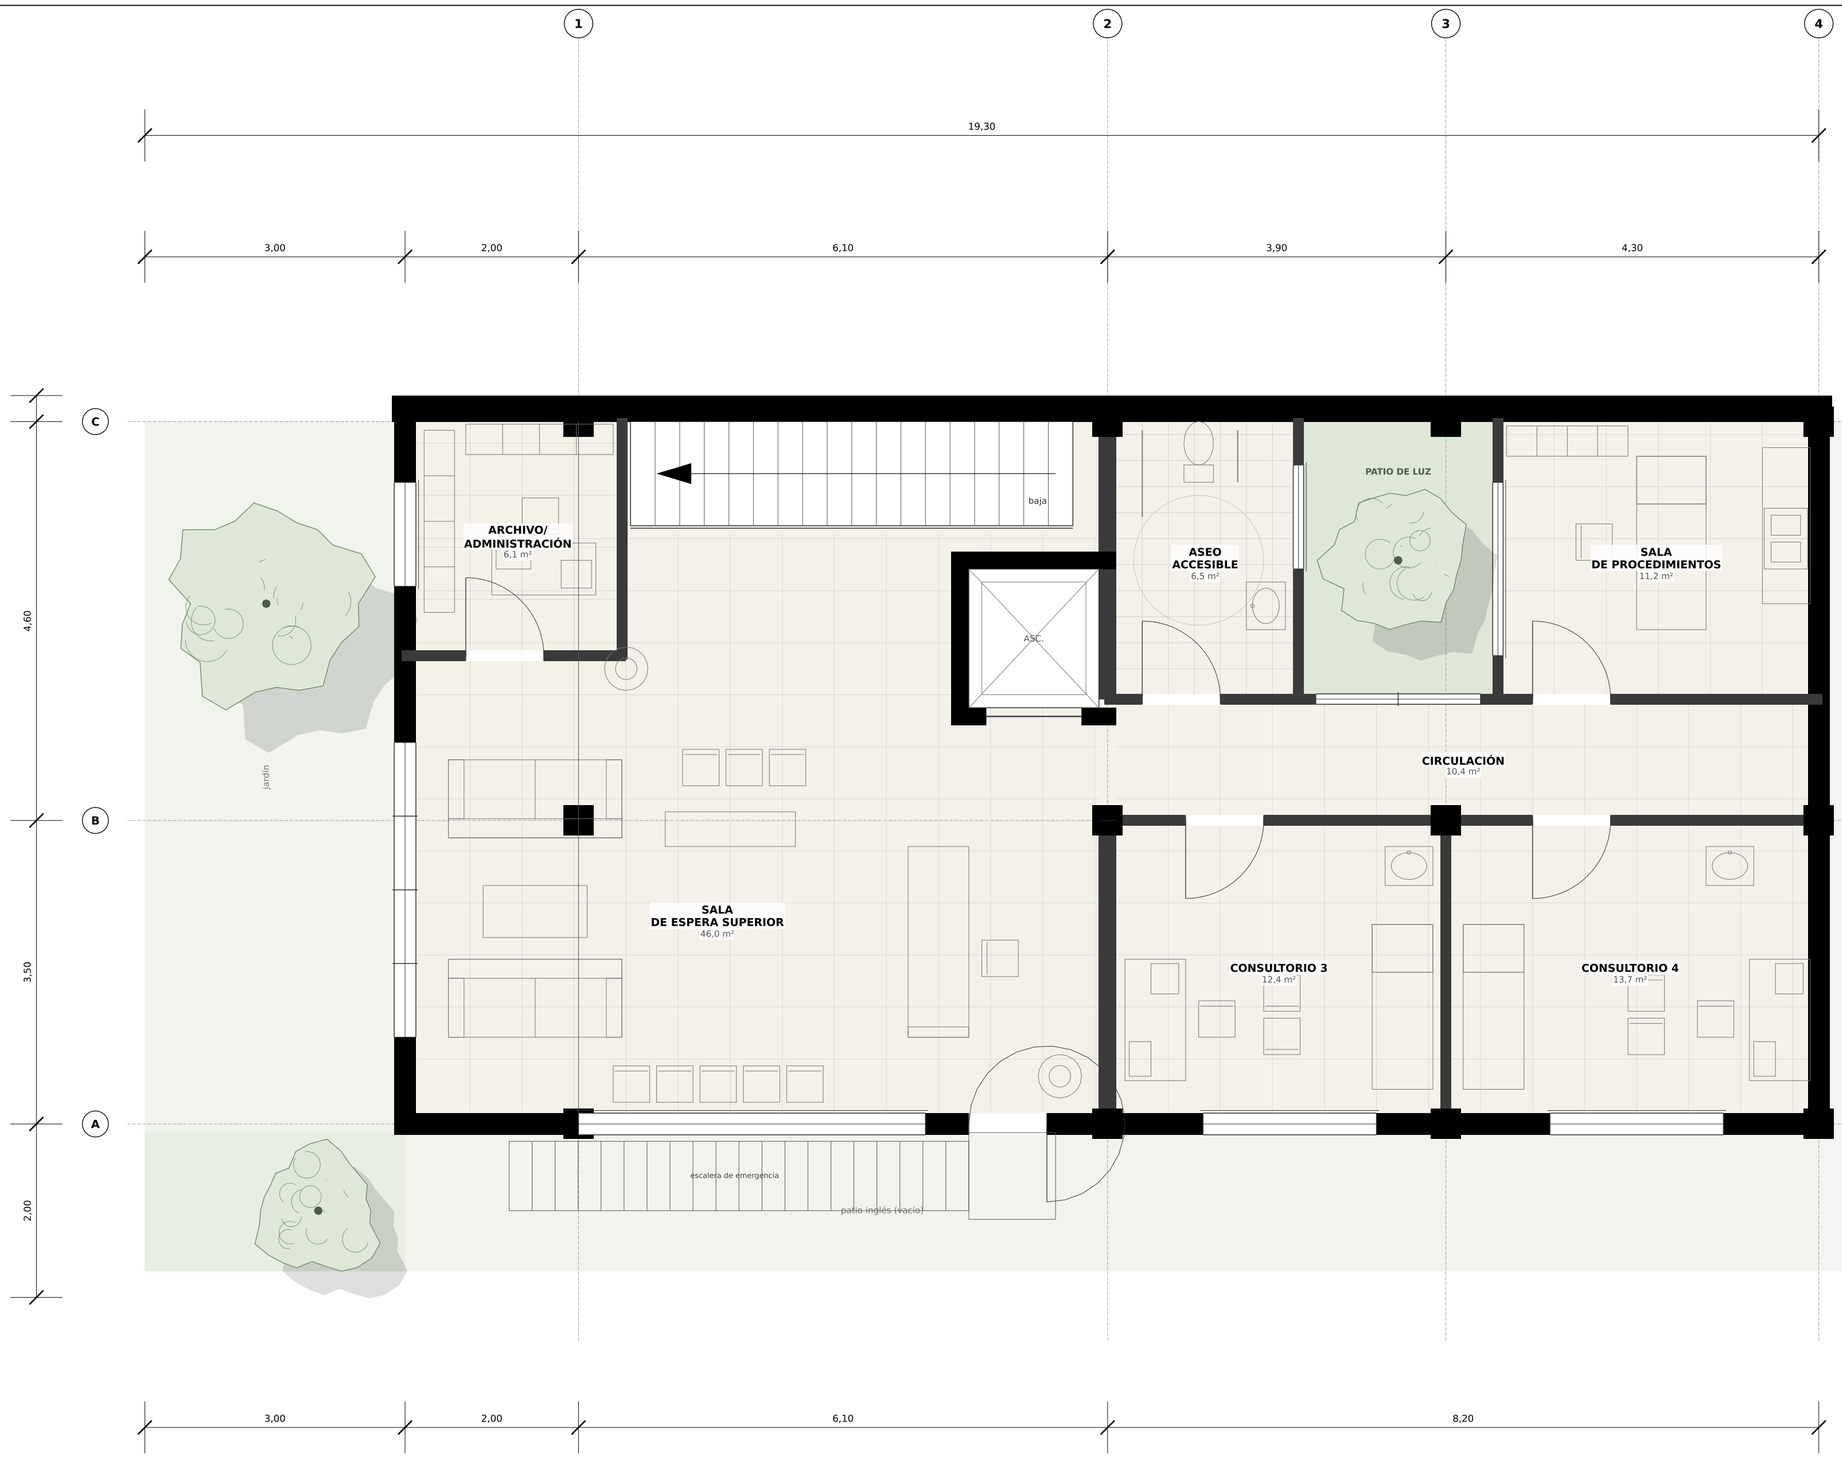


CUADRO DE SUPERFICIES ÚTILES (m²)


CLÍNICA · PLANTA PRIMERA

Sala de espera superior	46,0
Archivo/administración	6,1
Escalera	6,1
Ascensor	2,4
Consultorio 3	12,4
Consultorio 4	13,7
Circulación	10,4
Aseo accesible	6,5
Patio de luz (descubierto)	6,9
Sala de procedimientos	11,2
Superficie útil	**114,8**

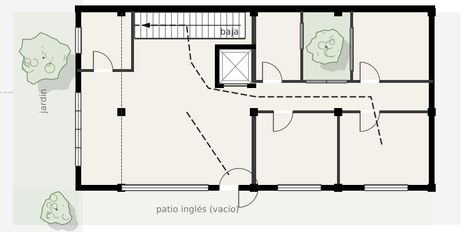

ESQUEMA DE EVACUACIÓN

Escalera principal y escalera exterior de emergencia (abierta). Recorrido < 25 m.

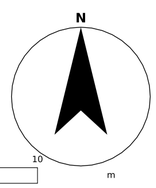



PLANTA PRIMERA

E 1:50

CASO_008 · PROPUESTA A Anteproyecto · Clínica ambulatoria y vivienda	Escala **1:50**	
PLANTA PRIMERA · CLÍNICA	Lámina **P02**	Anteproyecto