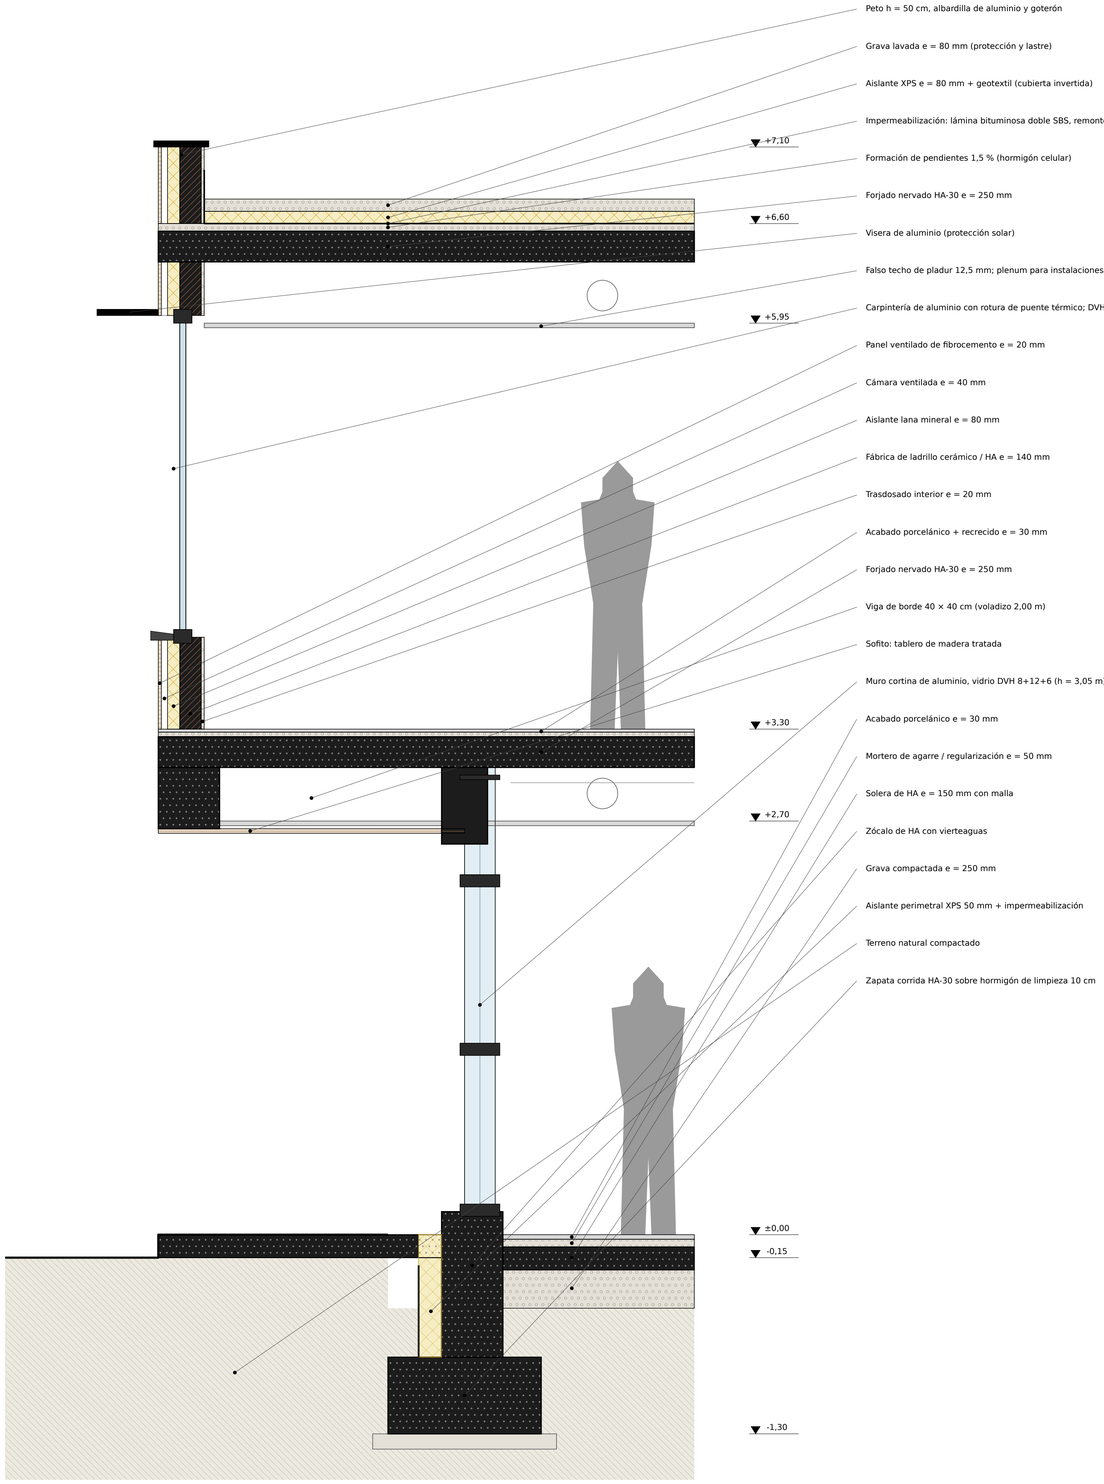


Sección por la ventana de la caja de consultorios (planta primera), por el muro cortina de la planta baja retranqueada y por el voladizo.

DETALLE CONSTRUCTIVO DE FACHADA: CIMENTACIÓN A CUBIERTA

E 1:20

CASO_008 · PROPUESTA B	DETALLE CONSTRUCTIVO DE FACHADA
Anteproyecto · Clínica ambulatoria y vivienda	Escala 1:20 · Lámina D01