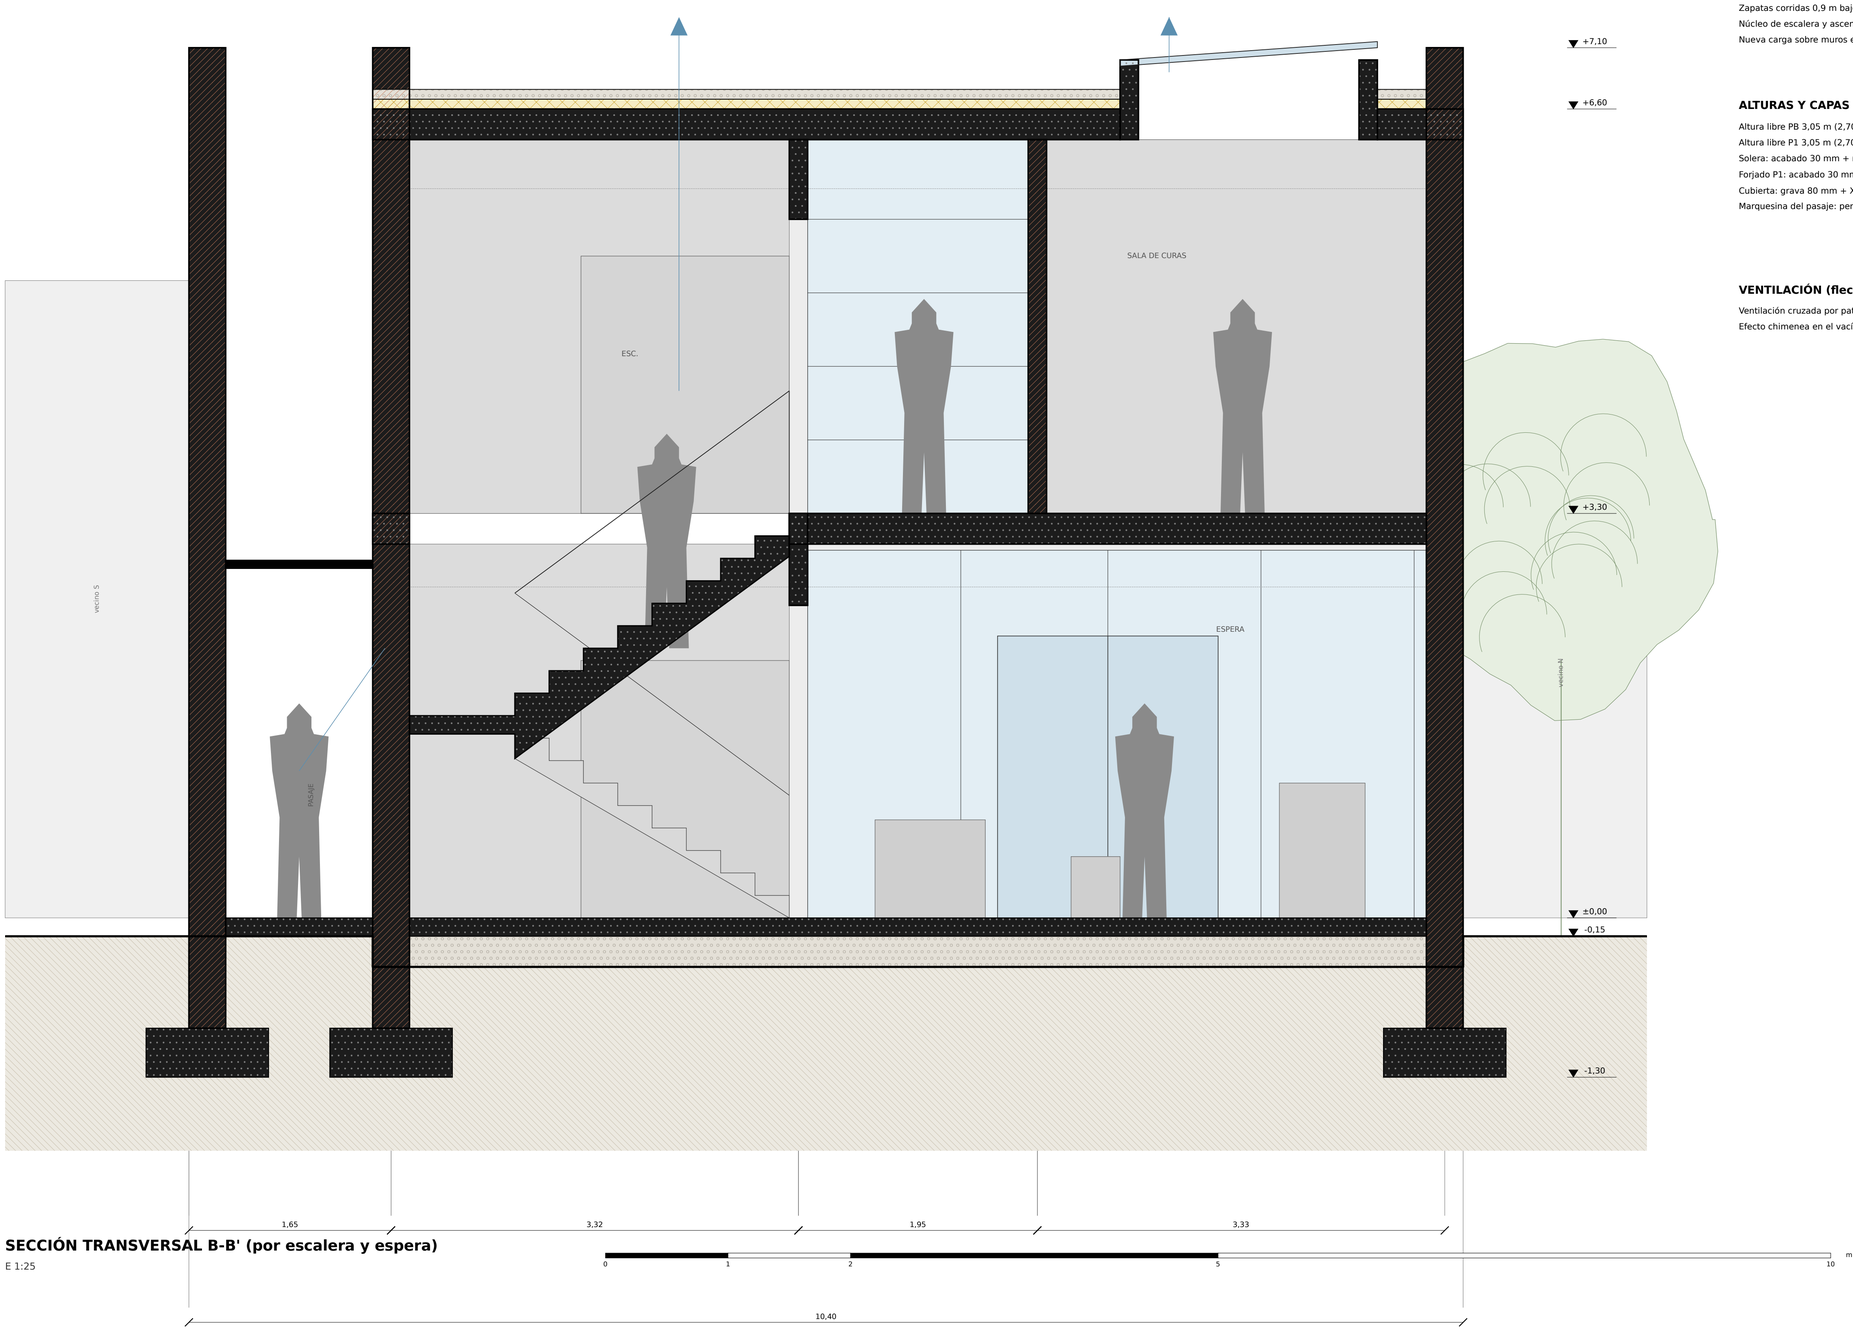


PREDIMENSIONADO ESTRUCTURAL

Retícula: ejes 1-7 cada 4,00-5,00 m; ejes A-D (muros A y D, corredor B-C).
Luces: 3,33 m entre muros (transversal); 4,00-5,00 m longitudinal.
Forjado P1 y cubierta: losa nervada h = 25 cm (L/17 en voladizo, L/20 en vano).
Voladizo de 2,00 m: viga de borde 40 × 40 cm y contrapeso por continuidad.
Pilares tipo: 30 × 30 cm HA-30 (carga ≈ 600 kN, cuantía 1,5 %).
Muros existentes de ladrillo 30 y 15 cm: se mantienen como portantes.
Zapatas corridas 0,9 m bajo muros; zapatas aisladas 1,40 × 1,40 × 0,50 m.
Núcleo de escalera y ascensor: muros de HA 15-20 cm (arriostramiento).
Nueva carga sobre muros existentes: refuerzo con recrecido de zapata.

ALTURAS Y CAPAS

Altura libre PB 3,05 m (2,70 m bajo falso techo con instalaciones).
Altura libre P1 3,05 m (2,70 m bajo falso techo).
Solera: acabado 30 mm + mortero 70 mm + HA 150 mm + grava 250 mm + terreno.
Forjado P1: acabado 30 mm + recrecido 50 mm + nervado HA 250 mm.
Cubierta: grava 80 mm + XPS 80 mm + lámina + pendiente + forjado 250 mm.
Marquesina del pasaje: perfil de acero y policarbonato alveolar, h = +2,85.

VENTILACIÓN (flechas)

Ventilación cruzada por patio clínico, lucernario con apertura y pasaje sur.
Efecto chimenea en el vacío de escalera (extracción alta).

SECCIÓN TRANSVERSAL B-B' (por escalera y espera)

E 1:25

1,65 | 3,32 | 1,95 | 3,33

10,40

0 1 2 5 10 m

CASO_008 · PROPUESTA B	SECCIÓN TRANSVERSAL B-B'
Anteproyecto · Clínica ambulatoria y vivienda	Escala 1:25 · Lámina S02