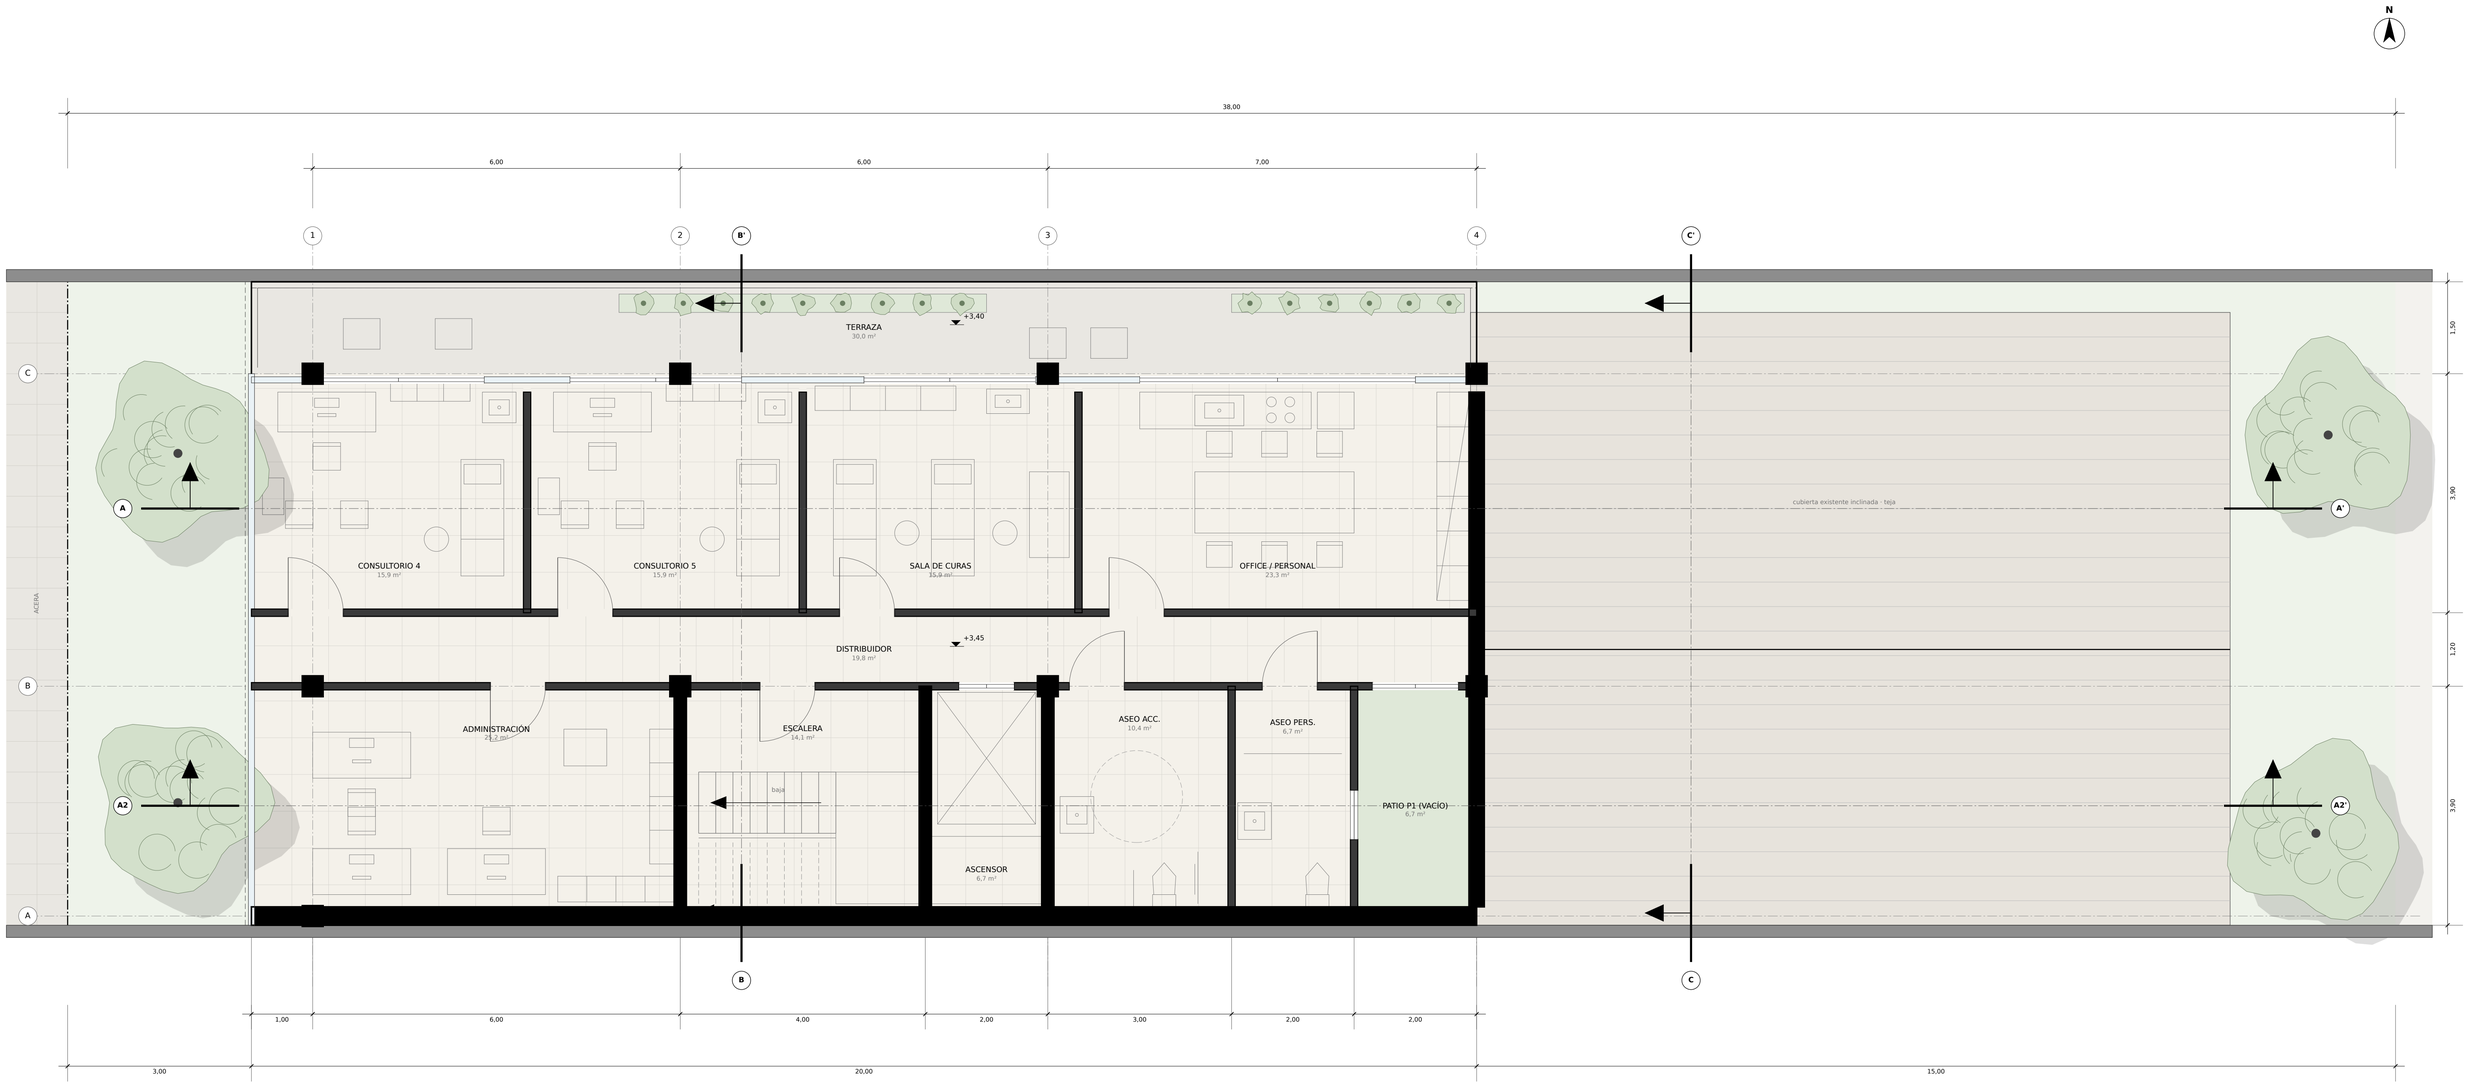


PLANTA PRIMERA · +3,45

E 1:50

0 1 2 5 10 m

ESQUEMA DE USOS, ACCESIBILIDAD Y EVACUACIÓN

E 1:100



CUADRO DE SUPERFICIES ÚTILES · PLANTA PRIMERA

Estancia	Uso	m² útiles
21 ADMINISTRACIÓN	Clínica	25,2
22 DISTRIBUIDOR	Clínica	19,8
23 CONSULTORIO 4	Clínica	15,9
24 CONSULTORIO 5	Clínica	15,9
25 SALA DE CURAS	Clínica	15,9
26 OFFICE / PERSONAL	Clínica	23,3
27 ESCALERA	Común / núcleo	14,1
28 ASCENSOR	Común / núcleo	6,7
29 ASEO ACC.	Clínica	10,4
30 ASEO PERS.	Clínica	6,7
31 PATIO P1 (VACÍO)	Común / núcleo	6,7
32 TERRAZA	Terraza (no computa)	30,0
Total útil clínica		**133,0**
Total útil núcleo común		**20,7**

CASO_008 · PROPUESTA C

Planta primera

Anteproyecto

Escala: **E 1:50 / 1:100**

Lámina: **P02**