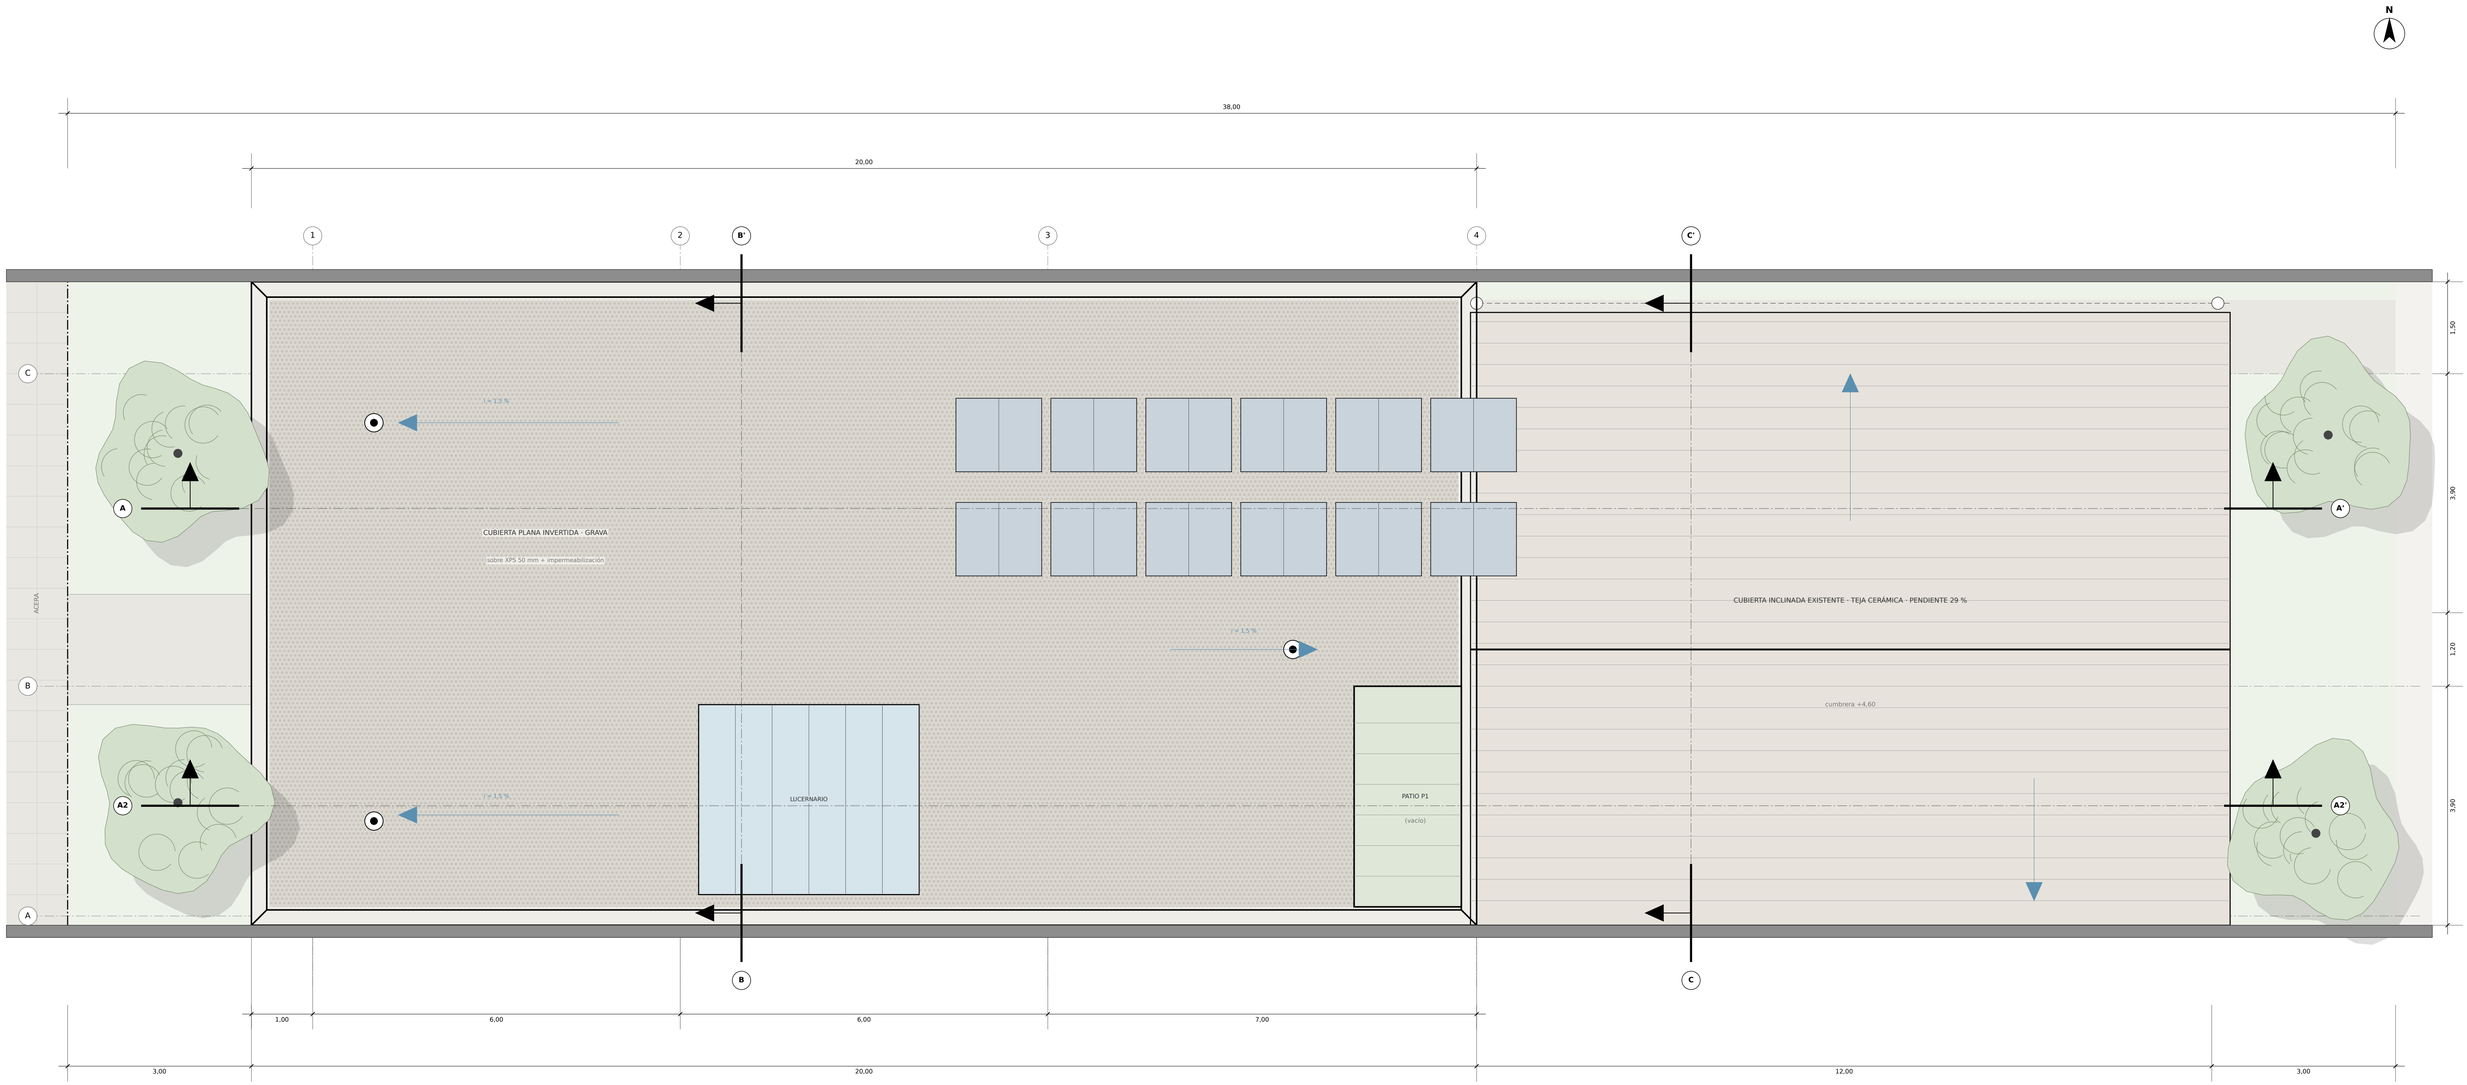


PLANTA DE CUBIERTAS · +6,65 / +4,60

E 1:50

0 1 2 5 10 m

LEYENDA Y CRITERIOS DE CUBIERTA

1. Cubierta plana invertida (clínica): losa 20 cm, mortero de pendientes 4 cm, lámina impermeabilizante, XPS 5 cm, geotextil y grava 7 cm.
2. Pendiente del 1,5 % hacia 3 sumideros de 110 mm con rebosadero; peto perimetral +7,05 con albardilla de hormigón y goterón.
3. Lucernario sobre la escalera (iluminación cenital y extracción de aire caliente por efecto chimenea, con huecos practicables en alto).
4. Patio P1: vacío en toda la altura, que da luz y ventilación cruzada a aseos y distribuidor; rejilla y sumidero en el fondo.
5. Campo solar: 12 módulos fotovoltaicos (≈ 5,5 kWp) y 2 captadores térmicos para ACS, orientados al norte (hemisferio sur), inclinación 20°.
6. Cubierta de la vivienda (existente, tramo de mayor altura): se conserva, con teja cerámica y alero de 1,10 m al norte; se refuerzan canalón y ventilación del desván.
7. Recogida de pluviales hacia aljibe de 6 m³ en el jardín trasero (riego y lavado), con aliviadero a la red.

CASO_008 · PROPUESTA C

Planta de cubiertas

Anteproyecto

Escala
E 1:50

Lámina
P03