

F1 CIMENTACIÓN, SOLERA Y ARRANQUE DE FACHADA

Sección vertical · E 1:20

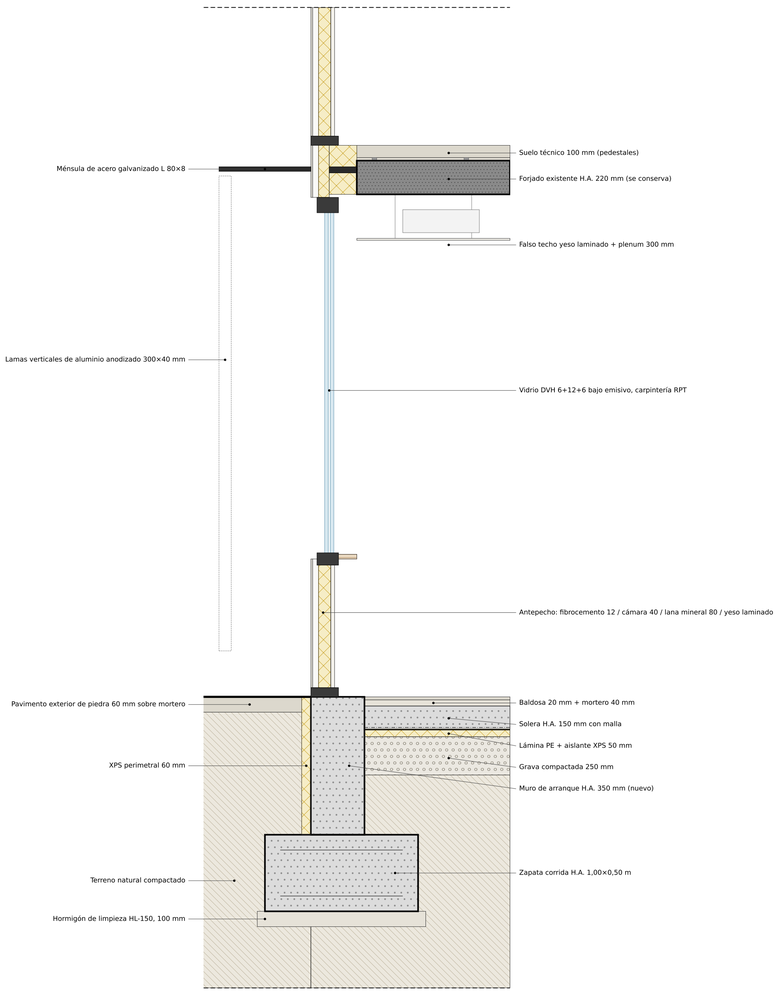


F2 FORJADO TIPO Y MURO CORTINA CON LAMAS

Sección vertical · E 1:20

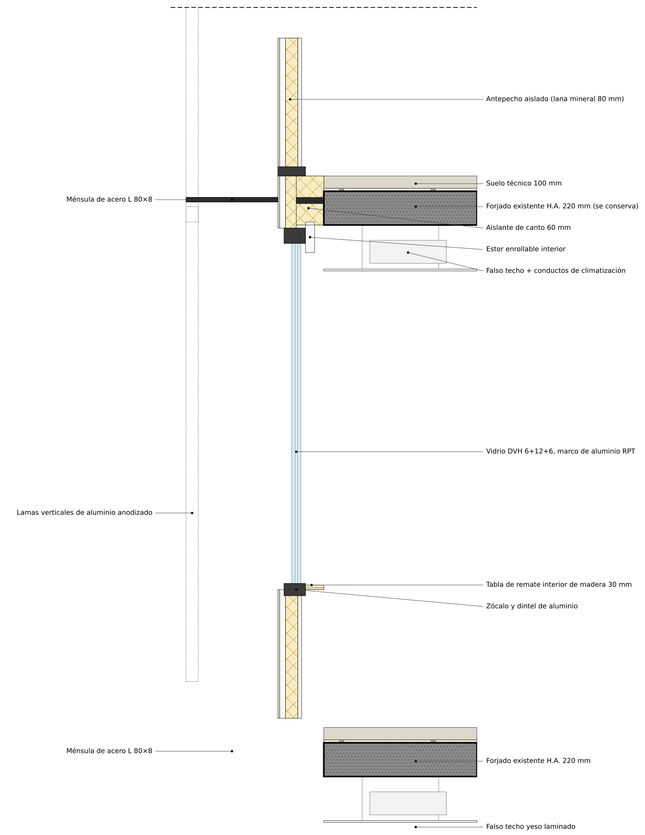

F3 COTA TERRAZA +10,80: CUBIERTA INVERTIDA, PETO Y BARANDILLA

Sección vertical · E 1:20

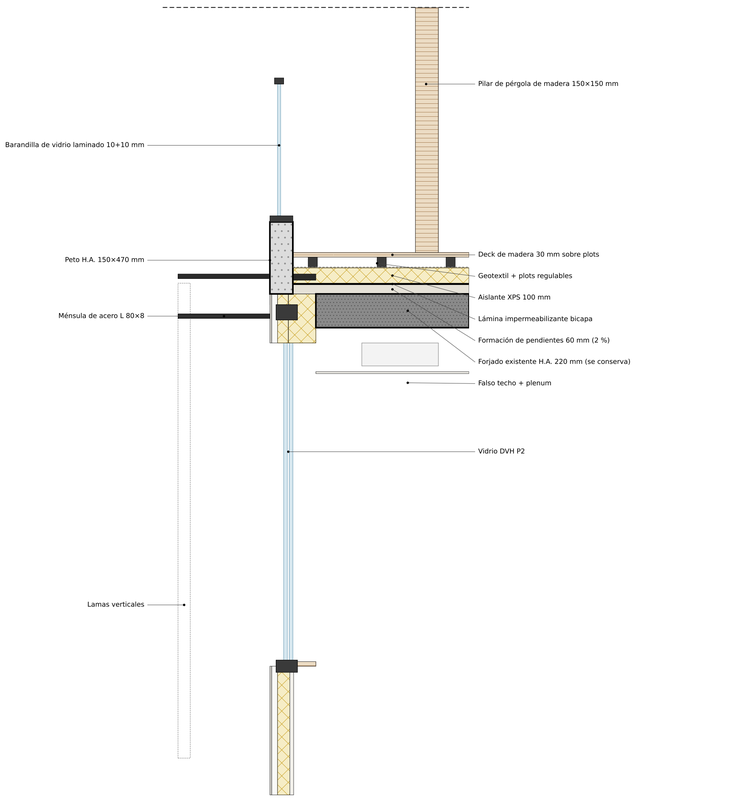

CUADRO DE CAPAS Y SISTEMAS (de exterior a interior / de arriba a abajo)

SOLERA PB: baldosa porcelánica 20 mm · mortero 40 mm · solera H.A. 150 mm con malla · lámina PE · aislante XPS 50 mm · grava compactada 250 mm · terreno natural.

CIMENTACIÓN: zapata corrida H.A. 100×50 cm sobre limpieza 10 cm; muro de arranque 35 cm. Aislamiento perimetral XPS 60 mm hasta la zapata.

FACHADA OPACA (antepecho): fibrocemento 12 mm · cámara ventilada 40 mm · lana mineral 80 mm entre montantes · doble placa de yeso laminado 2×12,5 mm.

MURO CORTINA: perfilería de aluminio con rotura de puente térmico, vidrio DVH 6+12+6 bajo emisivo (U ≈ 1,4 W/m²K), factor solar g ≤ 0,40.

FORJADO TIPO (existente, se conserva): losa/vigueta H.A. 220 mm; suelo técnico 100 mm; falso techo de yeso laminado a 3,00 m con plenum de 300 mm para instalaciones.

LAMAS: aluminio anodizado 300×40 mm cada 600 mm, separadas 600 mm de la fachada, sobre ménsulas de acero galvanizado ancladas al canto del forjado.

CUBIERTA INVERTIDA TRANSITABLE (terraza): deck de madera 30 mm sobre plots · geotextil · XPS 100 mm · lámina bicapa · formación de pendientes 60 mm (2 %) · forjado existente 220 mm. Peto H.A. 150 mm con remate de aluminio y barandilla de vidrio laminado 10+10 mm de 1,10 m.

CUBIERTA VERDE (cuerpo posterior): sustrato 80 mm · drenaje · XPS 100 mm · lámina · pendientes · forjado (ver P05).

Leyenda de tramas: Hormigón existente (se conserva) · Hormigón nuevo · Aislante térmico · Madera · Terreno natural · Grava · Vidrio

CASO_009 · PROPUESTA A

Detalle constructivo de fachada y cubierta

Anteproyecto · Renovación integral de edificio de oficinas

Lámina **D01**

Escala **1:20** · Anteproyecto