

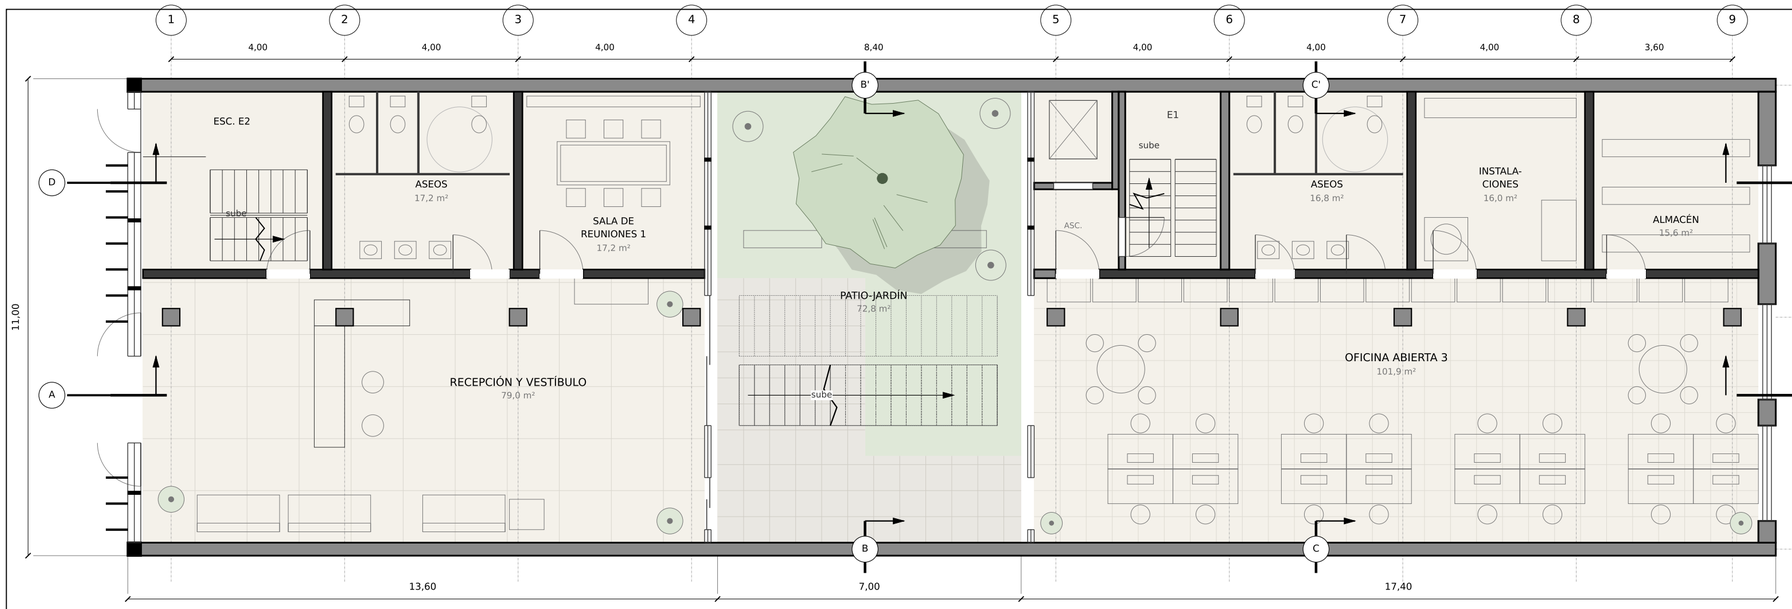


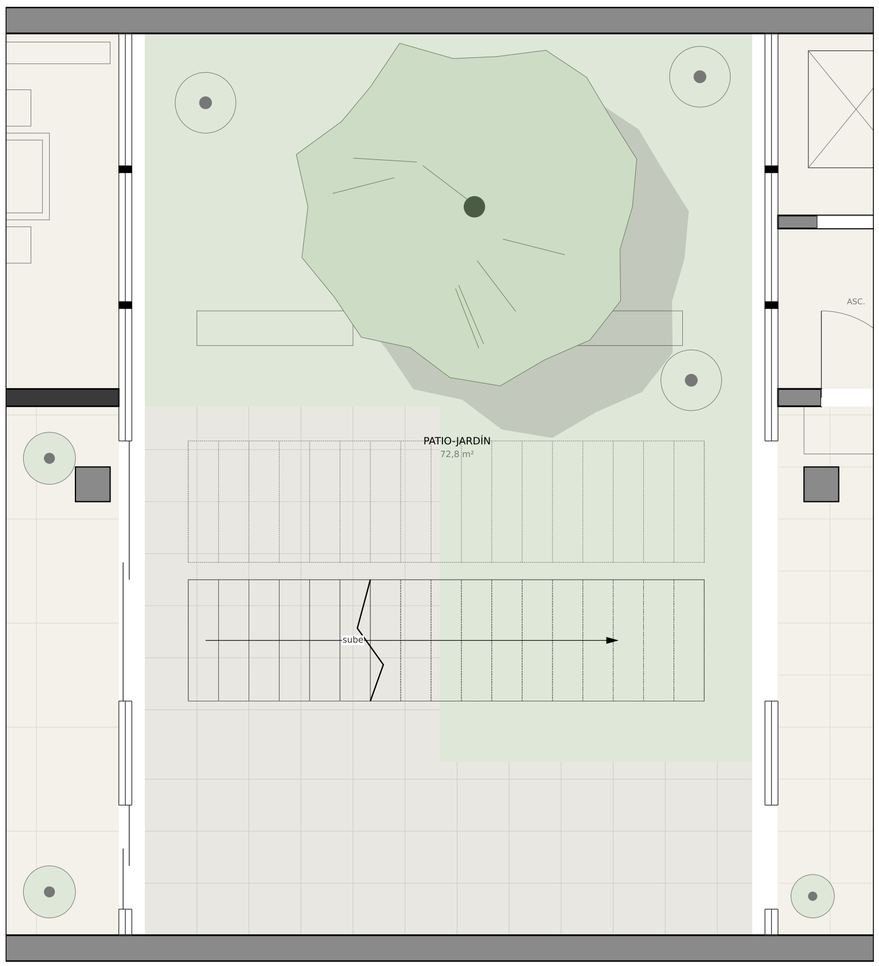

AMPLIACIÓN PATIO-JARDÍN Y ESCALERA
E 1:50

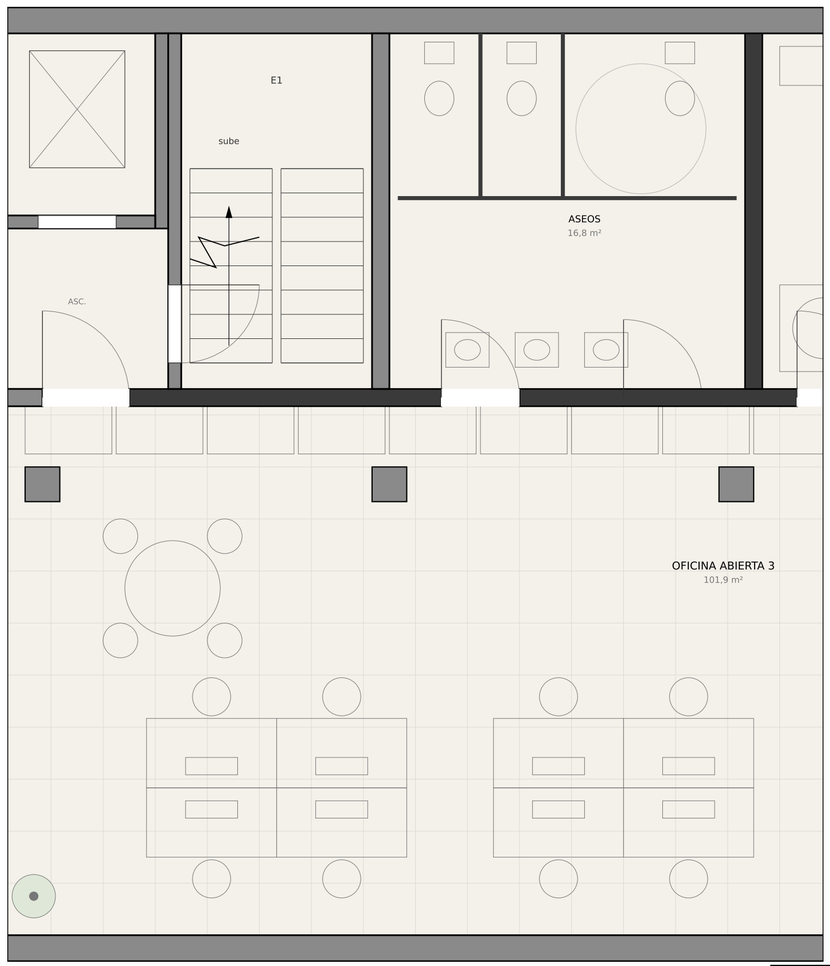

AMPLIACIÓN NÚCLEO Y ASEOS
E 1:50

N

0 1 2 5 10 m

PLANTA BAJA +0,00

E 1:100

Fachada a la calle al norte (izquierda).

LEYENDA

- Muro existente que se conserva
- Obra nueva (muro / fachada / forjado)
- Tabique nuevo
- Existente a demoler (contorno)
- Carpintería / muro cortina

Nivel de corte de planta: +1,20 m sobre el suelo terminado.

CUADRO DE SUPERFICIES ÚTILES (aprox.)

ASEOS 1	17,2 m²
RECEPCIÓN Y VESTÍBULO	79,0 m²
SALA DE REUNIONES 1	17,2 m²
NÚCLEO E1 + ASCENSOR	17,6 m²
ASEOS 2	16,8 m²
OFICINA ABIERTA 3	101,9 m²
INSTALA- CIONES	16,0 m²
ALMACÉN	15,6 m²
PATIO-JARDÍN (exterior)	72,8 m²
Superficie útil interior del nivel	**281,3 m²**

CASO_009 · PROPUESTA A

Planta baja

Anteproyecto · Renovación integral de edificio de oficinas

Lámina
P01

Escala
1:100

Anteproyecto