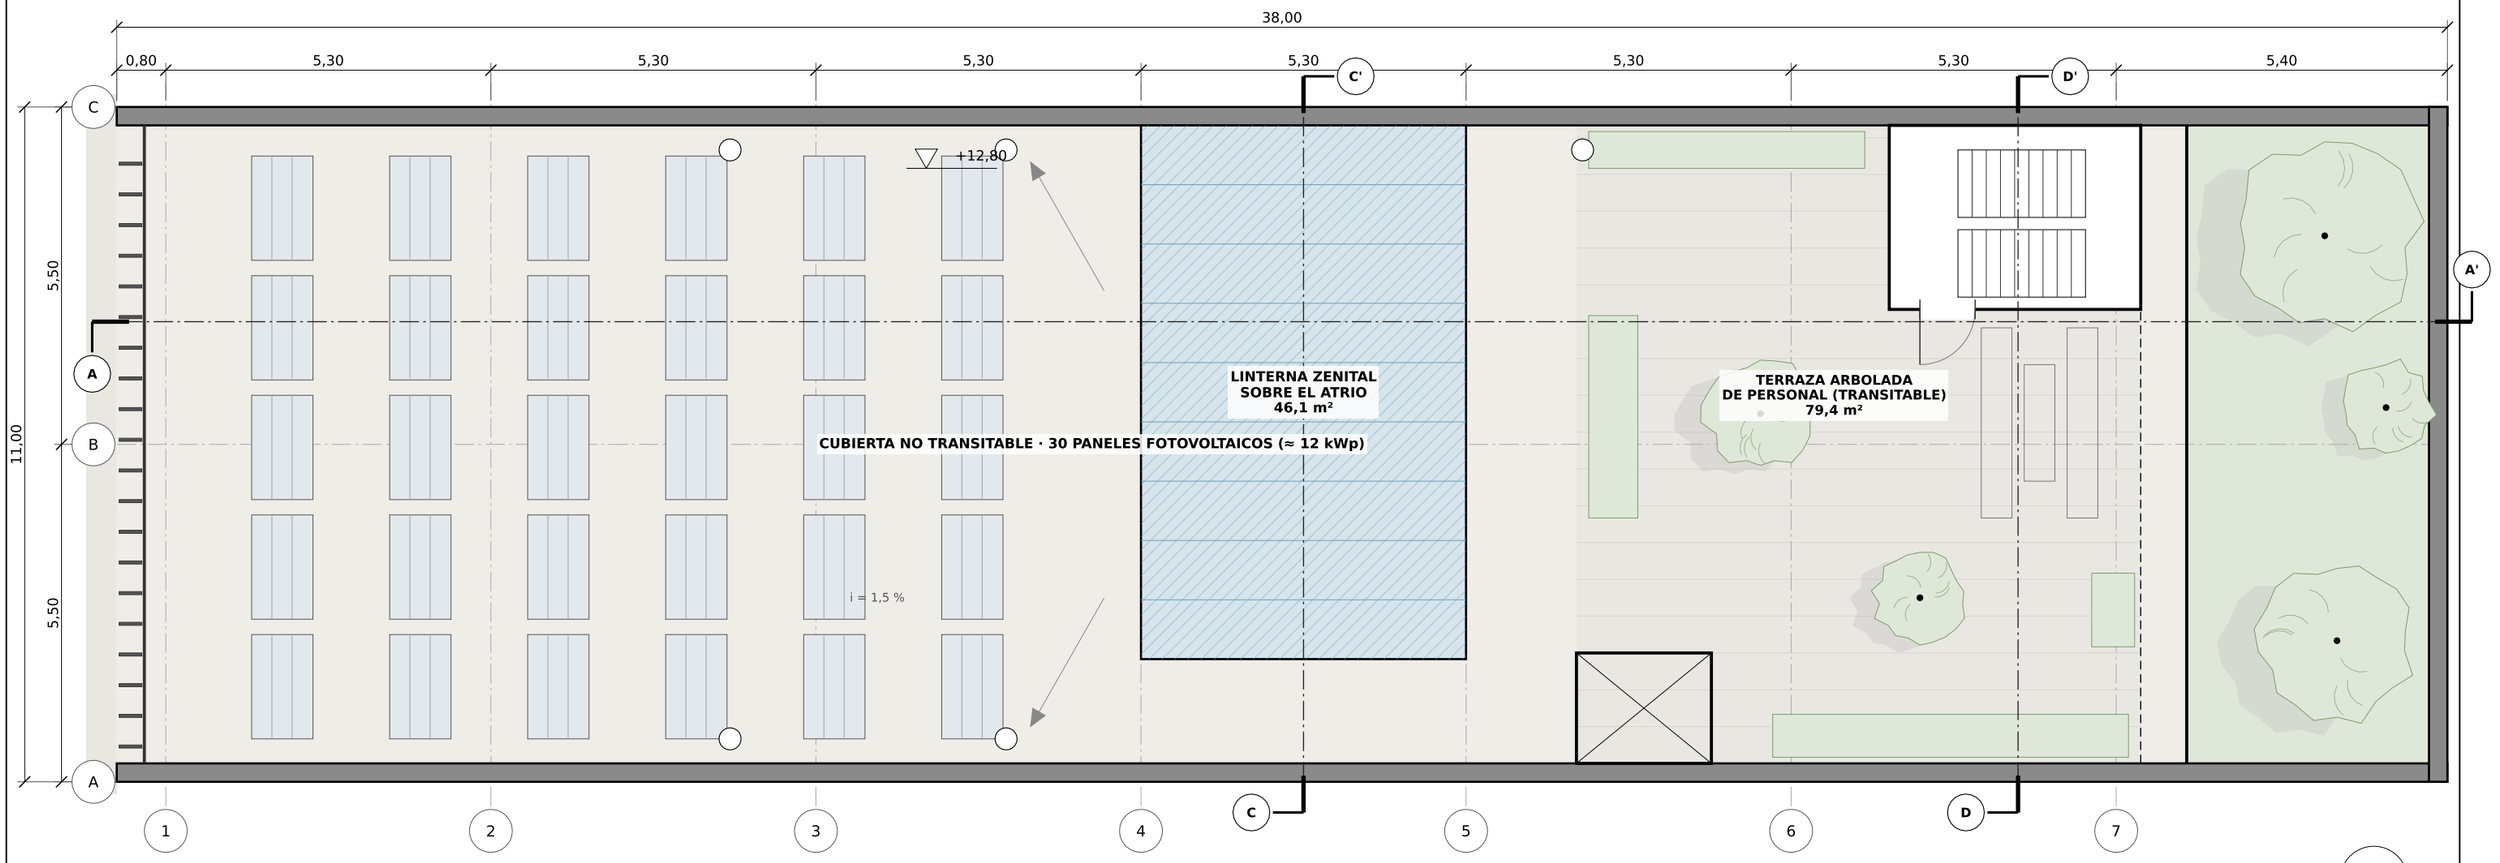


PLANTA DE CUBIERTAS

E 1:100

0 1 2 5 10 m

ELEMENTOS DE CUBIERTA

Cubierta plana invertida: forjado 30 cm, formación de pendientes, lámina impermeable, aislante XPS 14 cm, geotextil y grava 5 cm (zonas técnicas) / pavimento flotante (terraza).

Linterna zenital con lamas orientables: ventilación cruzada y extracción de aire caliente del atrio.

Casetón de escalera 2 y sobre-recorrido del ascensor: únicos elementos que superan el peto.

Medianeras existentes conservadas y rematadas con albardilla; peto frontal = lamas verticales.

Recogida de pluviales: 5 sumideros con rebosadero y bajantes por el interior de los núcleos.

CUADRO DE SUPERFICIES DE CUBIERTA

Cubierta no transitable con paneles fotovoltaicos (zona frontal)	≈ 190,0 m²
Linterna zenital sobre el atrio	46,1 m²
Terraza arbolada de personal (transitable)	79,4 m²
Casetón de escalera 2 y sobre-recorrido del ascensor	16,3 m²
Superficie de cubierta total (en proyección)	**≈ 345 m²**

LEYENDA

- Existente que se conserva (medianeras, pilares y forjados)
- Obra nueva: muros de hormigón de núcleos y escaleras
- Tabique nuevo / vidrio de salas (línea fina doble)
- Existente que se demuele (trazo discontinuo)
- Itinerario accesible (ascensor y plano a nivel)
- Recorrido de evacuación hacia escalera protegida

CASO_009 · PROPUESTA B — Anteproyecto

Planta de cubiertas

Escala 1:100
Medidas en metros

Lámina P05