


SECCIÓN TRANSVERSAL C-C'

E 1:50 · por el atrio y la escalera

0 1 2 5 10 m

Se mira hacia el norte (C-C' a través del atrio; D-D' hacia el jardín posterior).

Hormigón existente en gris; hormigón y forjados nuevos en negro; trama de grava y aislante en cubierta; terreno con rayado.

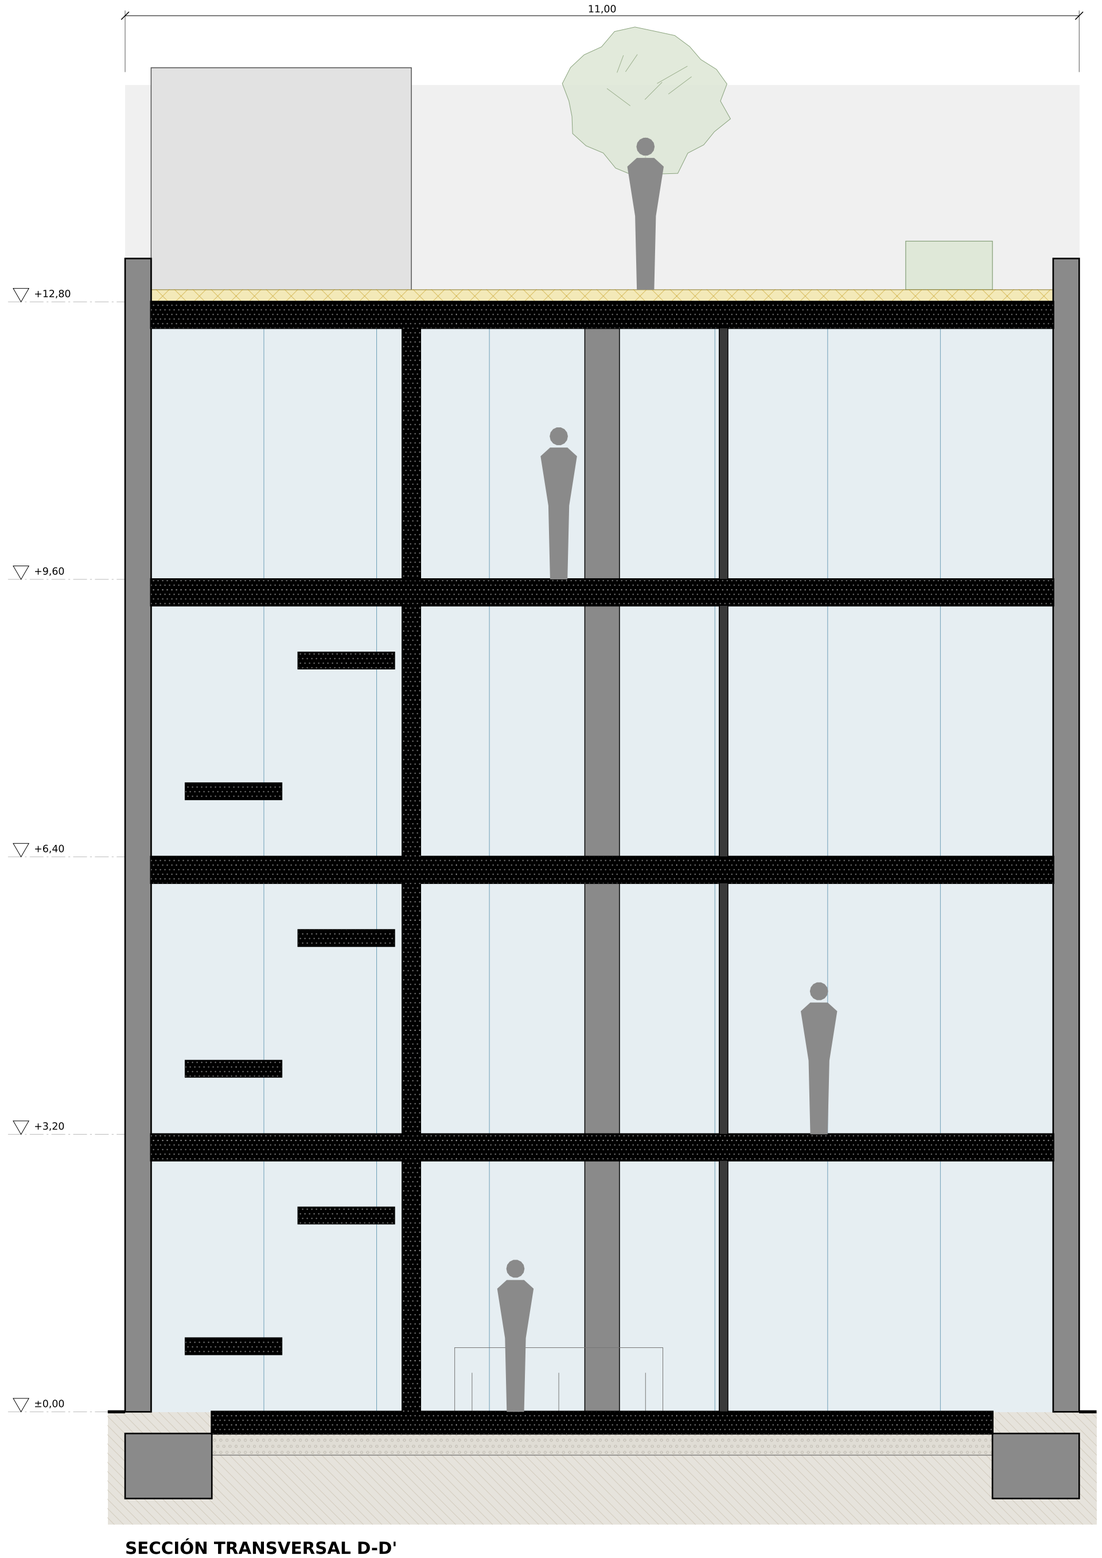

SECCIÓN TRANSVERSAL D-D'

E 1:50 · por la zona posterior

CASO_009 · PROPUESTA B

Anteproyecto

Secciones transversales C-C' y D-D'

Escala 1:50

Cotas en metros

Lámina S02