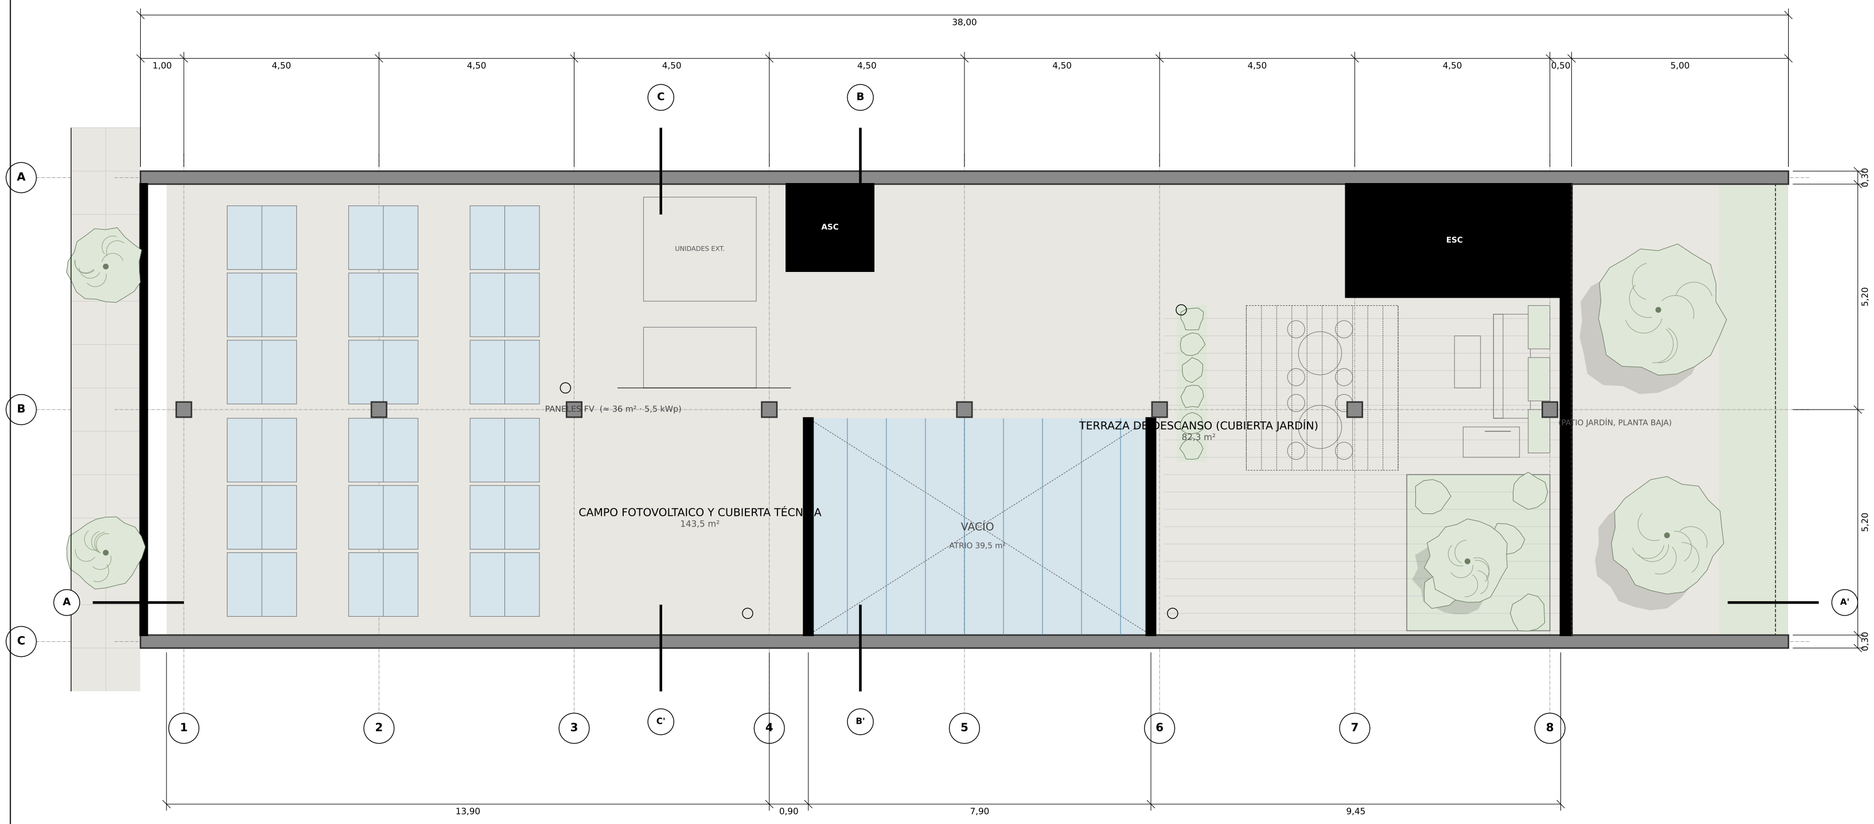


PLANTA DE CUBIERTAS

LEYENDA

- Obra nueva (muros, núcleos, fachada)
- Existente que se conserva
- Existente que se demuele
- Tabique nuevo

ESQUEMA DE EVACUACIÓN Y ACCESIBILIDAD

- Recorrido de evacuación
- Itinerario accesible (Ø 1,50 giro)

EP escalera protegida (EI 120)

ASC ascensor accesible 1,10 × 1,40

Ancho mín. de paso 1,20 m

Atrio con control de humos en lucernario


PLANTA DE CUBIERTAS

E 1:100

0 1 2 5 m

N

+14.40

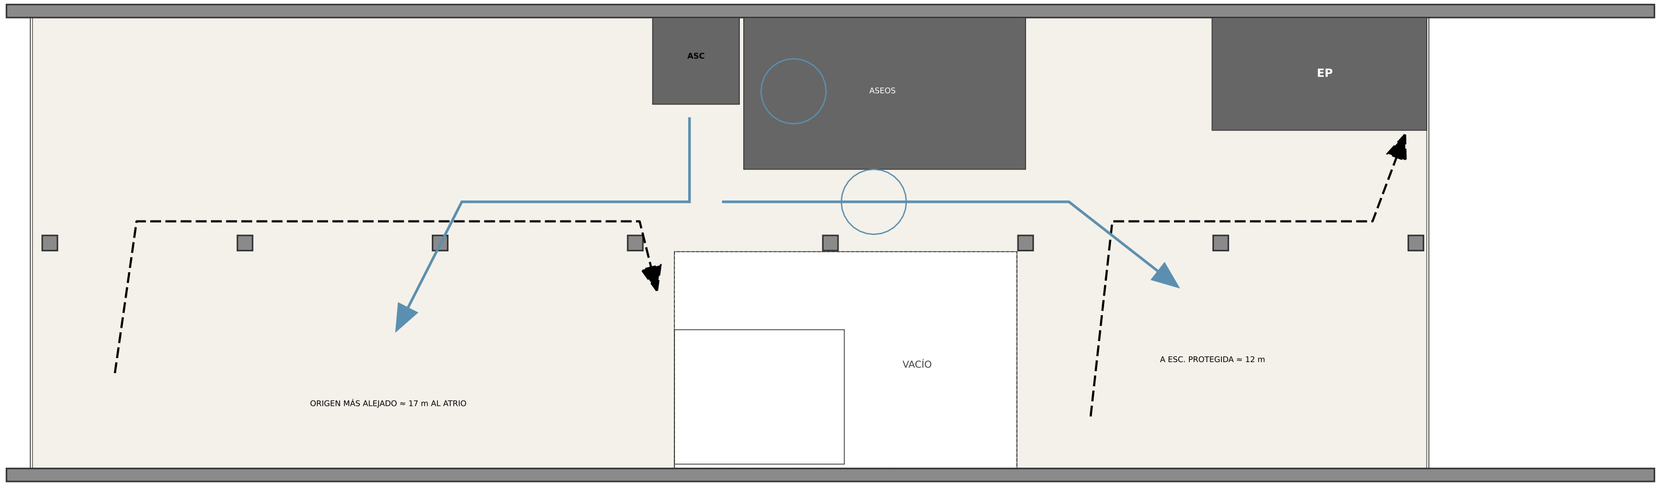

ESQUEMA DE EVACUACIÓN Y ACCESIBILIDAD — PLANTA DE CUBIERTAS

E 1:100

CUADRO DE ESTANCIAS Y SUPERFICIES ÚTILES

01	TERRAZA DE DESCANSO (CUBIERTA JARDÍN)	82,3 m²	**03**	LUCERNARIO DEL ATRIO	39,5 m²	**05**	CASETÓN ASCENSOR	2,9 m²
02	CAMPO FOTOVOLTAICO Y CUBIERTA TÉCNICA	143,5 m²	**04**	CASETÓN ESCALERA / SALIDA A CUBIERTA	11,4 m²			

CASO_009 · PROPUESTA C

Planta De Cubiertas

Renovación integral de edificio de oficinas

ESCALA

1:100

LÁMINA

P05

Anteproyecto