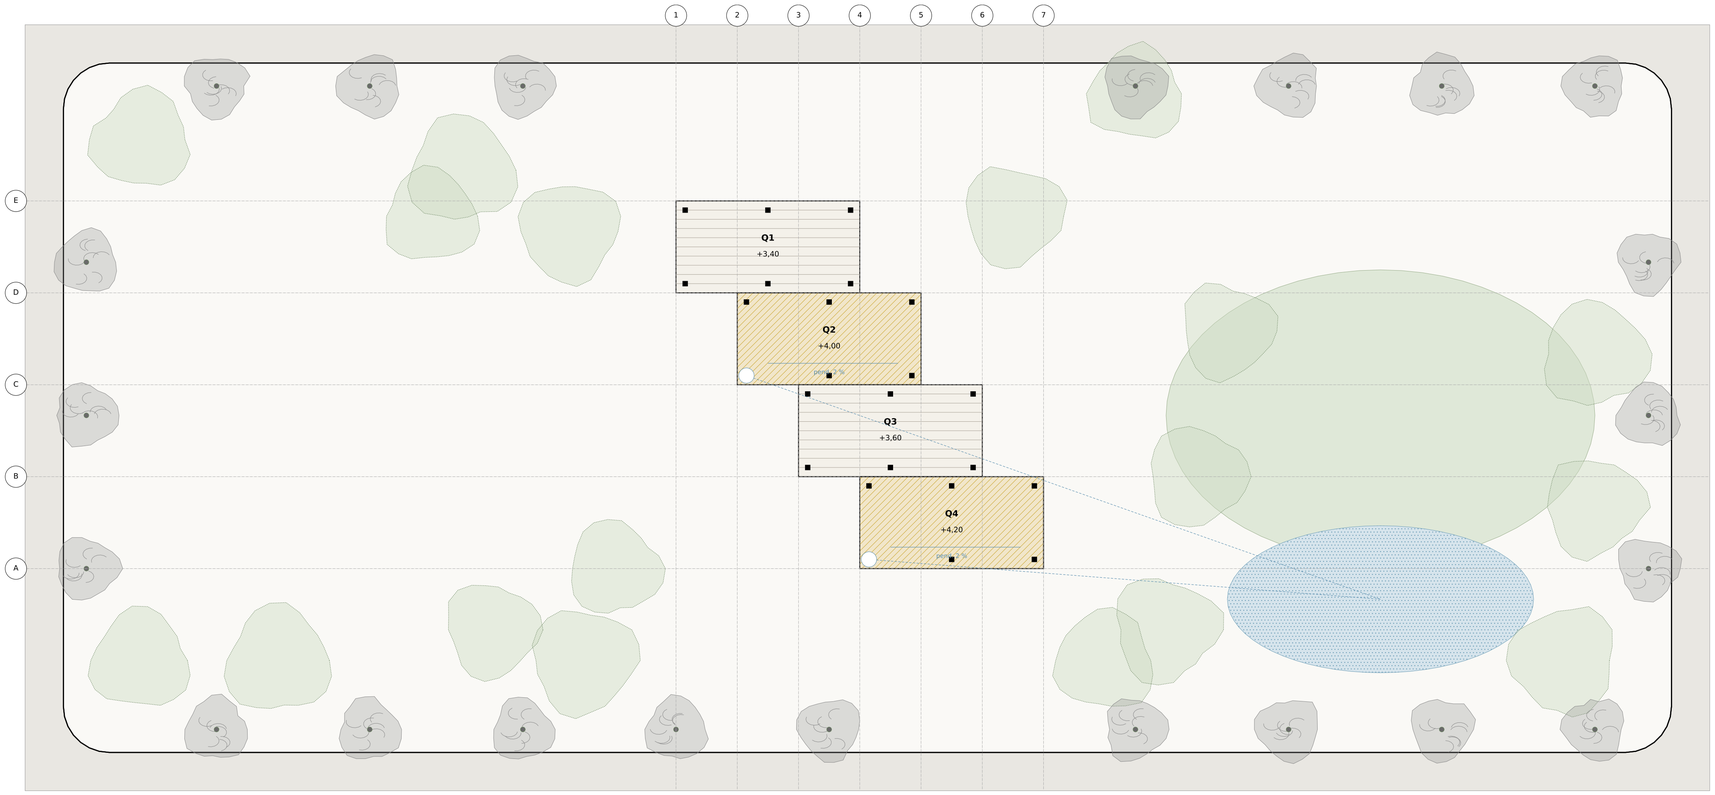


PLANTA DE CUBIERTAS · PLAZA 2

E 1:200

N

0 5 10 20 m


CUADRO DE PÉRGOLAS

Plaza · cubierta	Dim. (m)	Cota alero	Tipo
1 · A	12 x 6	+3,40	lamas de madera
1 · B	12 x 6	+4,20	panel opaco + bajante
1 · C	12 x 6	+3,80	lamas de madera
1 · D	12 x 6	+4,60	lamas de madera
1 · E	12 x 6	+3,80	panel opaco + bajante
1 · F	12 x 6	+3,40	lamas de madera
2 · Q1	12 x 6	+3,40	lamas de madera
2 · Q2	12 x 6	+4,00	panel opaco + bajante
2 · Q3	12 x 6	+3,60	lamas de madera
2 · Q4	12 x 6	+4,20	panel opaco + bajante

Cubierta de lamas: libre drenaje, sombra filtrada (~65 % de ocultación).
Cubierta con panel opaco: pendiente 2 %, bajante por el pilar hueco hacia el jardín de lluvia (retención de 30 l/m² de cubierta).
Cotas de alero sobre el pavimento terminado (+0,00).

LEYENDA

- Cubierta de lamas
- Cubierta con panel opaco
- Copa de arbolado (discontinuo)
- Jardín de lluvia

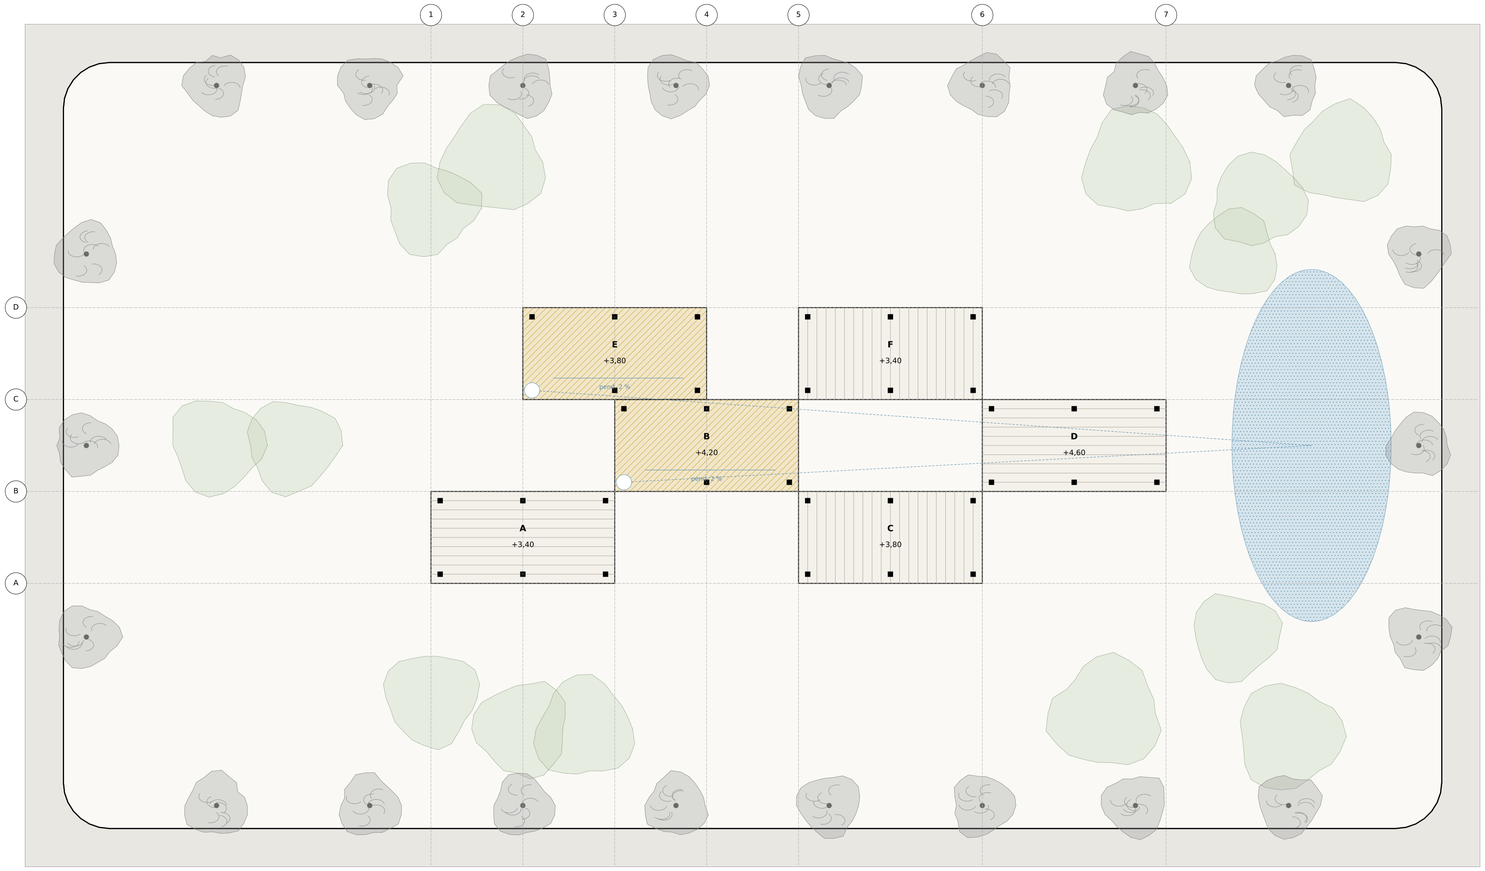

PLANTA DE CUBIERTAS · PLAZA 1

E 1:200

CASO_010 · PROPUESTA A Planta de cubiertas y pérgolas · nivel +4,60	Plano **P03**	
Anteproyecto · Dos plazas de barrio	Escala 1:200	Lámina P03