



SECCIÓN TRANSVERSAL B-B' · PLAZA 1 (calle - pérgola B - calle)

E 1:150 · corte por pilares; en proyección, pérgolas, mobiliario y arbolado más allá del plano

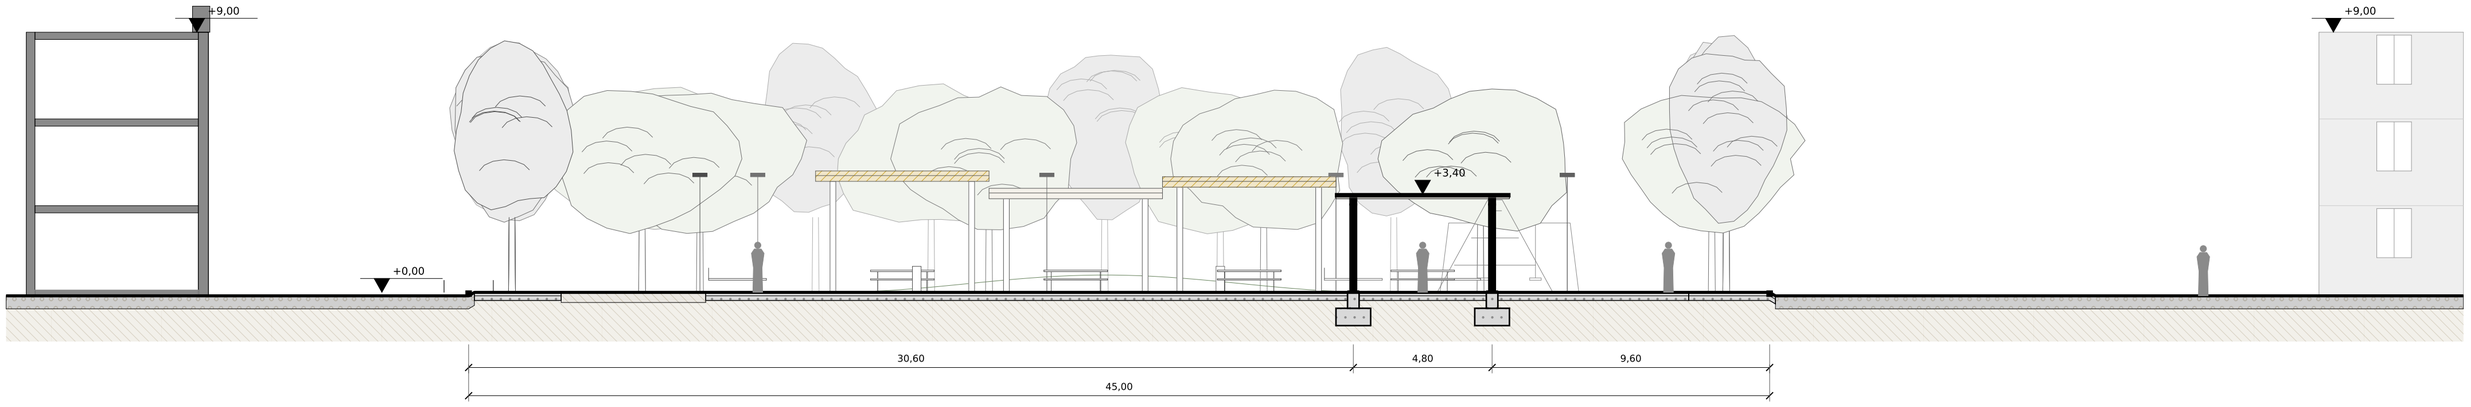

SECCIÓN TRANSVERSAL D-D' · PLAZA 2 (por el eje de la calle norte y la escalera de pérgolas)

E 1:150 · corte por pilares; en proyección, pérgolas, mobiliario y arbolado más allá del plano

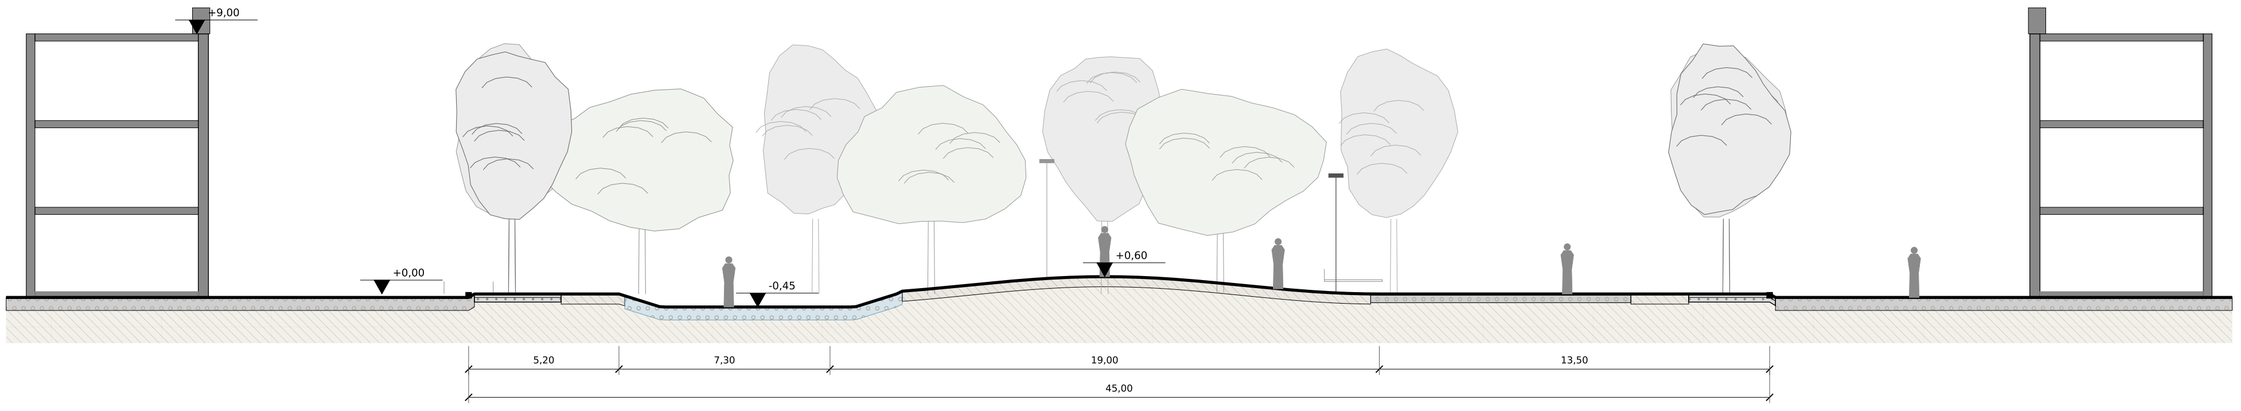

SECCIÓN TRANSVERSAL E-E' · PLAZA 2 (por el montículo y el jardín de lluvia)

E 1:150 · corte por pilares; en proyección, pérgolas, mobiliario y arbolado más allá del plano

CASO_010 · PROPUESTA A Secciones transversales B-B' (Plaza 1), D-D' y E-E' (Plaza 2)	Plano **S02**	
Anteproyecto · Dos plazas de barrio	Escala 1:150	Lámina S02