

SECCIÓN CONSTRUCTIVA DE LA PÉRGOLA, DE LA CIMENTACIÓN A LA CUBIERTA


Plano de corte por el eje de pilares, perpendicular a la viga. E 1:25

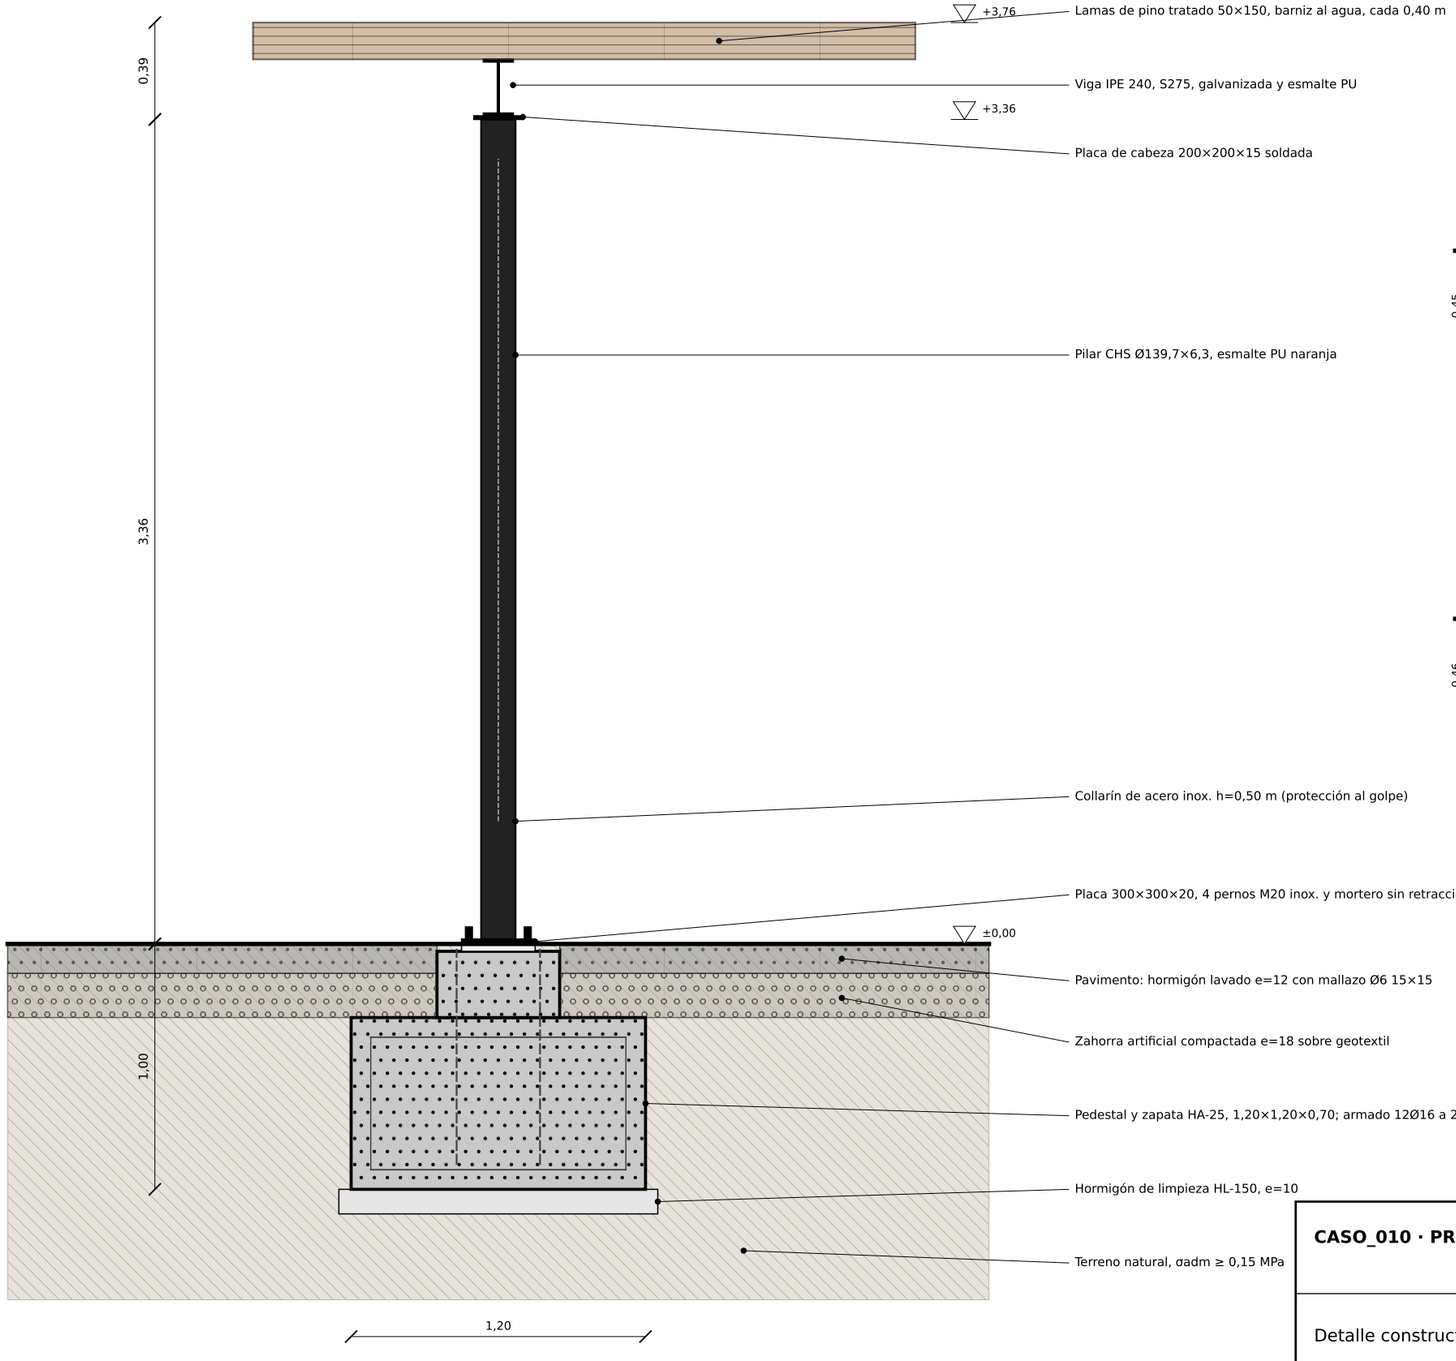


A · PAVIMENTO DURO (CAMINOS Y PLAZOLETAS)

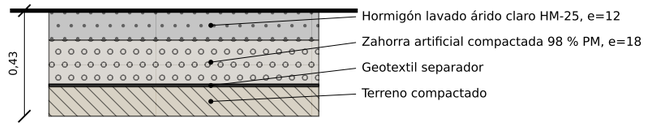

B · ZONA DE JUEGOS (CAUCHO CONTINUO)

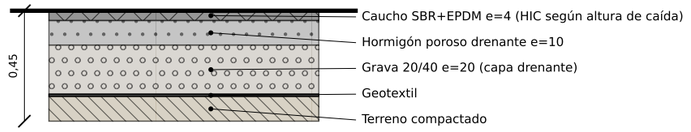

C · PRADERA Y CUBRESUELOS

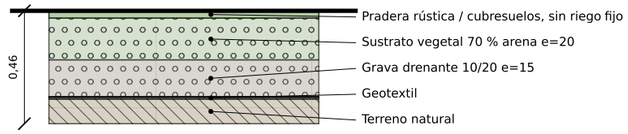

Pendiente de los pavimentos: 1,5 % hacia las praderas (drenaje por infiltración en bandas verdes). Sin juntas de dilatación en el caucho.

CASO_010 · PROPUESTA B	ESCALA	LÁMINA
Detalle constructivo: pérgola, cimentación y pavimentos	**1:25**	**D01**
		Anteproyecto