
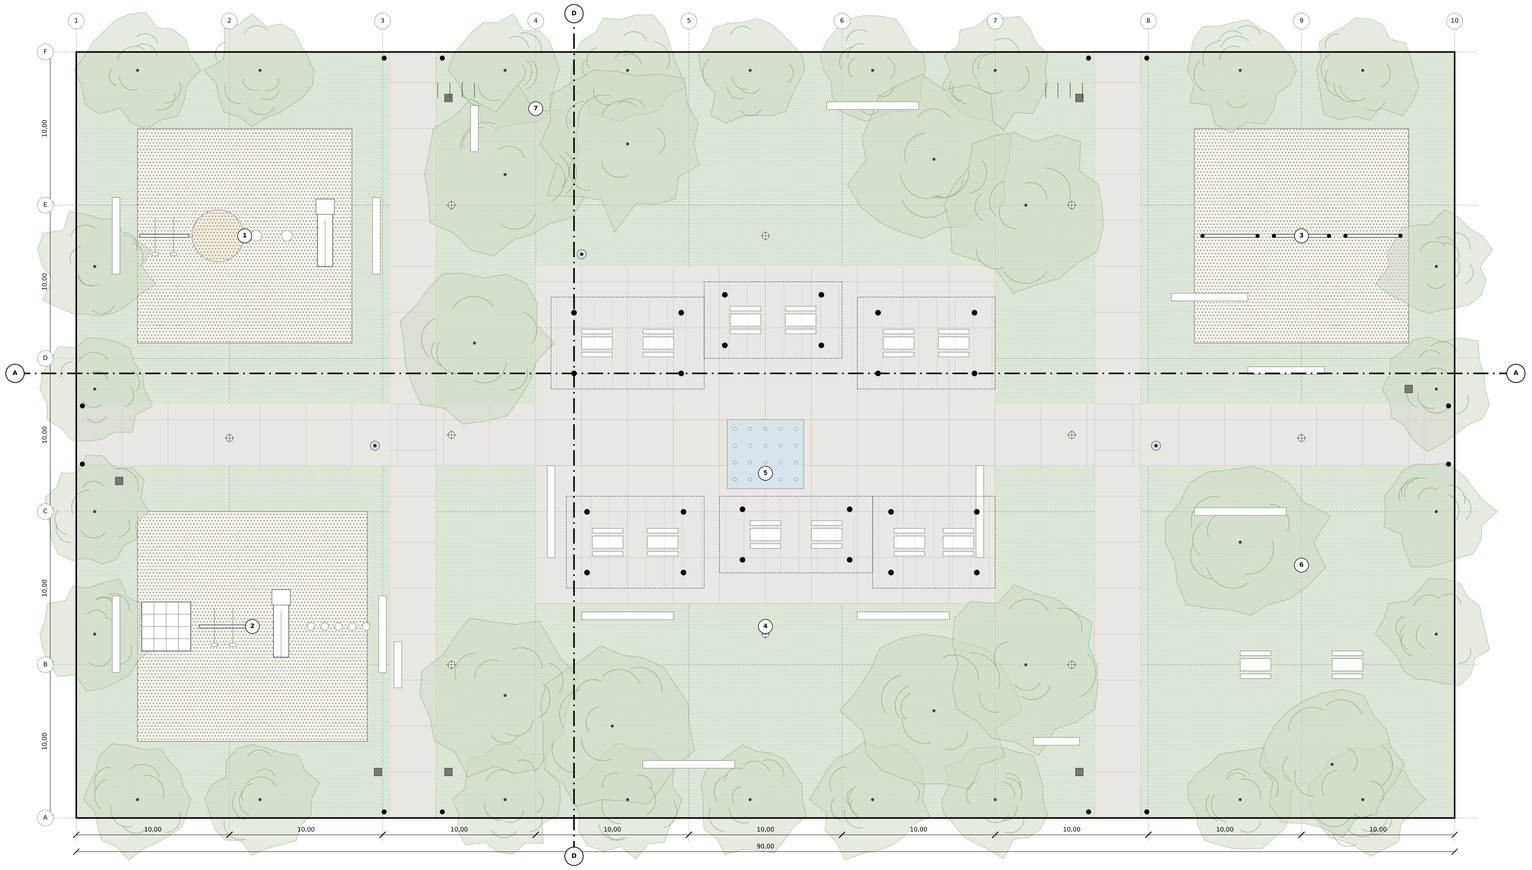


PLAZA 1 · «EL PÓRTICO»

E 1:200 · 4.500 m²

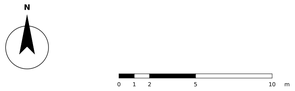

LEYENDA

PLAZA 1 · «EL PÓRTICO»

1. Juegos 0-5 años (caucho continuo)
   196 m²
2. Juegos 6-12 años (caucho continuo)
   225 m²
3. Calistenia y ocio activo (caucho)
   196 m²
4. Salón de pérgolas: 6 módulos, 311 m² cubiertos
   pavimento 660 m²
5. Juego de agua a ras de suelo
   22,5 m²
6. Pradera y ocio ligero (ping-pong, ajedrez)
   pad 112 m²
7. Cuadro de arbolado: 37 ud
   copa 4,3-5,2 m

PLAZA 2 · «LA GALERÍA»

1. Juegos 6-12 años (caucho continuo)
   280 m²
2. Juegos 0-5 años (caucho, seto bajo)
   168 m²
3. Calistenia (caucho continuo)
   96 m²
4. Galería norte: 9 módulos, 425 m² cubiertos
   pavimento 1.400 m²
5. Ocio ligero: ping-pong y ajedrez
   168 m²
6. Pradera arbolada y alcorques corridos
   31 árboles
7. Diagonal accesible (calle - calle), 3,50 m
   pend. ≤ 1,5 %


SÍMBOLOS

- Árbol
- Pérgola (sobre el corte) y pilar
- Luminaria
- Bolardo en accesos
- Bebedero
- Papelera
- Banco 1,80 m
- Mesa con bancos

CUADRO DE SUPERFICIES (m²)

	P1	P2
Parcela	4.500 m²	4.725 m²
Pavimento duro	1.176 m²	1.556 m²
Caucho / juego	617 m²	544 m²
Pradera y alcorques	2.707 m²	2.625 m²
Total intervención	9.225 m²	

Secciones: A-A' y D-D' (P1), B-B' y C-C' (P2). Los ejes son una malla de replanteo de 10 m.

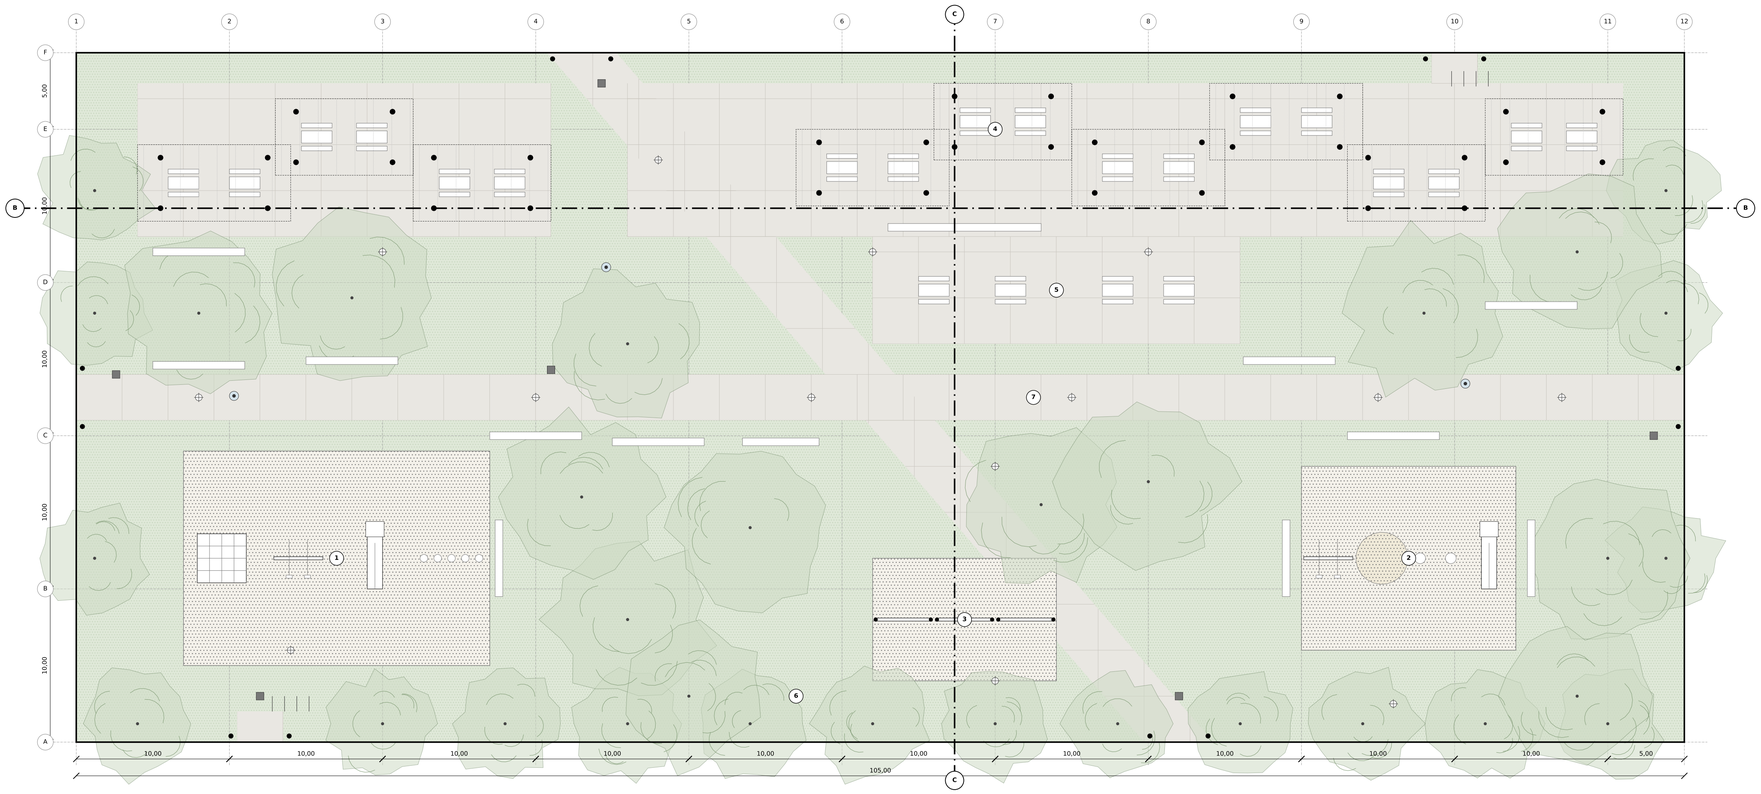

PLAZA 2 · «LA GALERÍA»

E 1:200 · 4.725 m²

CASO_010 · PROPUESTA B

Planta de conjunto. Pavimentos, mobiliario y arbolado

ESCALA 1:200

LÁMINA P01 Anteproyecto