


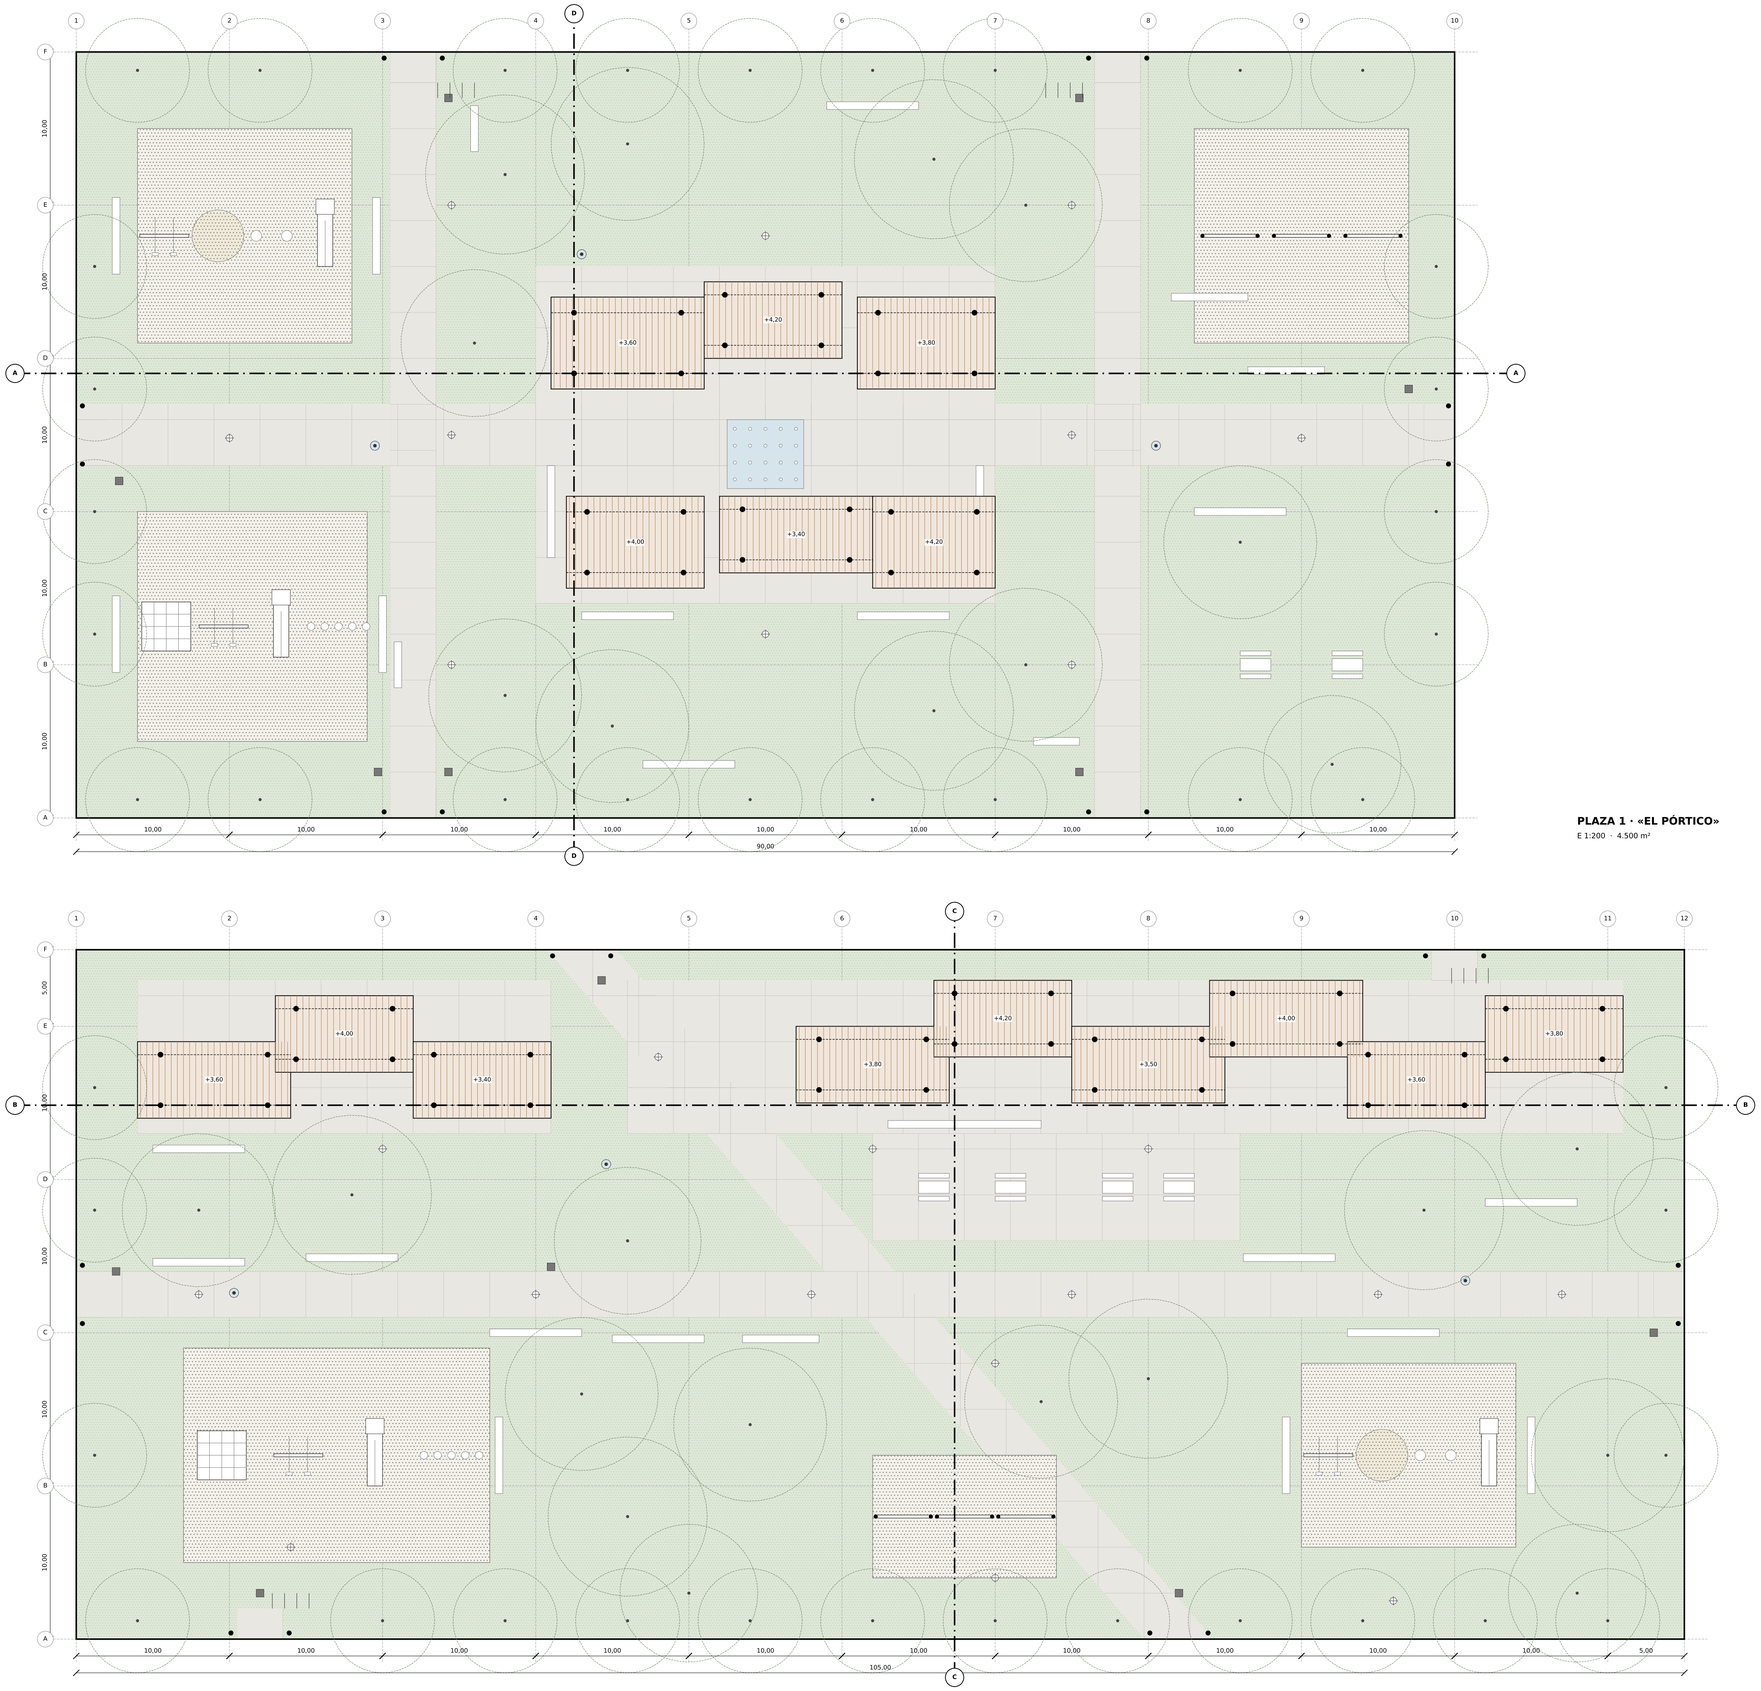

LEYENDA DE CUBIERTAS

Pérgola: lamas de madera 50×150 cada 0,40 m (cota de lama superior)

Vigas IPE 240 (trazo discontinuo) sobre pilares CHS Ø139

Copas de arbolado (contorno discontinuo)

CUADRO DE PÉRGOLAS

P1.1	10 × 6 m	+3,60 m	60 m²
P1.2	9 × 5 m	+4,20 m	45 m²
P1.3	9 × 6 m	+3,80 m	54 m²
P1.4	9 × 6 m	+4,00 m	54 m²
P1.5	10 × 5 m	+3,40 m	50 m²
P1.6	8 × 6 m	+4,20 m	48 m²
P2.1	10 × 5 m	+3,60 m	50 m²
P2.2	9 × 5 m	+4,00 m	45 m²
P2.3	9 × 5 m	+3,40 m	45 m²
P2.4	10 × 5 m	+3,80 m	50 m²
P2.5	9 × 5 m	+4,20 m	45 m²
P2.6	10 × 5 m	+3,50 m	50 m²
P2.7	10 × 5 m	+4,00 m	50 m²
P2.8	9 × 5 m	+3,60 m	45 m²
P2.9	9 × 5 m	+3,80 m	45 m²

Sombra proyectada de las pérgolas a 45º: 311 m² (P1) + 425 m² (P2).

Proyección de copas de arbolado: ≈ 1.810 m² (P1) y ≈ 1.660 m² (P2), sin descontar solapes.

Secciones: A-A' y D-D' (P1), B-B' y C-C' (P2).

PLAZA 1 · «EL PÓRTICO»
E 1:200 · 4.500 m²

PLAZA 2 · «LA GALERÍA»
E 1:200 · 4.725 m²

CASO_010 · PROPUESTA B

Planta de cubiertas: pérgolas y copas

ESCALA
1:200

LÁMINA
P03
Anteproyecto