



SECCIÓN A-A' · PLAZA 1

E 1:200

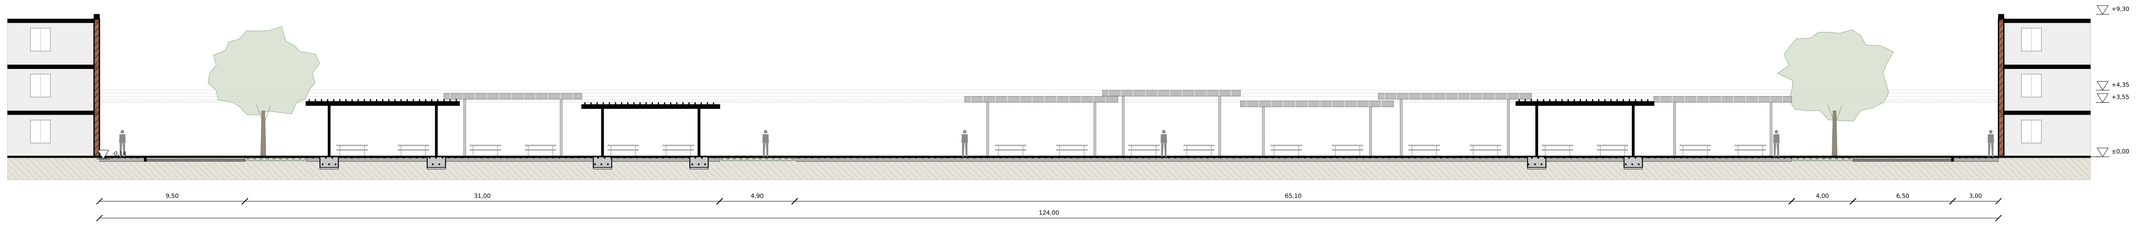

SECCIÓN B-B' · PLAZA 2

E 1:200

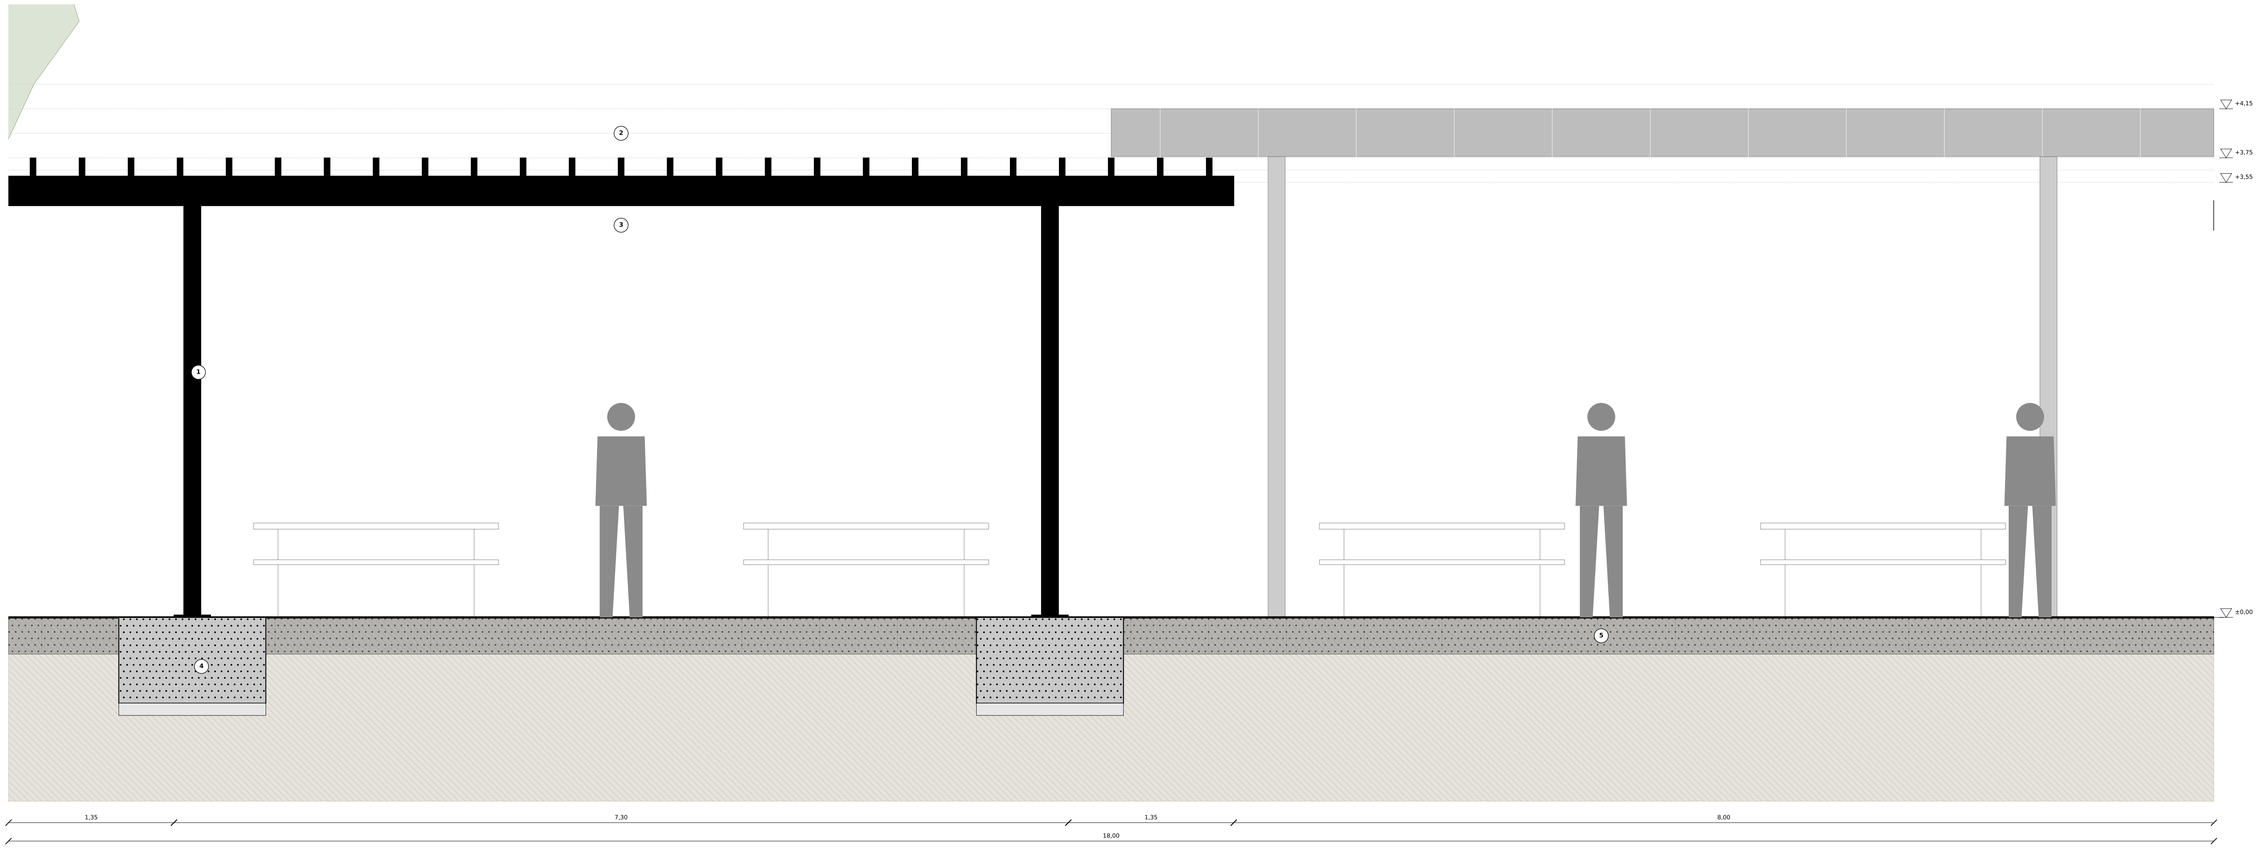

FRAGMENTO DE LA GALERÍA NORTE, SECCIÓN B-B'

E 1:25

TRAMAS Y MATERIALES

- Hormigón armado / pavimento
- Caucho continuo drenante
- Sustrato vegetal y grava drenante
- Terreno natural
- Fábrica de ladrillo (fachadas vecinas)
- Acero, madera y forjados cortados

1. Pilar CHS Ø139,7×6,3, acero S275 galvanizado y esmalte naranja
2. Lamas de pino tratado 50×150, cada 0,40 m
3. Viga IPE 240 con voladizo de 1,50 m
4. Zapata aislada 1,20×1,20×0,70 m, HA-25
5. Pavimento: hormigón lavado e=12 + zahorra e=18

Cotas en metros. Alturas libres bajo pérgola: 3,25 a 4,05 m.

Edificios vecinos: 3 plantas, +9,00 (peto +9,30).

Posición de los cortes en P01.

CASO_010 · PROPUESTA B	ESCALA	LÁMINA
Secciones longitudinales A-A' (Plaza 1), B-B' (Plaza 2) y fragmento 1:25	**1:200 / 1:25**	**S01** Anteproyecto