



SECCIÓN D-D' · PLAZA 1 (SALÓN DE PÉRGOLAS)

E 1:100

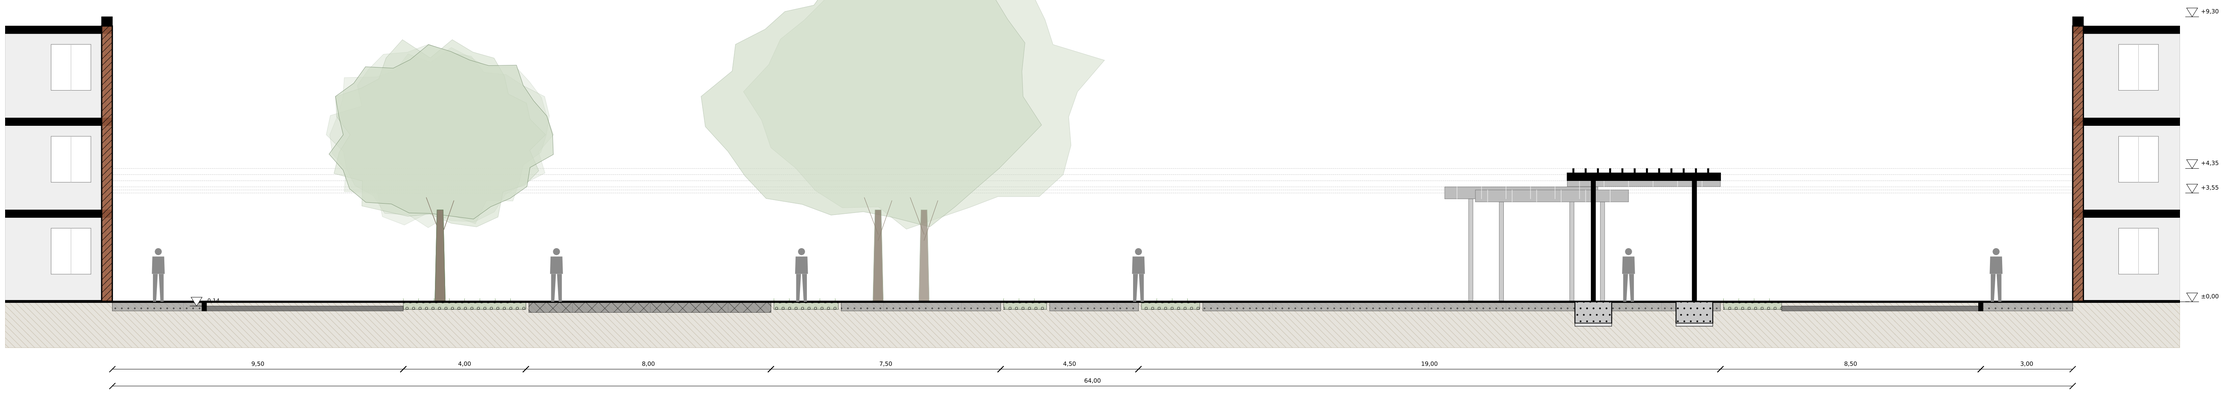

SECCIÓN C-C' · PLAZA 2 (GALERÍA NORTE)

E 1:100

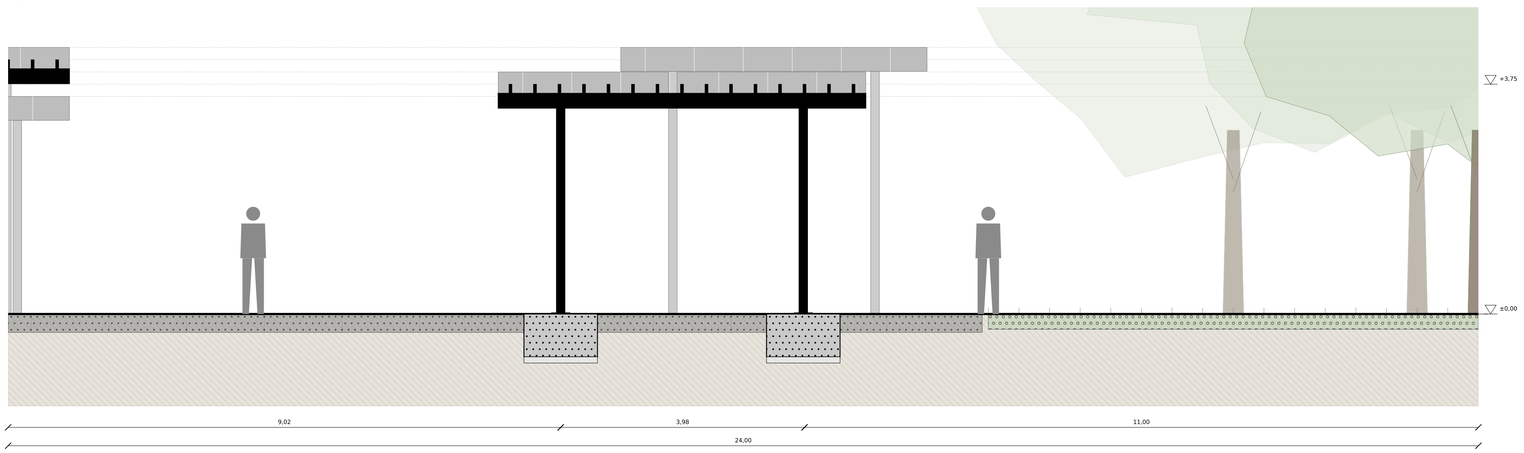

NOTAS

Las pérgolas flotan sobre el suelo: pilares a 7,00 × 4,00 m, voladizos de 1,50 m y lamas cada 0,40 m (50 % de abertura).

Sombra al mediodía de verano: la cota de lama protege sin cerrar la vista, ver P03.

Pavimento drenante: pendiente 1,5 % hacia las praderas.

Edificios vecinos 3 plantas, +9,00; calzada local -0,14.

Tramas y materiales: ver leyenda de S01.

Posición de los cortes en P01.

FRAGMENTO DEL SALÓN, SECCIÓN D-D'

E 1:50

CASO_010 · PROPUESTA B	ESCALA	LÁMINA
Secciones transversales C-C' (Plaza 2) y D-D' (Plaza 1) y fragmento 1:50	**1:100 / 1:50**	**S02** Anteproyecto