
D01 · SECCIÓN CONSTRUCTIVA POR TECHO-PÉRGOLA TIPO A Y PAVIMENTOS

E 1:20

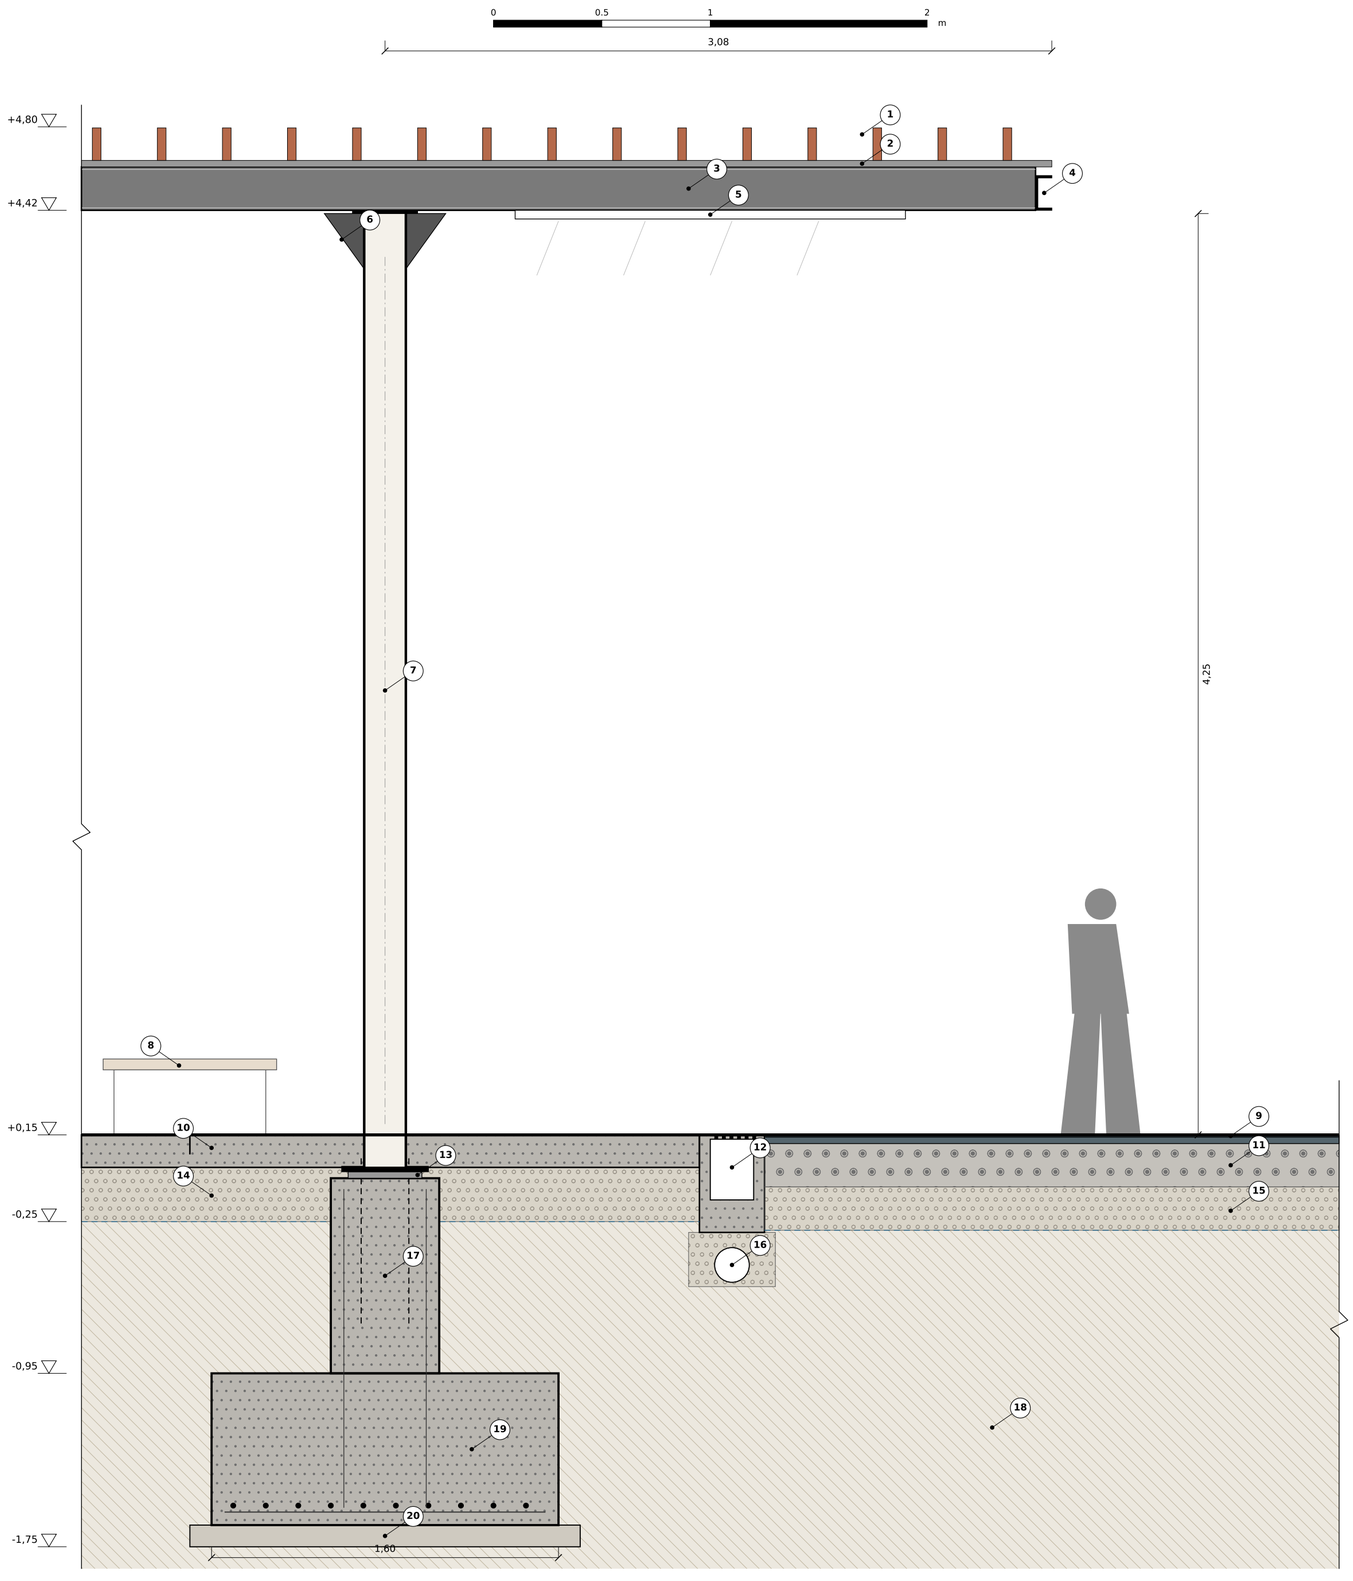

REFERENCIAS CONSTRUCTIVAS

1. Lama 150x40x2 mm de aluminio extruido lacado en terracota mate, cada 0,30 m (sombra ~50 %, permeable a lluvia y aire)
2. Rastrel omega 40x30 galvanizado, tornillería inoxidable
3. Viga doble 2 UPN 200 galvanizada en caliente y lacada; voladizo 3,00 m
4. Perfil de borde UPN 160 (zuncho perimetral)
5. Luminaria lineal LED 3000 K IP66 bajo viga
6. Placa de capitel 300x300x15 y cartelas e = 10 mm
7. Pilar tubo 200x200x8 S275 galvanizado y lacado
8. Banco de hormigón prefabricado con asiento de madera tratada
9. Caucho continuo: EPDM 1 cm + SBR 3 cm (HIC según altura de caída)
10. Pavimento de hormigón HF-4,0 fratasado, 15 cm, juntas cada 1,0 m
11. Hormigón poroso 20 cm (drenante)
12. Canaleta drenante prefabricada 200 con rejilla de fundición
13. Placa de anclaje 340x340x20, 4 pernos Ø20 L 600, mortero sin retracción
14. Zahorra artificial compactada 98 % PM, 25 cm, sobre geotextil
15. Zahorra drenante 20 cm sobre geotextil
16. Tubo dren Ø160 en lecho de grava, a red de infiltración
17. Pedestal de HA-25 50x50 cm
18. Terreno natural compactado
19. Zapata aislada HA-25 160x160x70 (tipo A, pilar único: estabilidad al vuelco), armado Ø12 c/15 en dos direcciones
20. Hormigón de limpieza HL-150, 10 cm

CASO_010 · PROPUESTA C	ESCALA	LÁMINA Anteproyecto
Sección constructiva · techo-pérgola	**E 1:20**	**D01**