
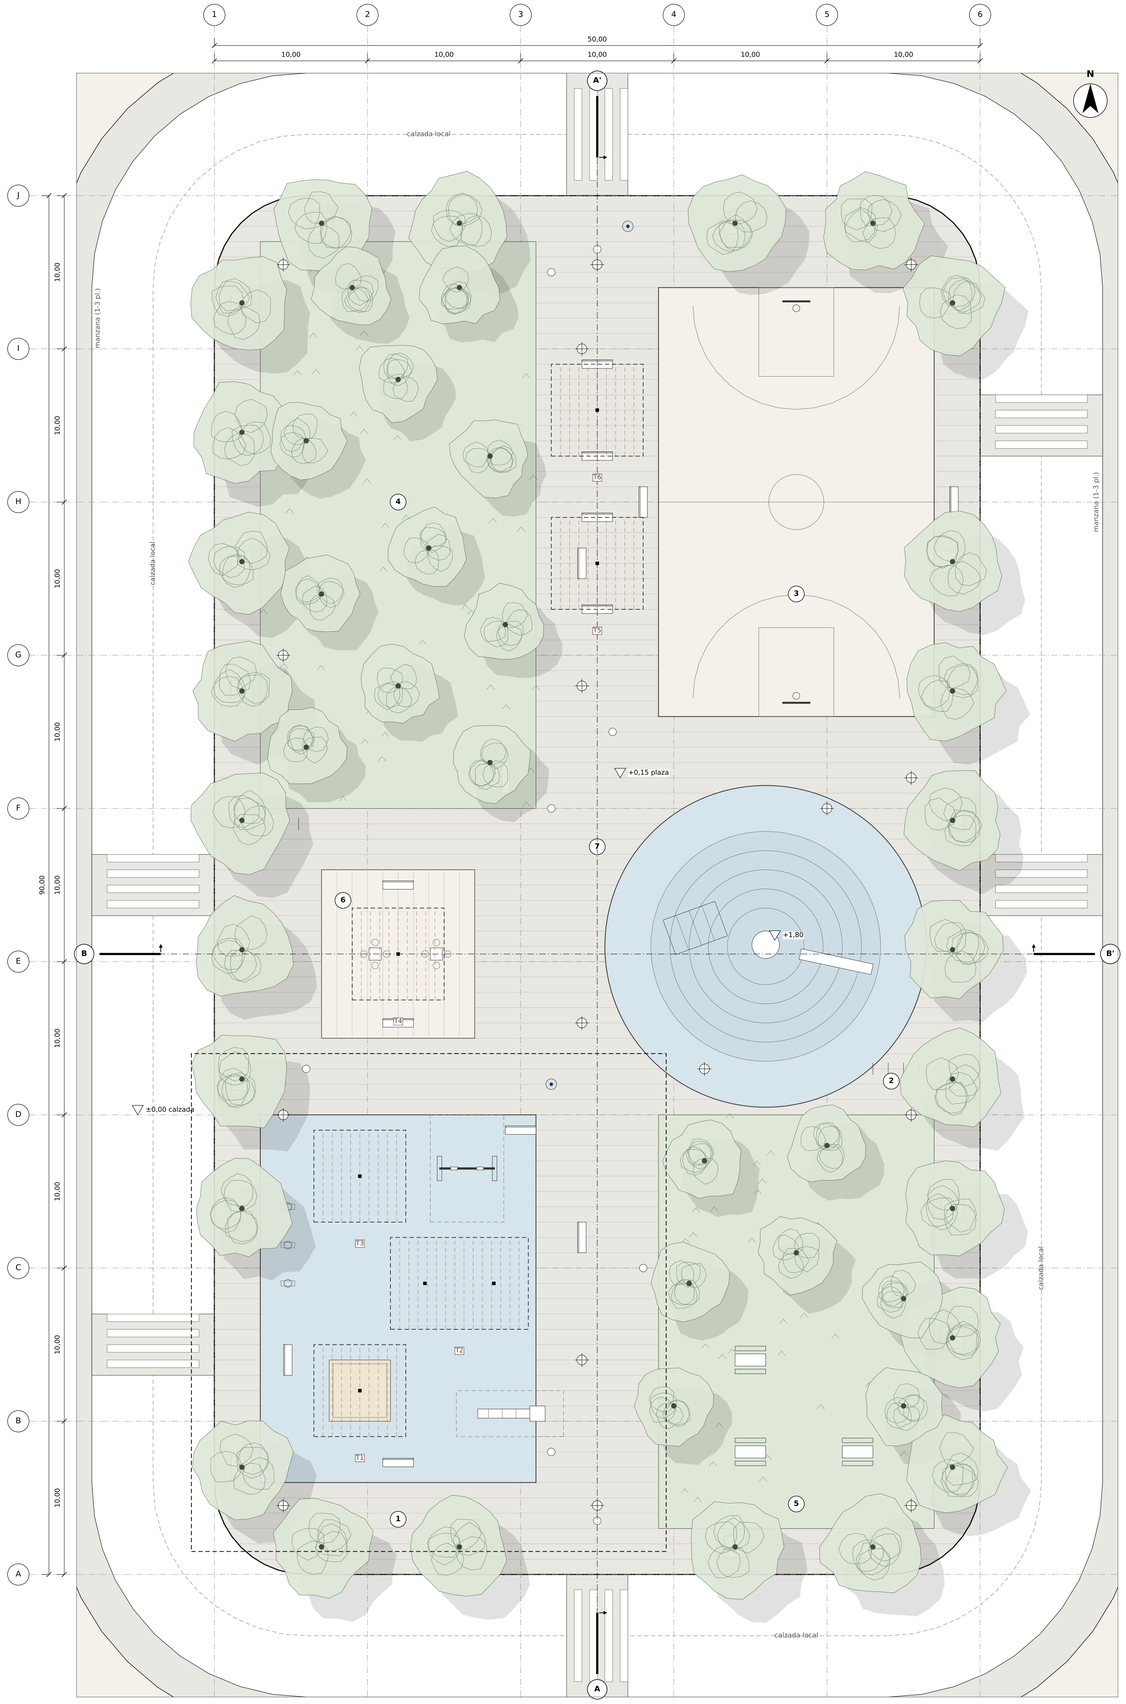


PLAZA 1 · PLANTA GENERAL

E 1:200

0 1 2 5 10 20 m

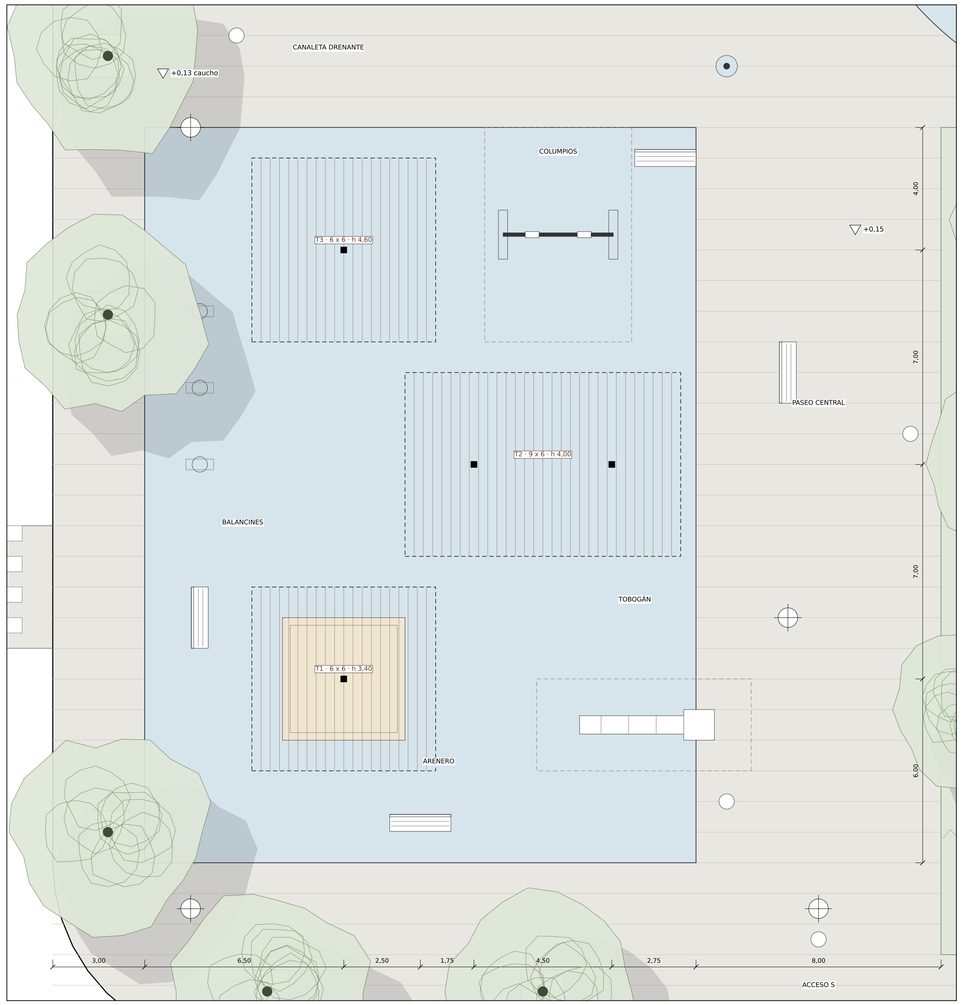

AMPLIACIÓN · JUEGOS 0-6 AÑOS BAJO LOS TECHOS T1-T3

E 1:100

0 1 2 5 m

CUADRO DE SUPERFICIES

1	Juegos 0-6 años (caucho)	432,0 m²
2	Montículo de juego 6-12 años	346,3 m²
3	Pista multiuso (baloncesto 3x3)	504,0 m²
4	Prado arbolado NO	666,0 m²
5	Prado de pícnic SE	486,0 m²
6	Sala de ajedrez bajo techo	110,0 m²
7	Plataformas, paseos y aceras interiores	1924,6 m²
	SUPERFICIE PLAZA 1	4469,0 m²
	Techos-pérgola (6 ud.)	234,0 m²
	Árboles nuevos / a mantener (ud.)	44

LEYENDA

- Pavimento de hormigón fratasado en bandas (despiece 1,0 m)
- Pavimento de piezas / pista / banda de estancia
- Pradera de bajo riego y arbustivas
- Caucho continuo de seguridad (juegos)
- Techo-pérgola en proyección (lamas sobre plano de corte)
- Pilar metálico cortado
- Báculo de iluminación LED 4,5-6 m
- Árbol (copa, alcorque y sombra a 45°)

TECHOS-PÉRGOLA

T1 6 x 6 m h 3,40 m	tipo A
T2 9 x 6 m h 4,00 m	tipo B
T3 6 x 6 m h 4,60 m	tipo A
T4 6 x 6 m h 4,60 m	tipo A
T5 6 x 6 m h 4,00 m	tipo A
T6 6 x 6 m h 3,40 m	tipo A

CASO_010 · PROPUESTA C	ESCALA	LÁMINA Anteproyecto
Plaza 1 · Planta general y ampliación	**E 1:200 / 1:100**	**P01**