
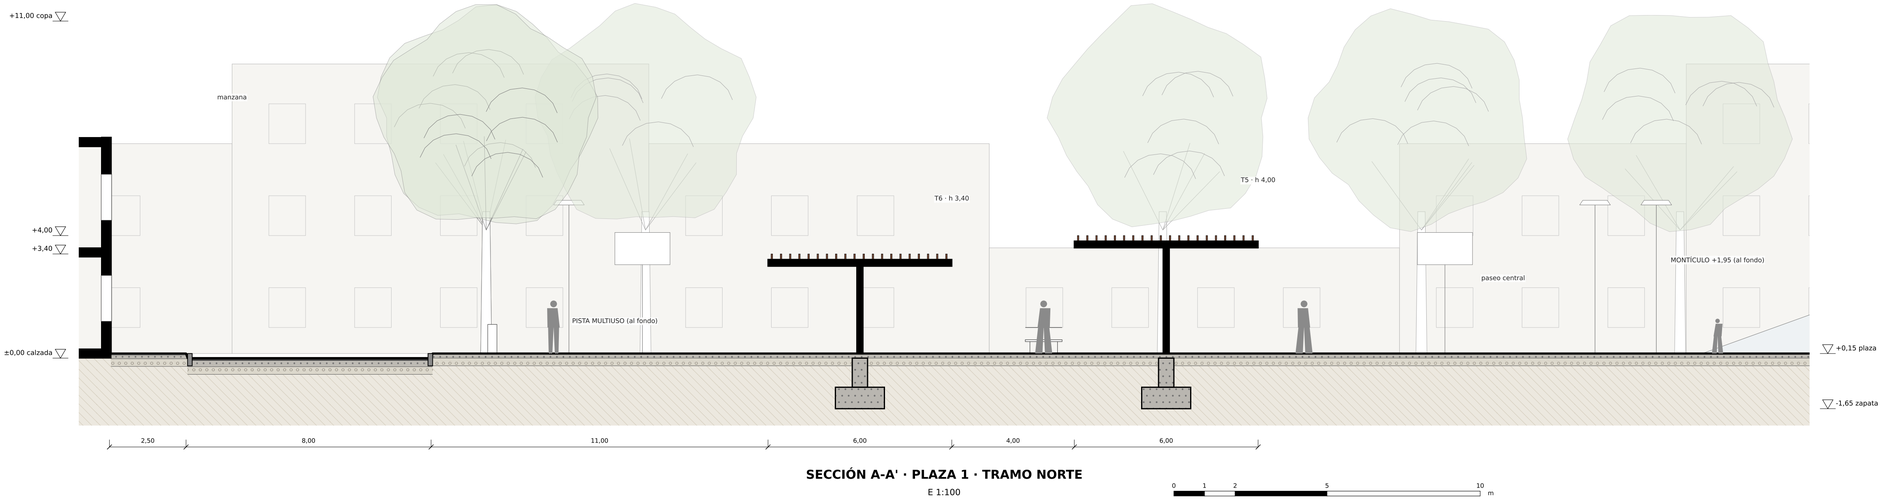


SECCIÓN A-A' · PLAZA 1 · TRAMO NORTE

E 1:100

0 1 2 5 10 m

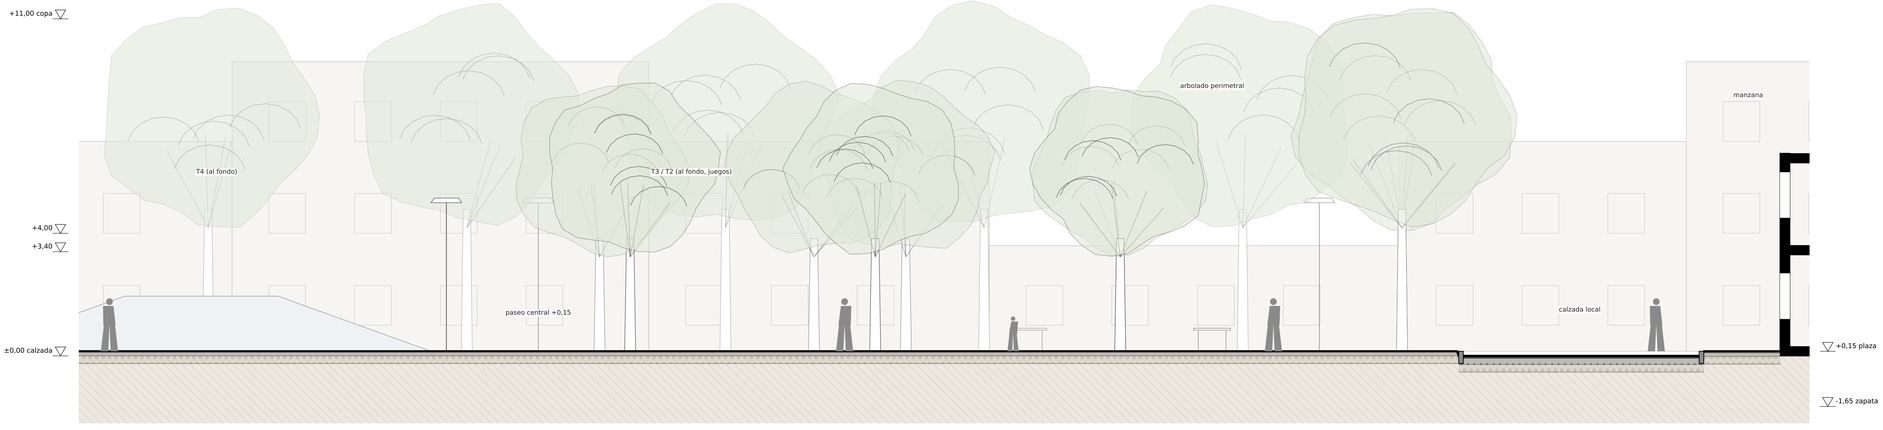


SECCIÓN A-A' · PLAZA 1 · TRAMO SUR

E 1:100

0 1 2 5 10 m

PLANO CLAVE PLAZA 1 - A-A'

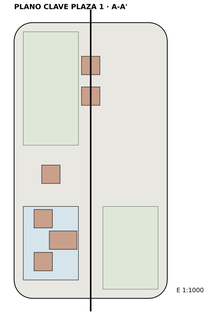

E 1:1000

MATERIALES EN CORTE

- Hormigón (pavimento 15 cm / zapatas)
- Zahorra compactada / relleno
- Tierra vegetal (pradera)
- Caucho continuo 4 cm
- Aglomerado asfáltico (calzada)
- Terreno natural
- Acero (pilares y vigas) / muros vecinos
- Lamas de aluminio lacado terracota

NOTAS

Sección longitudinal por el paseo central (eje x = 25,00 m),
mirando al este. Corta los techos T5 y T6 por sus pilares.
Plataforma única a +0,15: los pasos de calzada se
elevan a la cota de la plaza (sin bordillo en el cruce).
Zapatas aisladas HA-25: 1,60x1,60x0,70 (tipo A) y 1,30x1,30x0,60 (tipo B).
Pilares tubo 200x200x8; vigas 2 UPN 200;
lamas 150x40 mm de aluminio lacado cada 0,30 m.

CASO_010 · PROPUESTA C	ESCALA	LÁMINA Anteproyecto
Sección longitudinal A-A' (Plaza 1)	**E 1:100**	**S01**