


SECCIÓN B-B' · PLAZA 1 · TRANSVERSAL

E 1:100

0 1 2 5 10 m

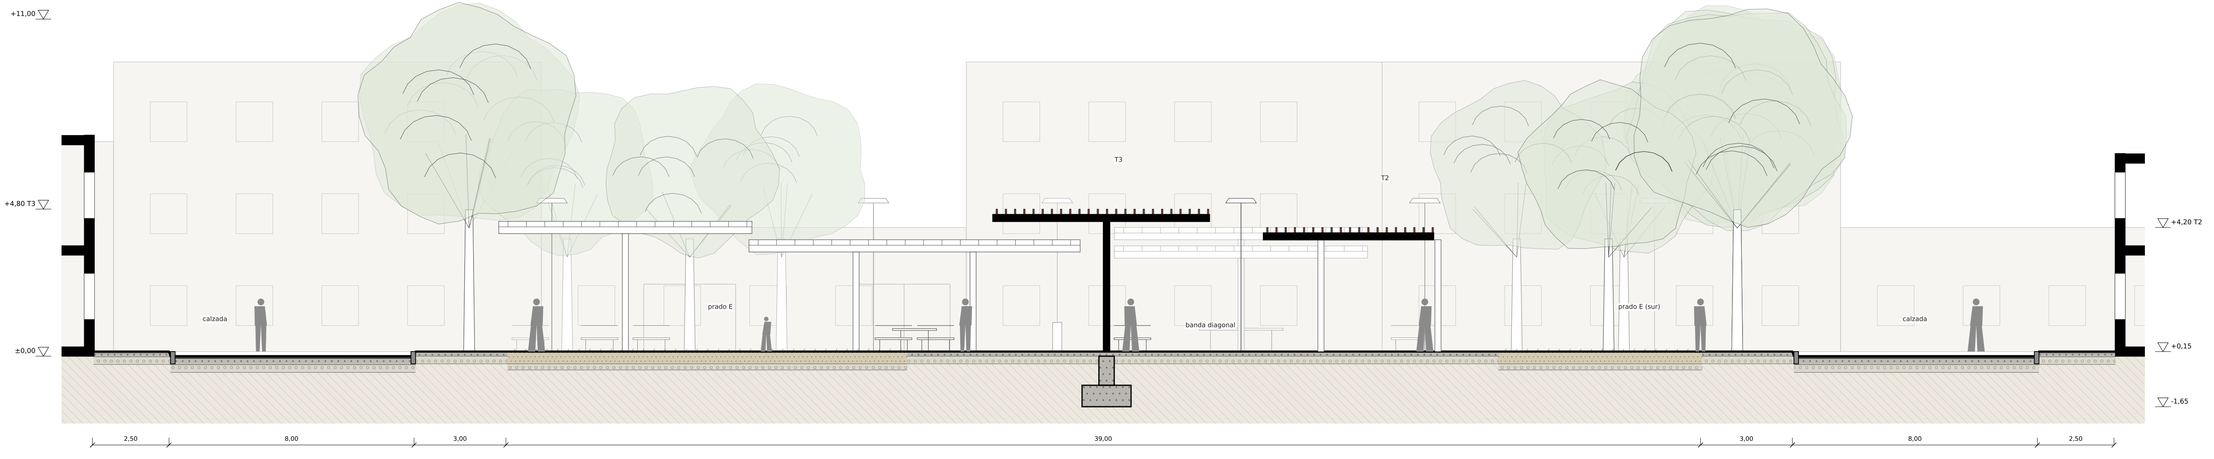

SECCIÓN C-C' · PLAZA 2 · TRANSVERSAL POR LA BANDA DIAGONAL


E 1:100

0 1 2 5 10 m

MATERIALES EN CORTE


- Hormigón (pavimento 15 cm / zapatas)
- Zahorra compactada / relleno
- Tierra vegetal (pradera)
- Caucho continuo 4 cm
- Aglomerado asfáltico (calzada)
- Terreno natural
- Acero (pilares y vigas) / muros vecinos
- Lamas de aluminio lacado terracota

PLANO CLAVE PLAZA 1 · B-B'

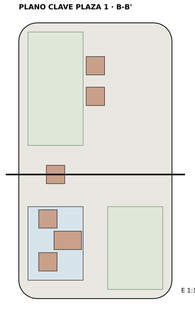

E 1:1000

PLANO CLAVE PLAZA 2 · C-C'

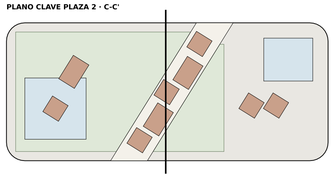

E 1:1000

CASO_010 · PROPUESTA C	ESCALA	LÁMINA Anteproyecto
Secciones transversales B-B' (P1) y C-C' (P2)	**E 1:100**	**S02**