
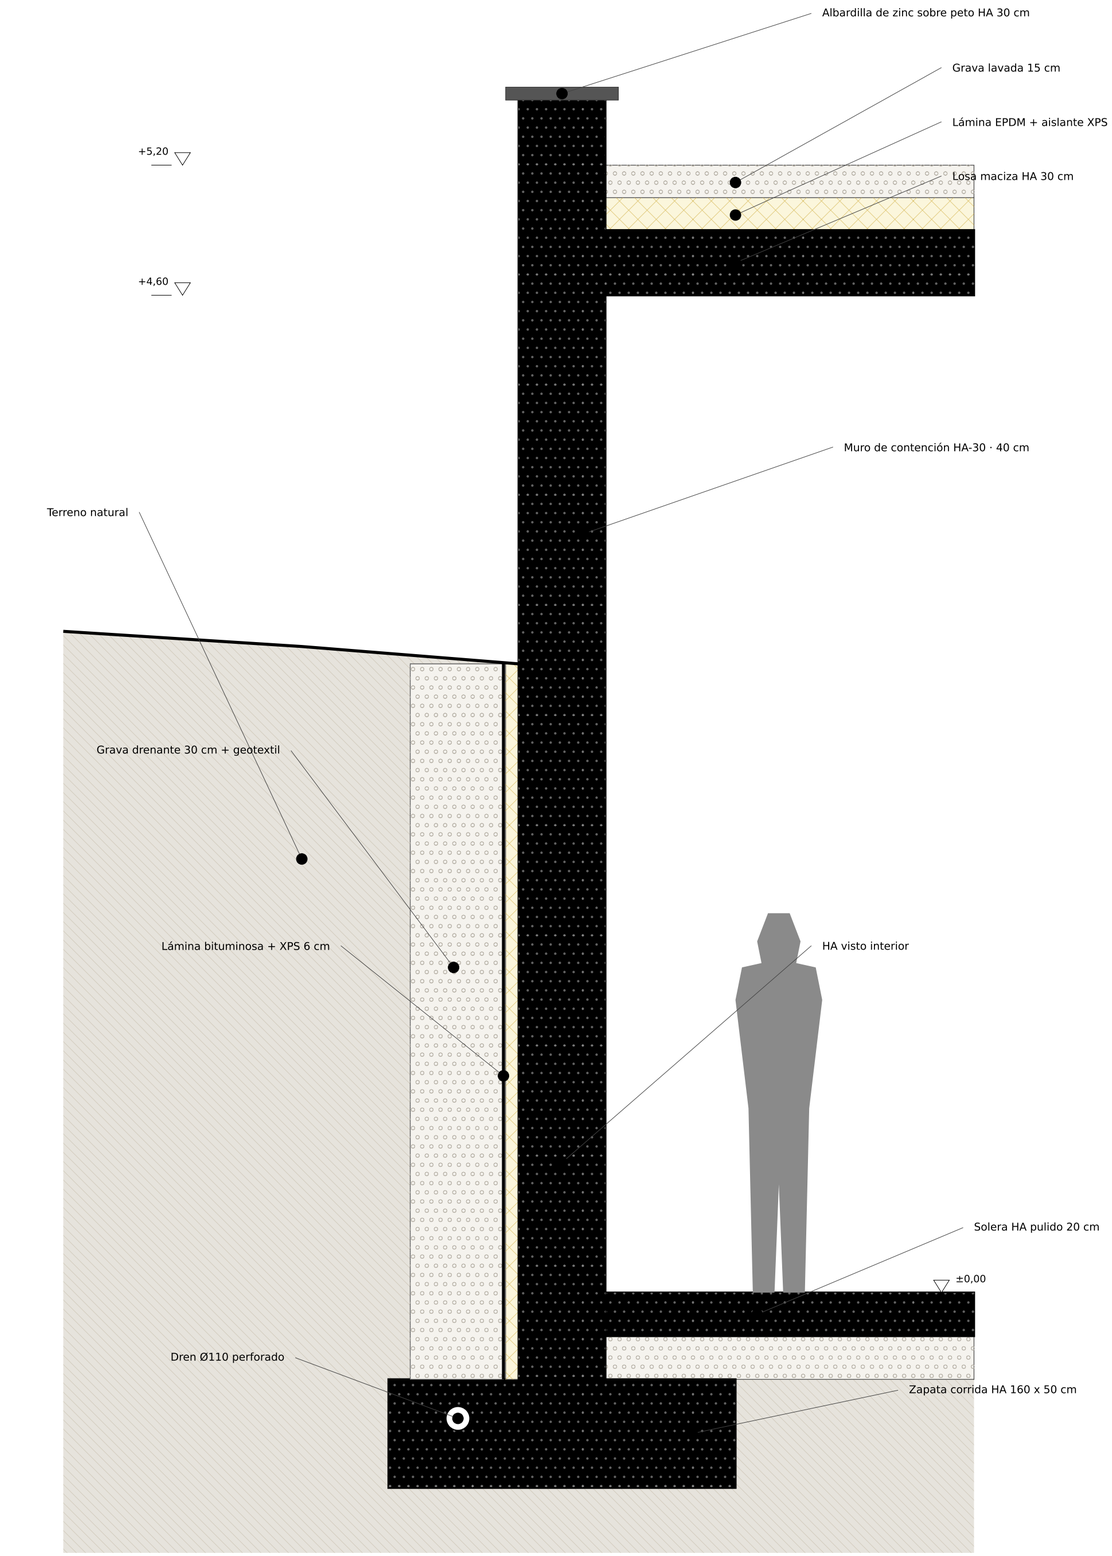


MURO DE CONTENCIÓN NORTE

E 1:20

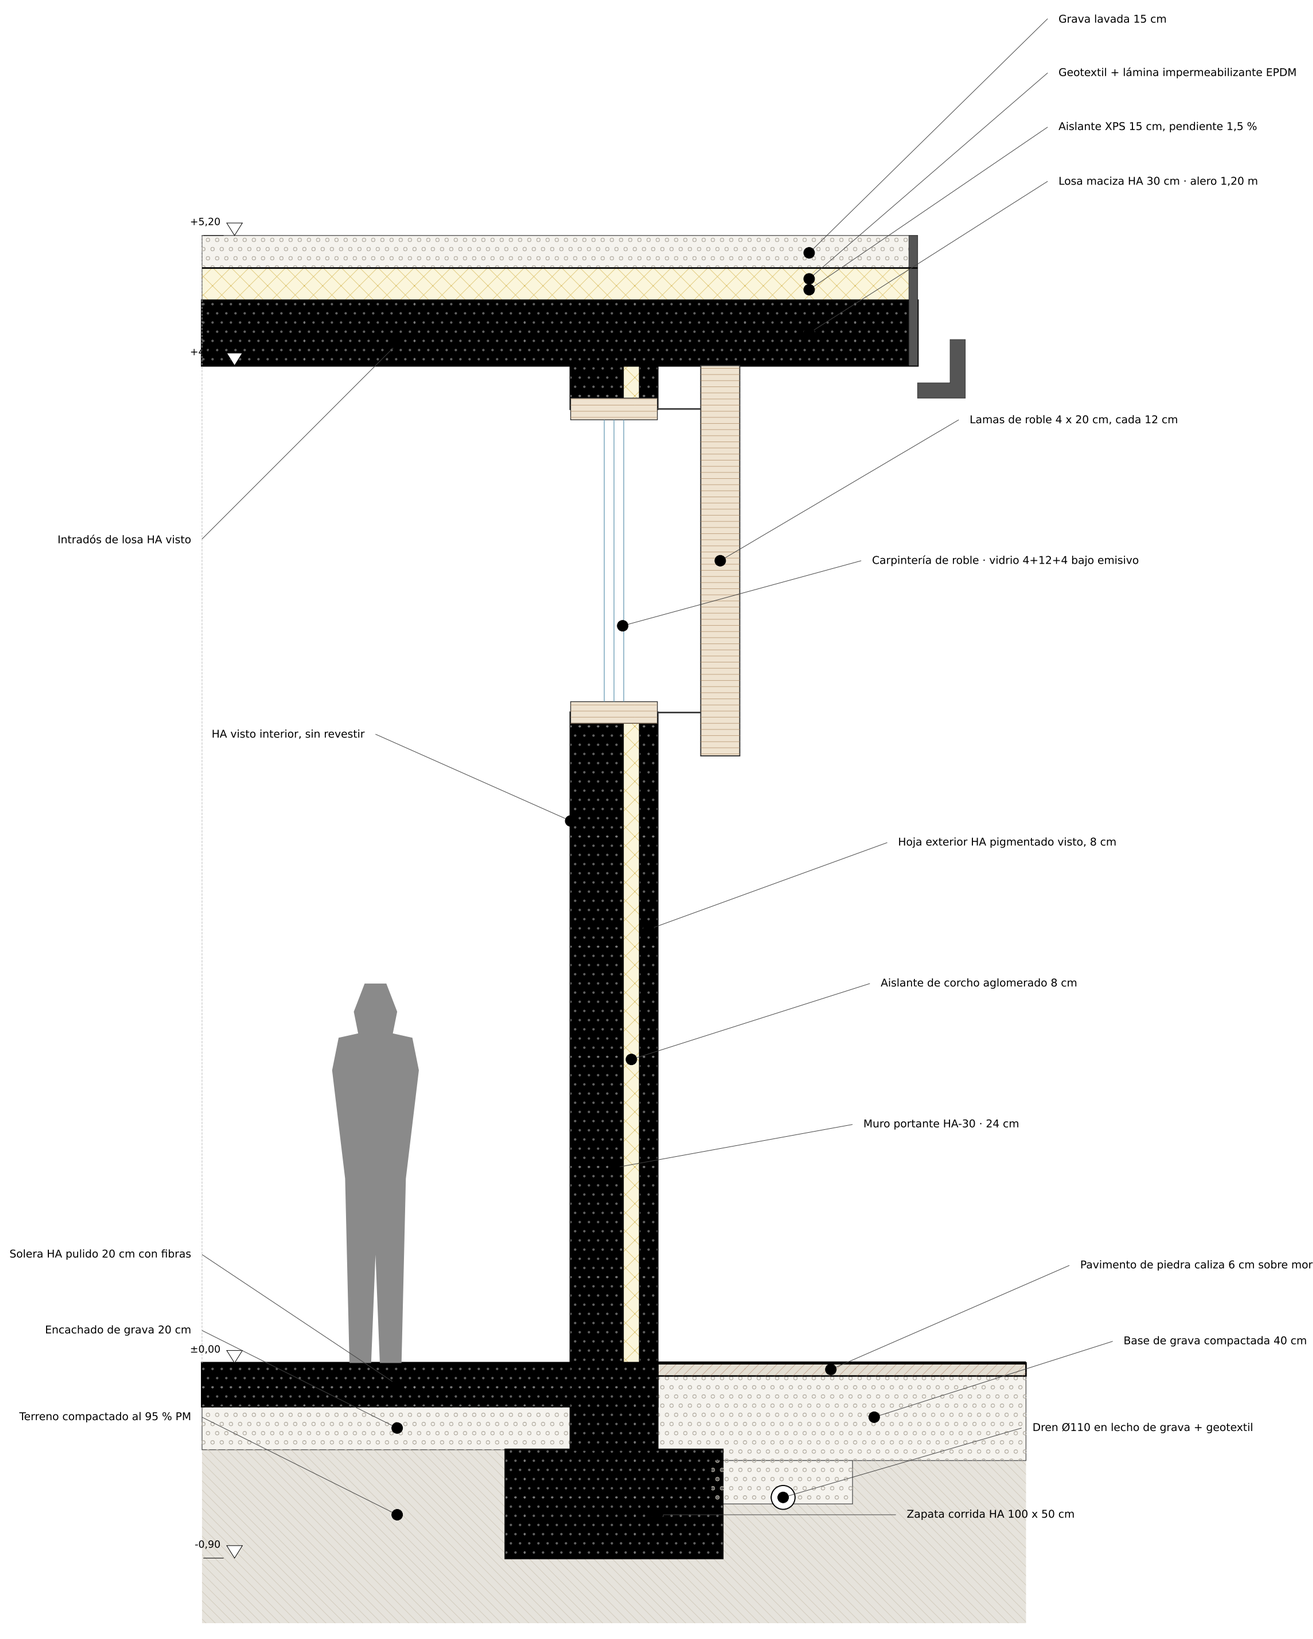

FACHADA SUR DE LA SALA

E 1:20

CASO_011 · PROPUESTA A	**E 1:20** **D01**
Sección constructiva: fachada sur y muro de contención norte	Anteproyecto