DETALLE 1 · MURO SUR DE LA SALA DE CRIANZA (de la cimentación a la cubierta)

E 1:20 · sección vertical por el eje de un panel de tapial


NOTAS

Transmitancias objetivo: cubierta U <= 0,30 W/m²K; muro de pabellón U <= 0,35;

tapial de 60 cm: retardo térmico > 12 h, sin aislante (inercia).

Hormigón HA-25/30 en cimentación y HA-30 en forjados; acero B500SD.

Cotas de nivel en metros; espesores en cm salvo indicación.

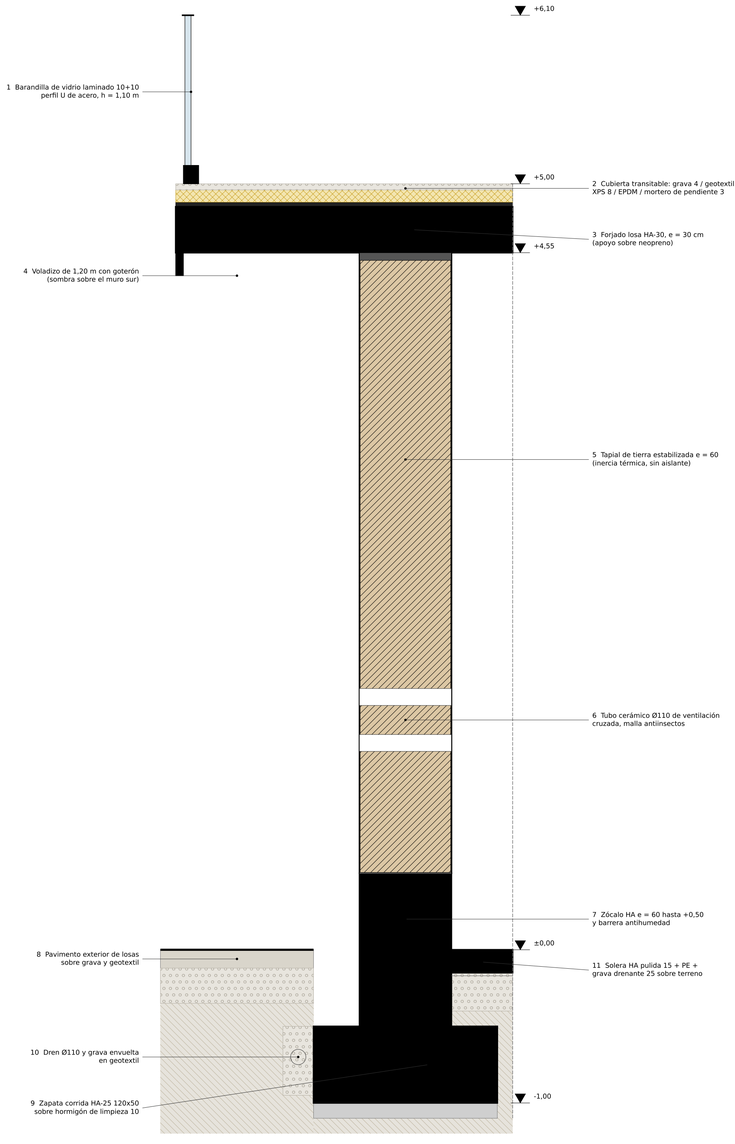


LEYENDA

Hormigón armado · Tapial · Aislante XPS · Grava / relleno · Terreno


0 0,5 1 2 m

ALZADO DEL PANEL PERFORADO (tipo)

Ø110 a 300 mm: 10 x 7 tubos = 70 uds. por panel, 3 paneles

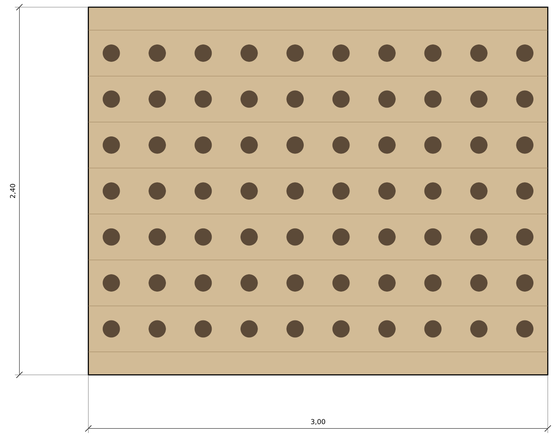

E 1:20

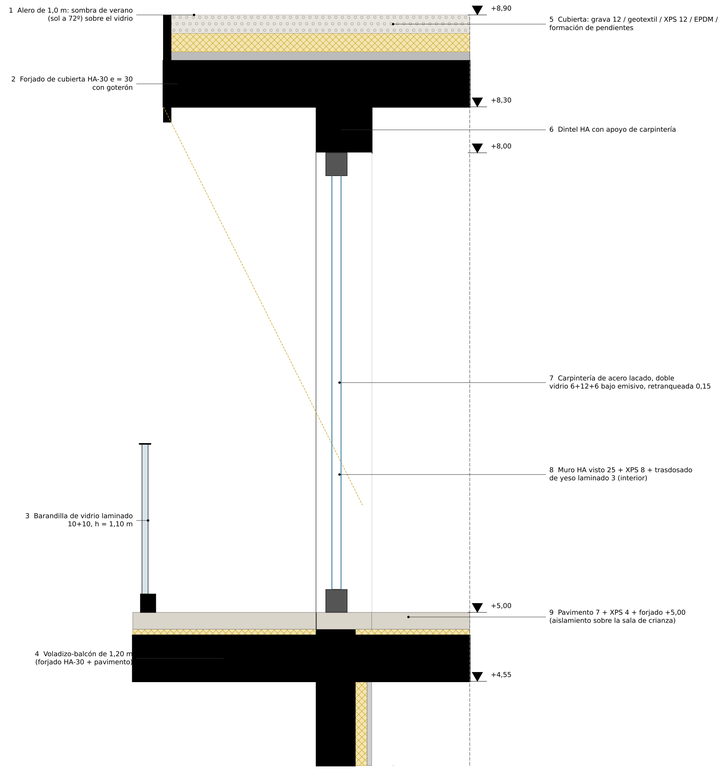

DETALLE 2 · MURO SUR DEL PABELLÓN (forjado +5,00 a cubierta +8,90)

E 1:20 · carpintería retranqueada bajo alero

CASO_011 · PROPUESTA B Sala de crianza en barricas	**Lámina D01**	
Detalle constructivo: sección de fachada sur	Escala 1:20	Anteproyecto DIN A1