
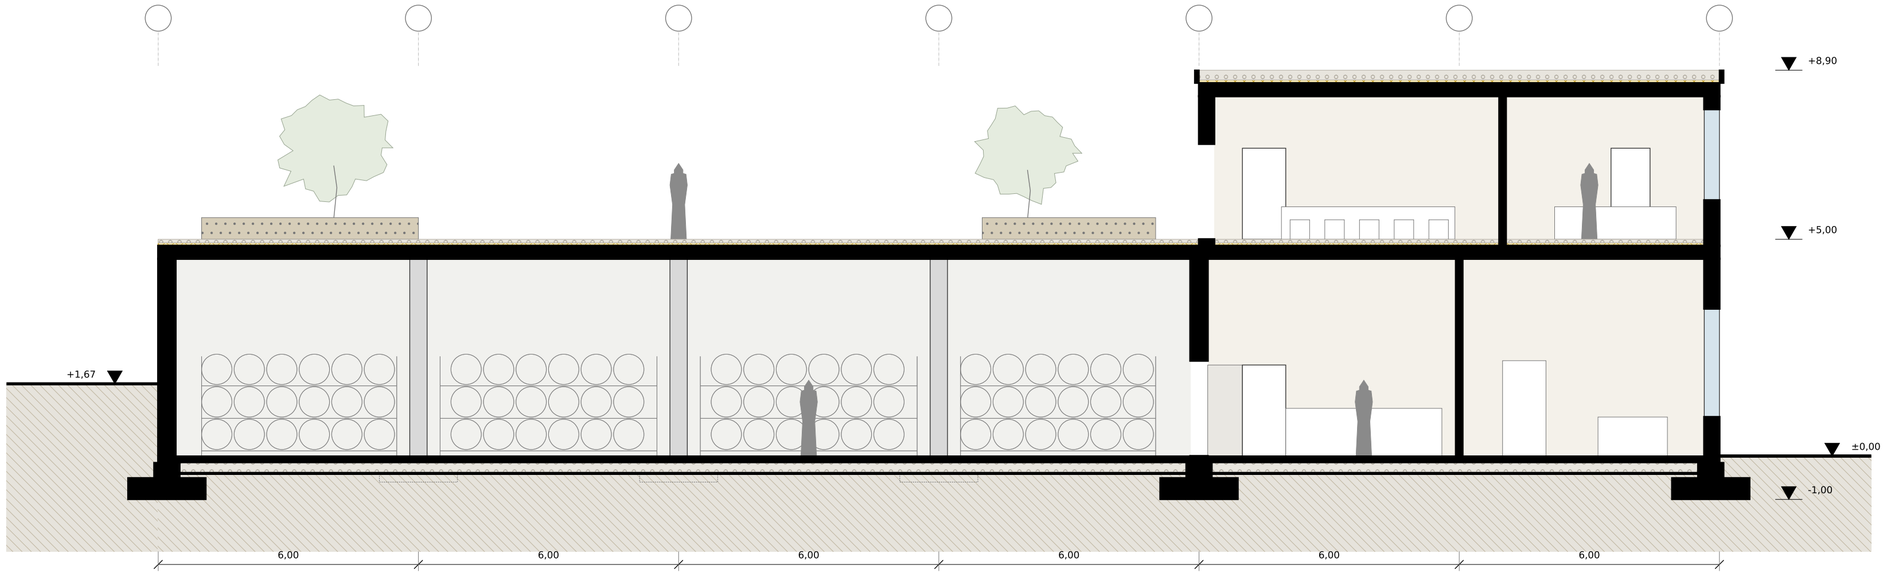


SECCIÓN A-A' (por la sala de crianza, recepción y cata, y = 4,00)
E 1:100

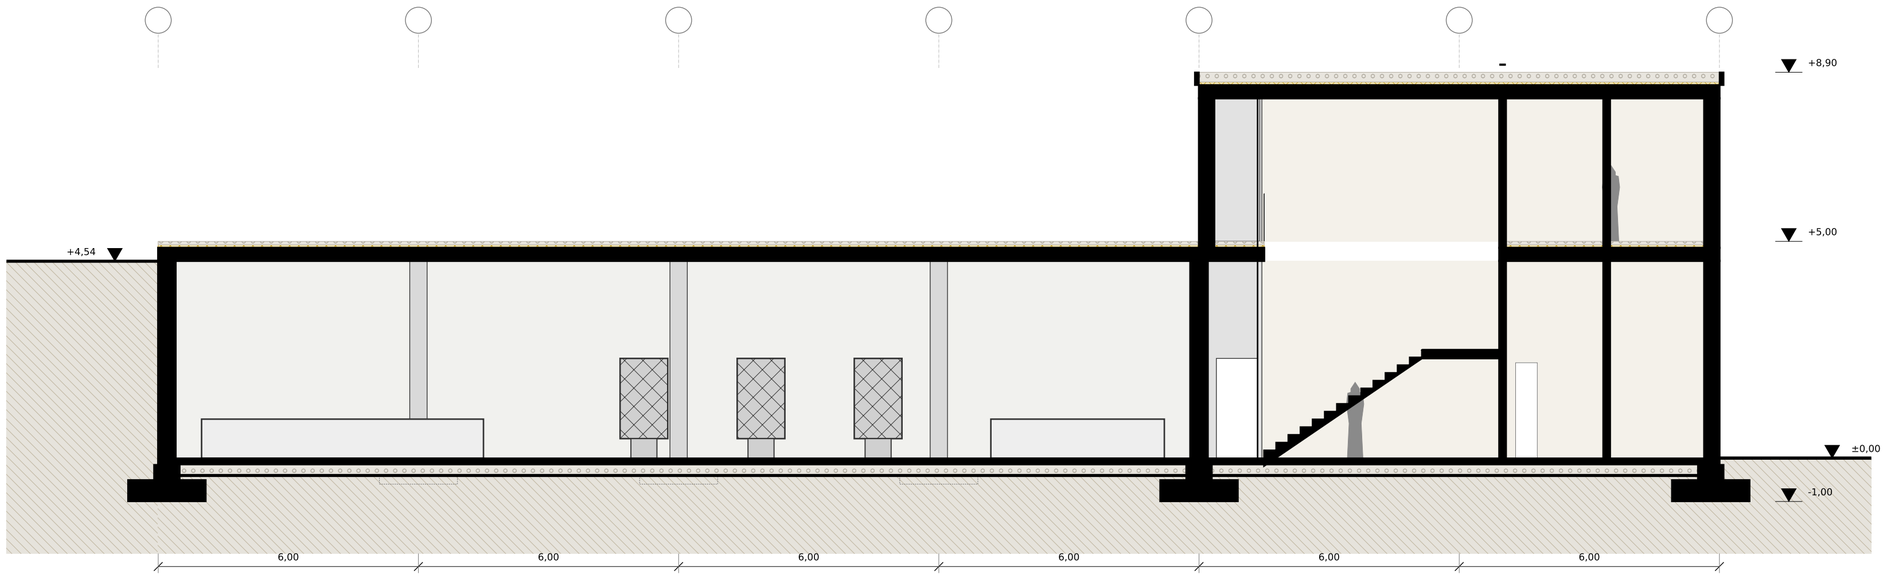

SECCIÓN C-C' (por escalera, y = 10,90)
E 1:100

0 1 2 5 10 m

CASO_011 · PROPUESTA B Sala de crianza en barricas	**Lámina S01**	
Secciones longitudinales A-A' y C-C'	Escala 1:100	Anteproyecto DIN A2