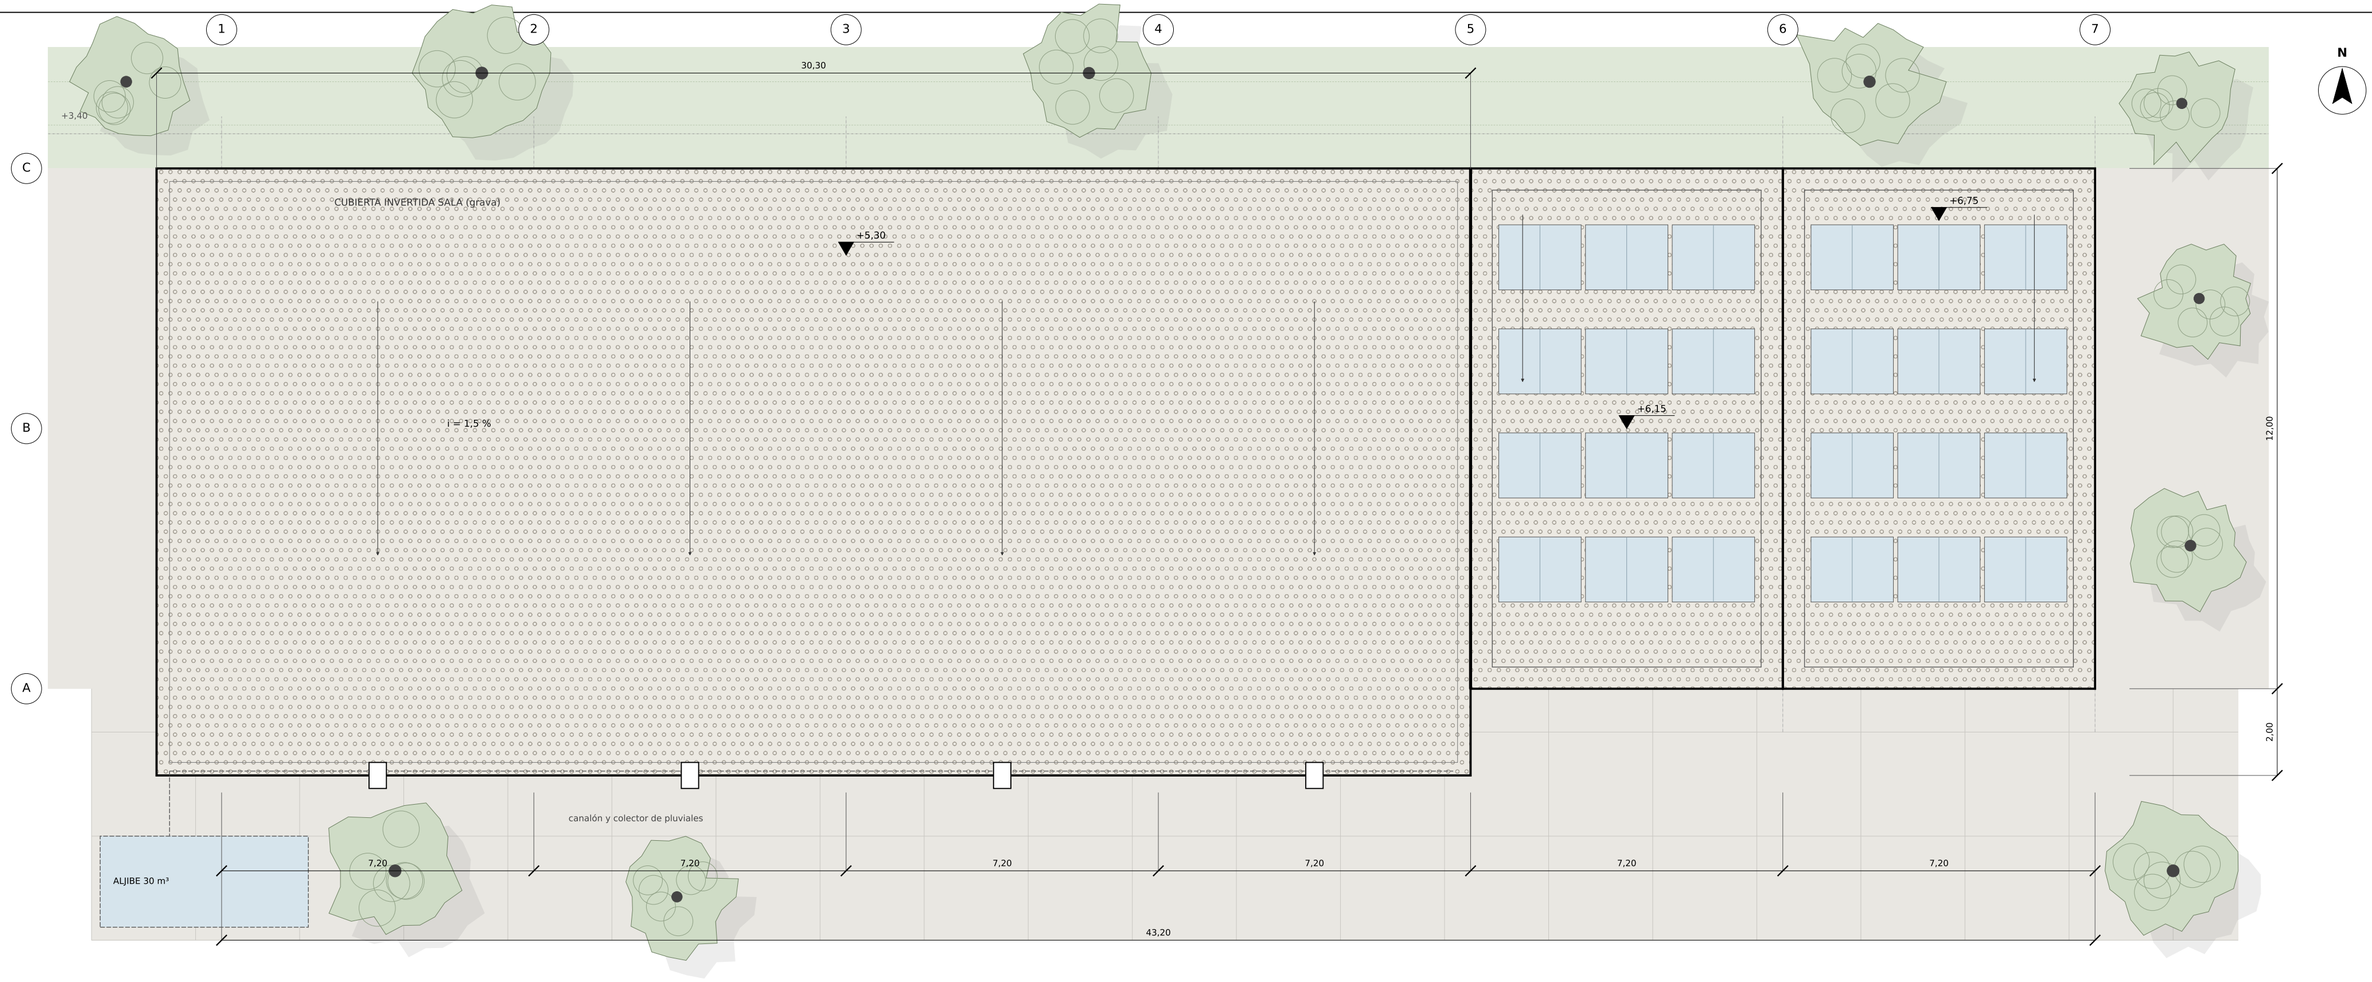


PLANTA DE CUBIERTAS

E 1:100

LEYENDA

Cubierta sala: invertida, losa 30 cm + XPS 12 cm + grava, i = 1,5 % hacia el sur (vuelo 2,00 m)

Cubierta pabellones: losa 35 cm + XPS 12 cm + grava, peto de hormigón visto a +6,75

Paneles fotovoltaicos: 24 ud. de 2,0 x 1,5 m (≈ 12 kWp) tras el peto, no visibles desde el valle

Aljibe de pluviales de 30 m³ enterrado (riego de viñedo y limpieza); rebosadero a la balsa existente

Línea discontinua: huella de muros bajo cubierta

Cotas: sala +5,30 · pabellones +6,15 · peto +6,75 · tierra norte +3,40

CASO_011 · PROPUESTA C	P02
Planta de cubiertas	E 1:100 · Anteproyecto