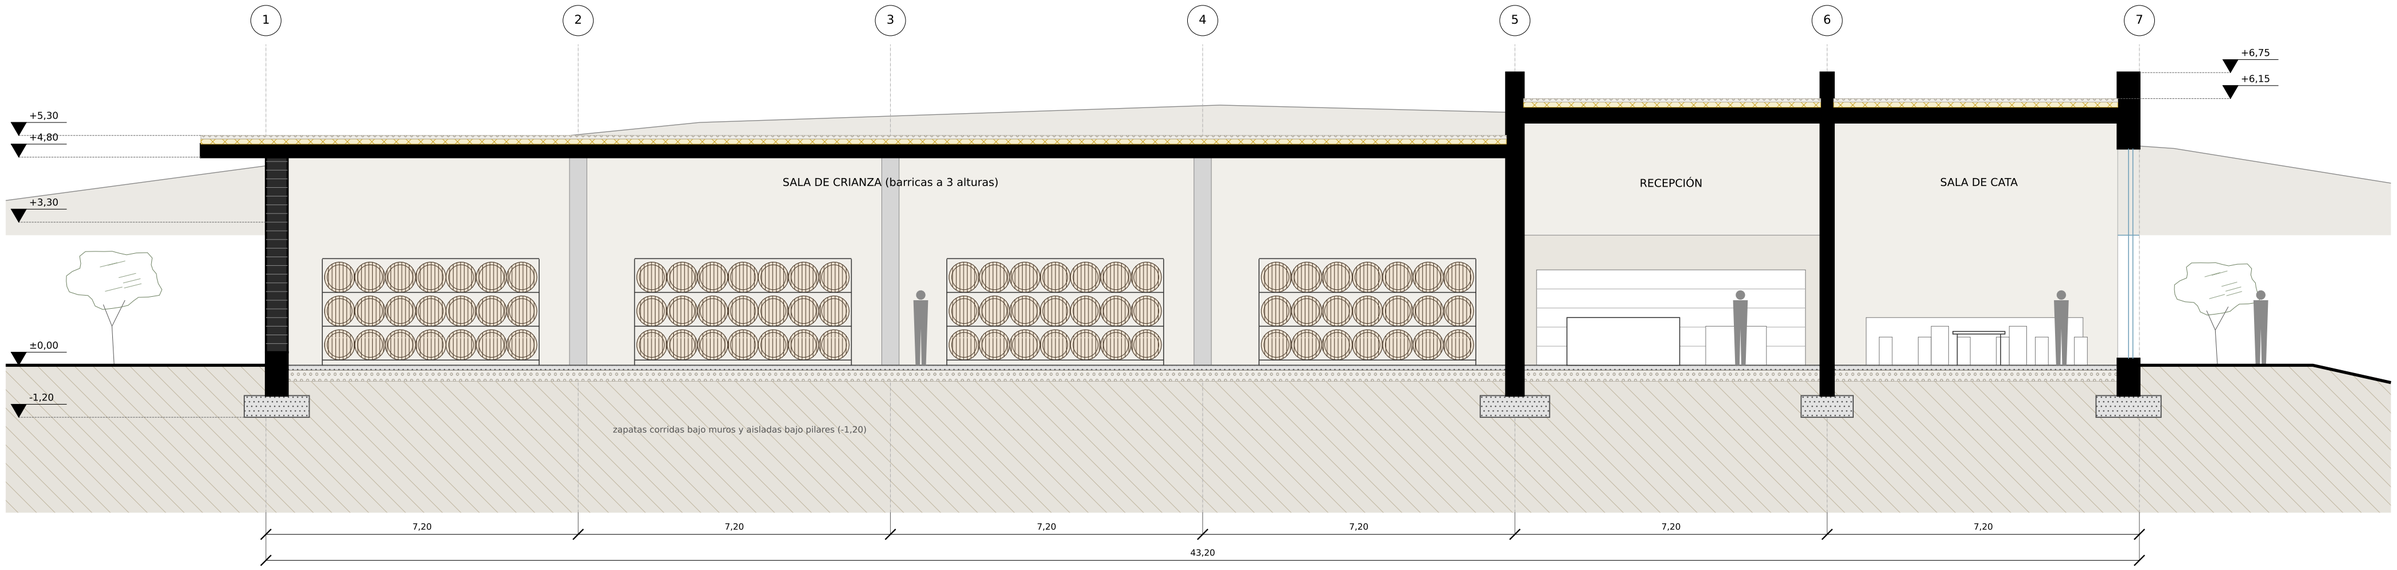


SECCIÓN LONGITUDINAL A-A'

E 1:100

0 1 2 5 10 m

PREDIMENSIONADO ESTRUCTURAL

Elemento	Luz / altura	Dimensión	Comprobación
Losa maciza sala, HA-30	2 x 6,00 m; vuelo 2,00 m	canto 30 cm (L/20; vuelo L/7)	q ≈ 11,5 kN/m²; punzonamiento en pilar OK con ábaco de 1,2 m
Pilar sala (3 ud.)	h = 4,80 m; área trib. 43 m²	40 x 40 cm, HA-30	N ≈ 500 kN → σ = 3,1 MPa < 20 MPa
Losa pabellones, HA-30	6,85 m (un solo vano)	canto 35 cm (L/20)	apoyada en muros de hormigón
Dintel-marco sur pabellón	7,20 m	viga-pared 50 x 175 cm	canto L/4: viga de gran canto
Muro contención norte	h = 5,10 m; tierra 4,60 m	e = 50 cm, HA-30	M ≈ 100 kN·m/m (apoyado en forjado) → Ø16/15
Muro de tierra apisonada	h = 3,30 m (sur y oeste)	e = 50 cm, 6 % cemento	40 kN/m → 0,08 MPa < 1 MPa; esbeltez 6,6
Zapata corrida	bajo muros	ancho 1,50 m, canto 50 cm	σ ≈ 55 kPa < 200 kPa (a confirmar con geotecnia)

CASO_011 · PROPUESTA C	**S01**
Sección longitudinal A-A'	E 1:100 · Anteproyecto